



THÉOLADE

Maëva

Étudiante en 5e année d'Architecture d'Intérieur et
Scénographie

PORTFOLIO

Depuis toujours, je suis sensible à la manière dont les espaces influencent nos émotions, nos mouvements, nos échanges. L'architecture d'intérieur est pour moi une manière de raconter une histoire à travers les volumes, la lumière, les matières et les sons.

Mon parcours est nourri par une recherche constante d'équilibre entre esthétique, usage et sens. J'aime imaginer des ambiances immersives, jouer avec les contraintes pour en faire des opportunités créatives, et concevoir des lieux qui laissent une empreinte sensible à celles et ceux qui les traversent.

Ce portfolio est le reflet de mon univers, de mes expérimentations et de ma vision du design : un design sincère, réfléchi, et tourné vers l'humain. Il rassemble des projets variés, pensés avec soin, qui témoignent de mon évolution et de mon engagement dans cette discipline exigeante et passionnante.

SOMMAIRE

FLUENCE

WAVEWOOD

L'ATTENTE, REPENSÉE

LUMIÈRE MATINALE

SOAPBOTTLE

CABINET

AT HOME

FLUENCE

L'HARMONIE ENTRE L'EAU, LE BOIS ET LA LUMIÈRE


Lieu : Vancouver, Canada (projet fictif)

Contexte : Expérimentation d'un espace fluide en bois, autour du mouvement et de la matière

Durée : Projet personnel – 2 semaines

Ce projet propose une expérience immersive où sport, détente et convivialité se rencontrent dans un même lieu. L'architecture met en valeur des matériaux nobles comme le bois, créant une atmosphère chaleureuse et raffinée. L'espace s'organise autour de trois pôles distincts : **une piscine** élégante au cœur du projet, **une salle de sport** intégrée pour une approche complète du bien-être, et **un espace de restauration** pensé comme un lieu de rencontre et de relaxation. L'harmonie entre les textures et la lumière sublime l'ensemble, offrant un cadre apaisant et sophistiqué.




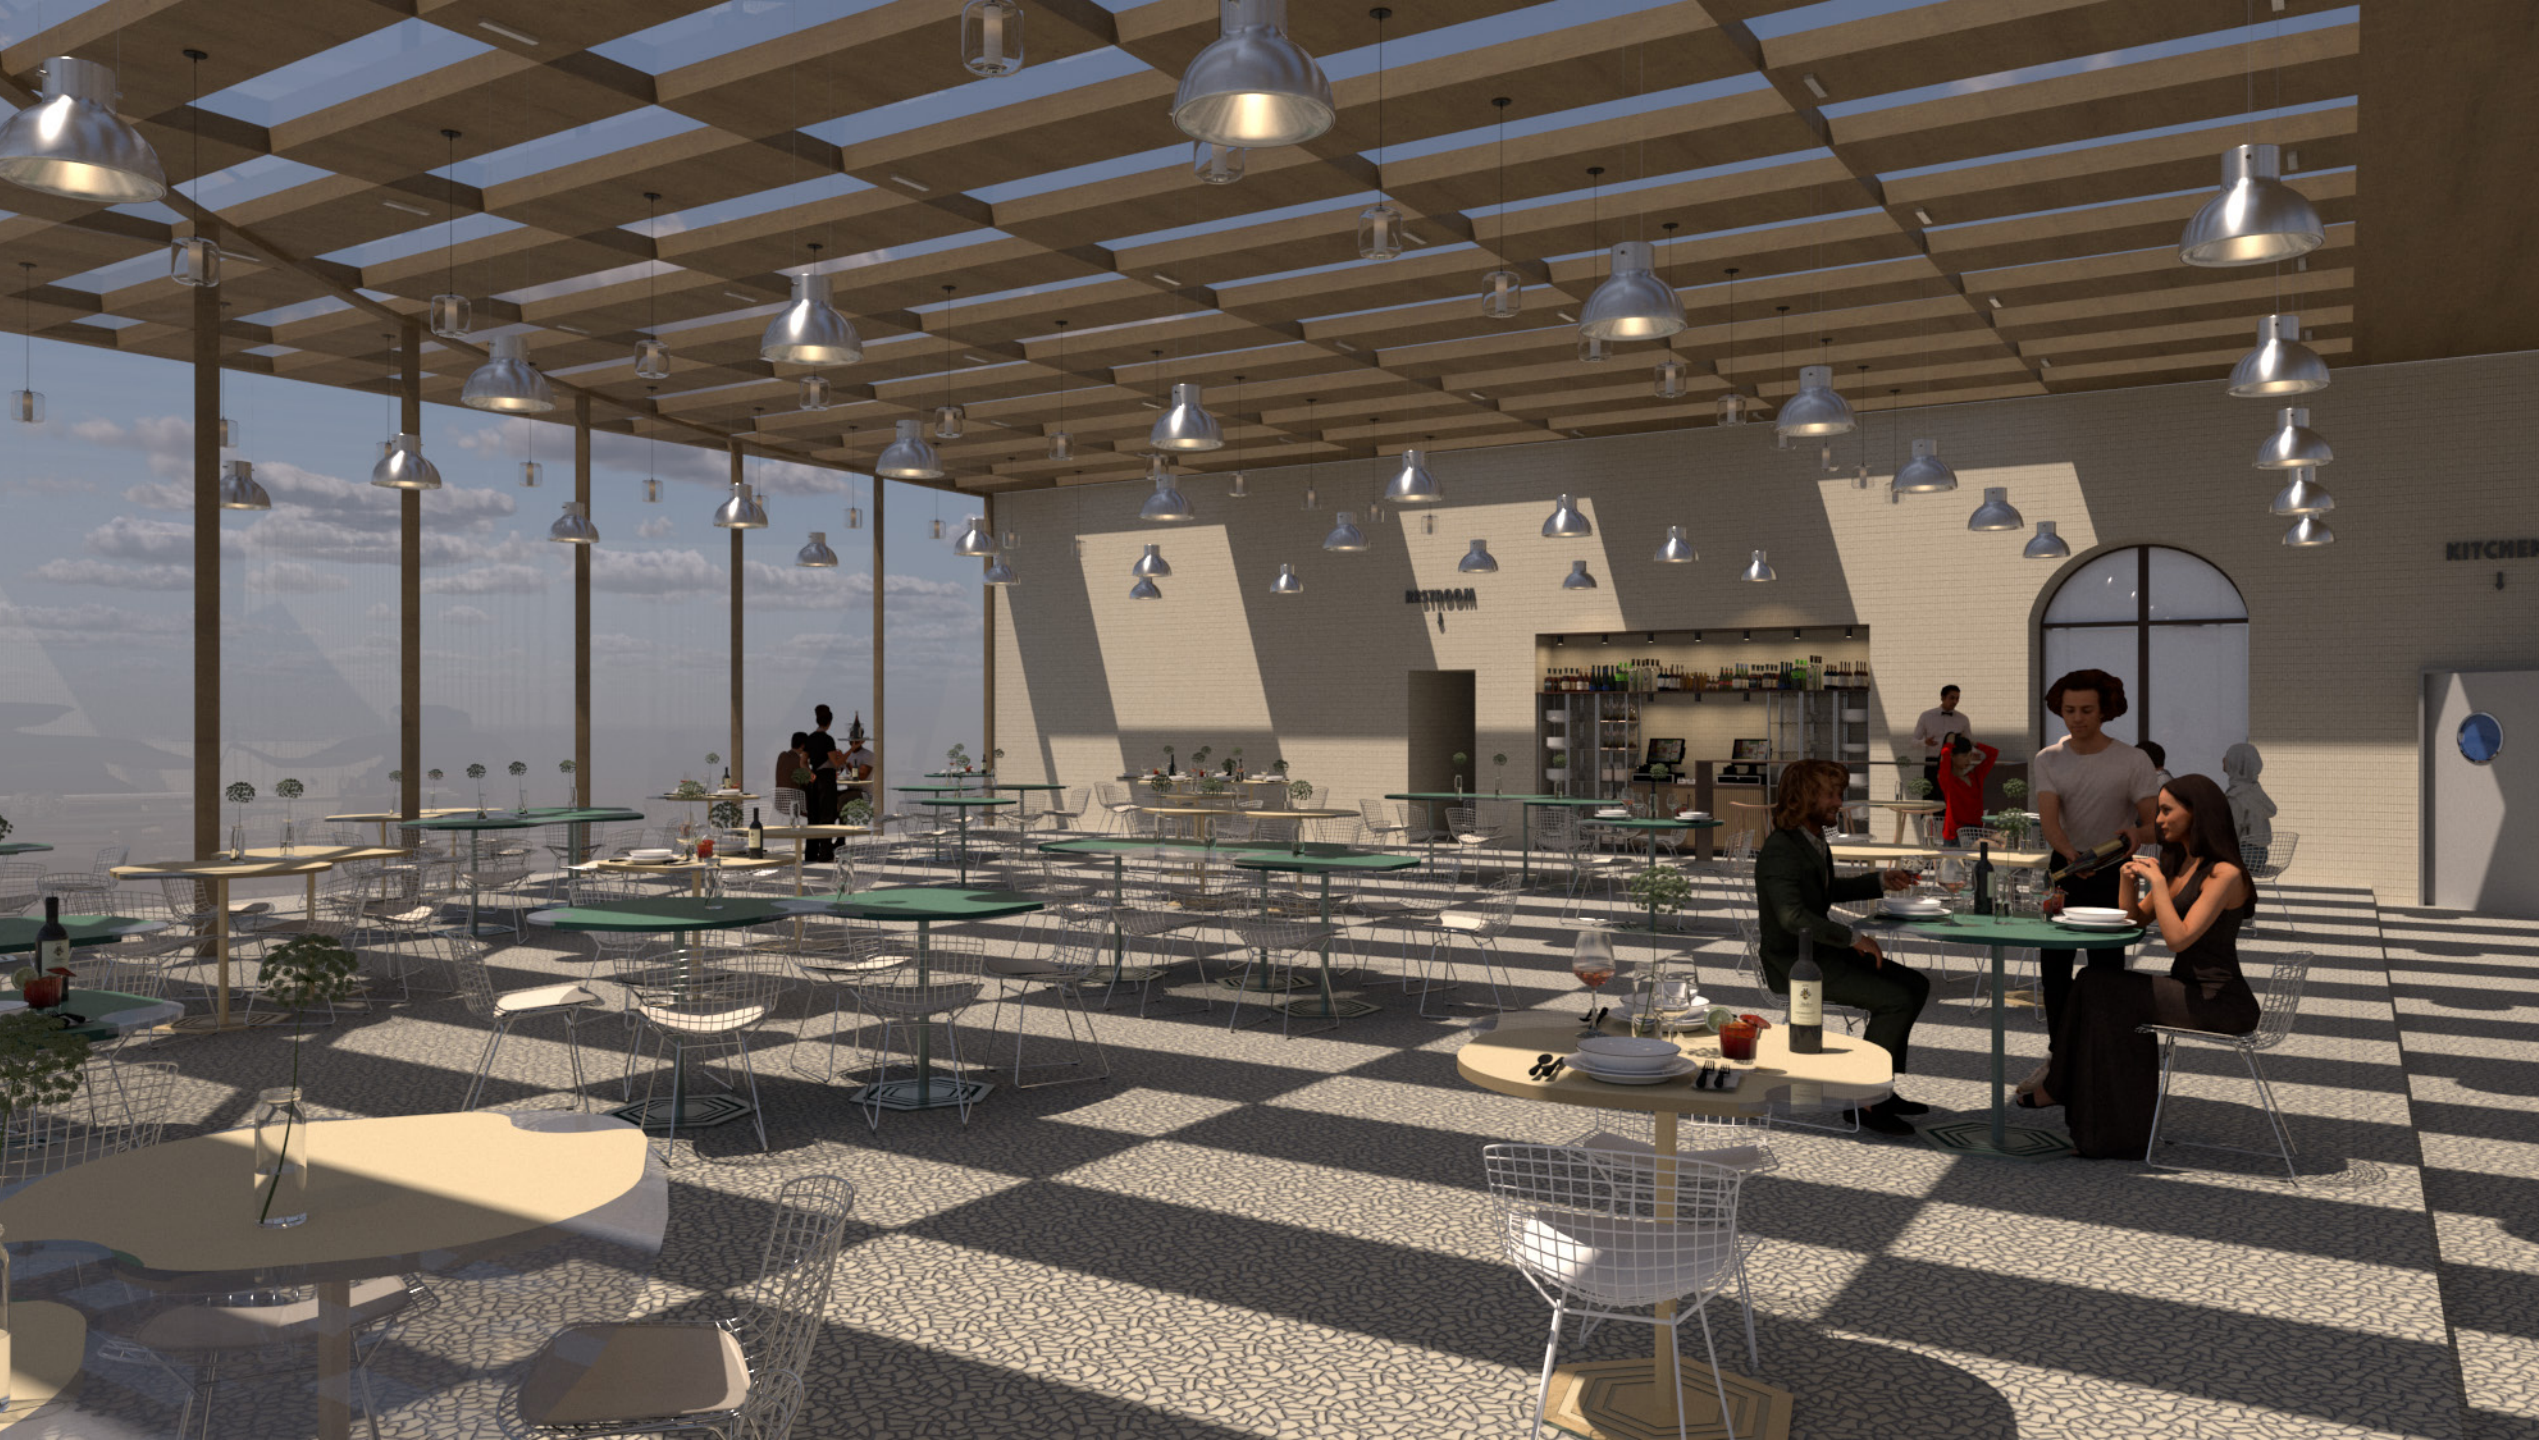

RESTAURANT



SALLE DE SPORT

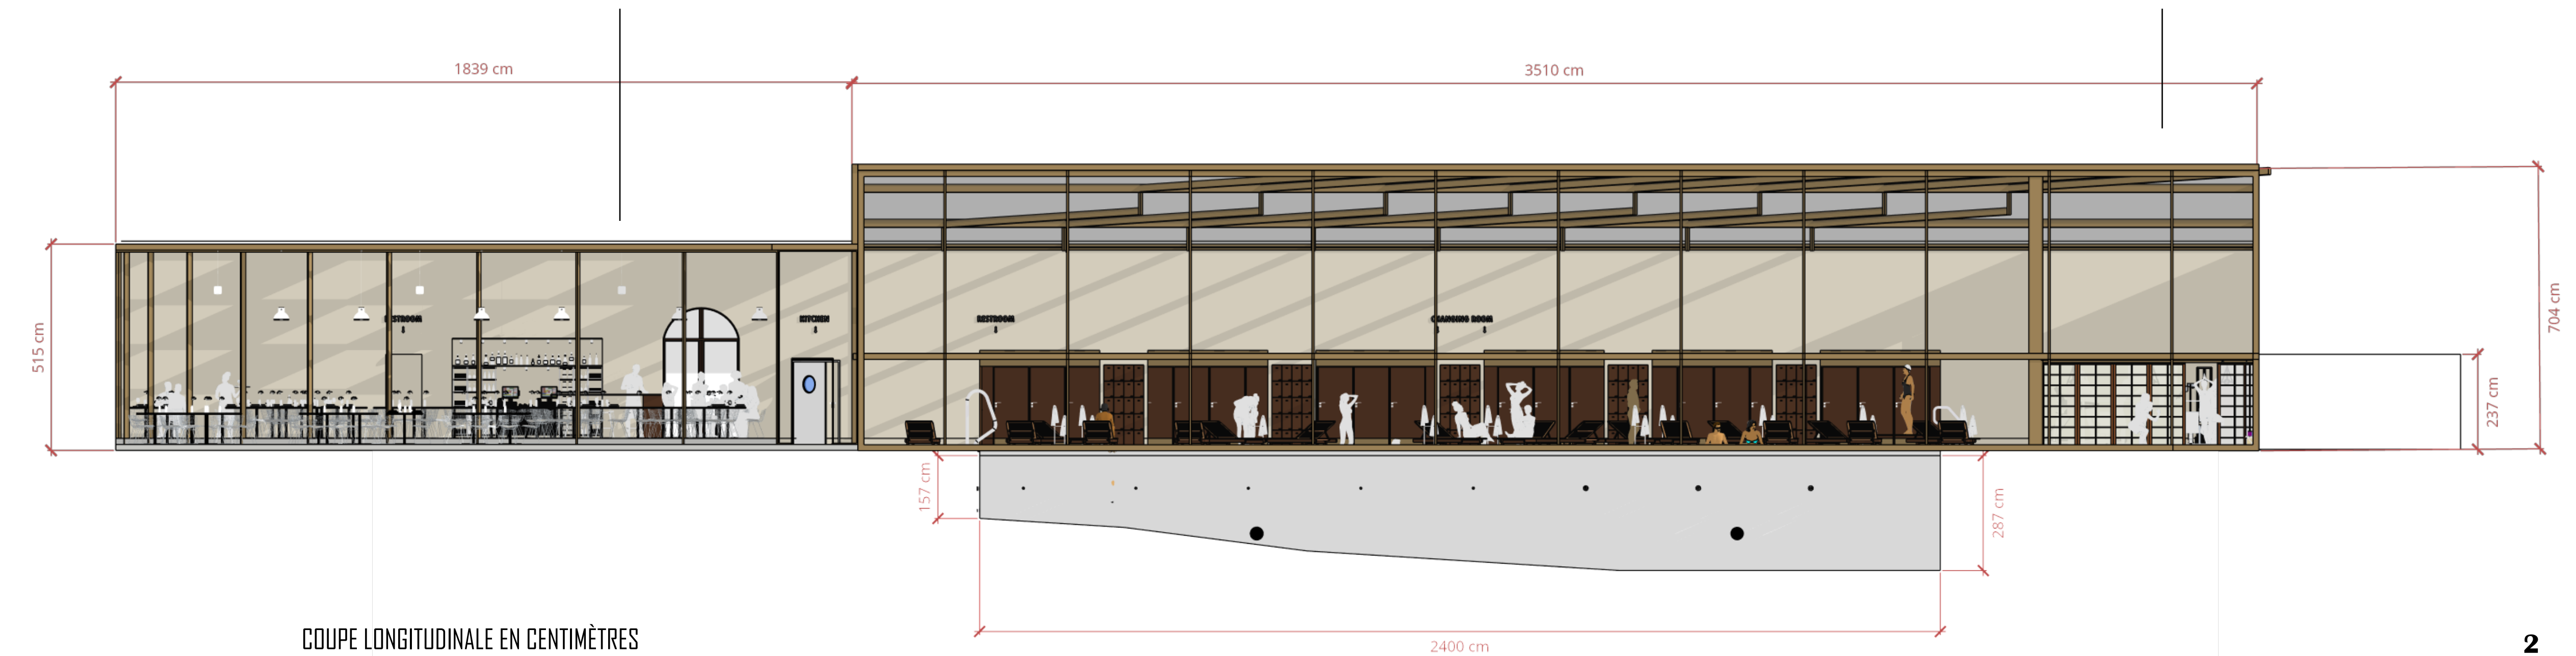

COUPE LONGITUDINALE EN CENTIMÈTRES



WAVEWOOD

L'ESSENCE DU BOIS EN MOUVEMENT

Lieu : Île d'Oléron, France (projet fictif)

Contexte : Expérimentation d'un espace fluide en bois, autour du mouvement et de la matière

Durée : Projet personnel – 2 semaines


Ce projet réaménage l'entrée d'une maison en un grand espace de vie composé d'un salon, d'une salle à manger et d'une cuisine ouverte.


Les différentes zones sont définies par la géométrie du plan et la fluidité de la circulation, dans un volume aux **murs en béton brut**.

De larges ouvertures latérales diffusent une lumière naturelle constante, animée par les ombres projetées des **poutres courbes en bois** apparentes au plafond.

Le mobilier intégré prolonge les lignes architecturales et renforce la cohérence de l'ensemble.



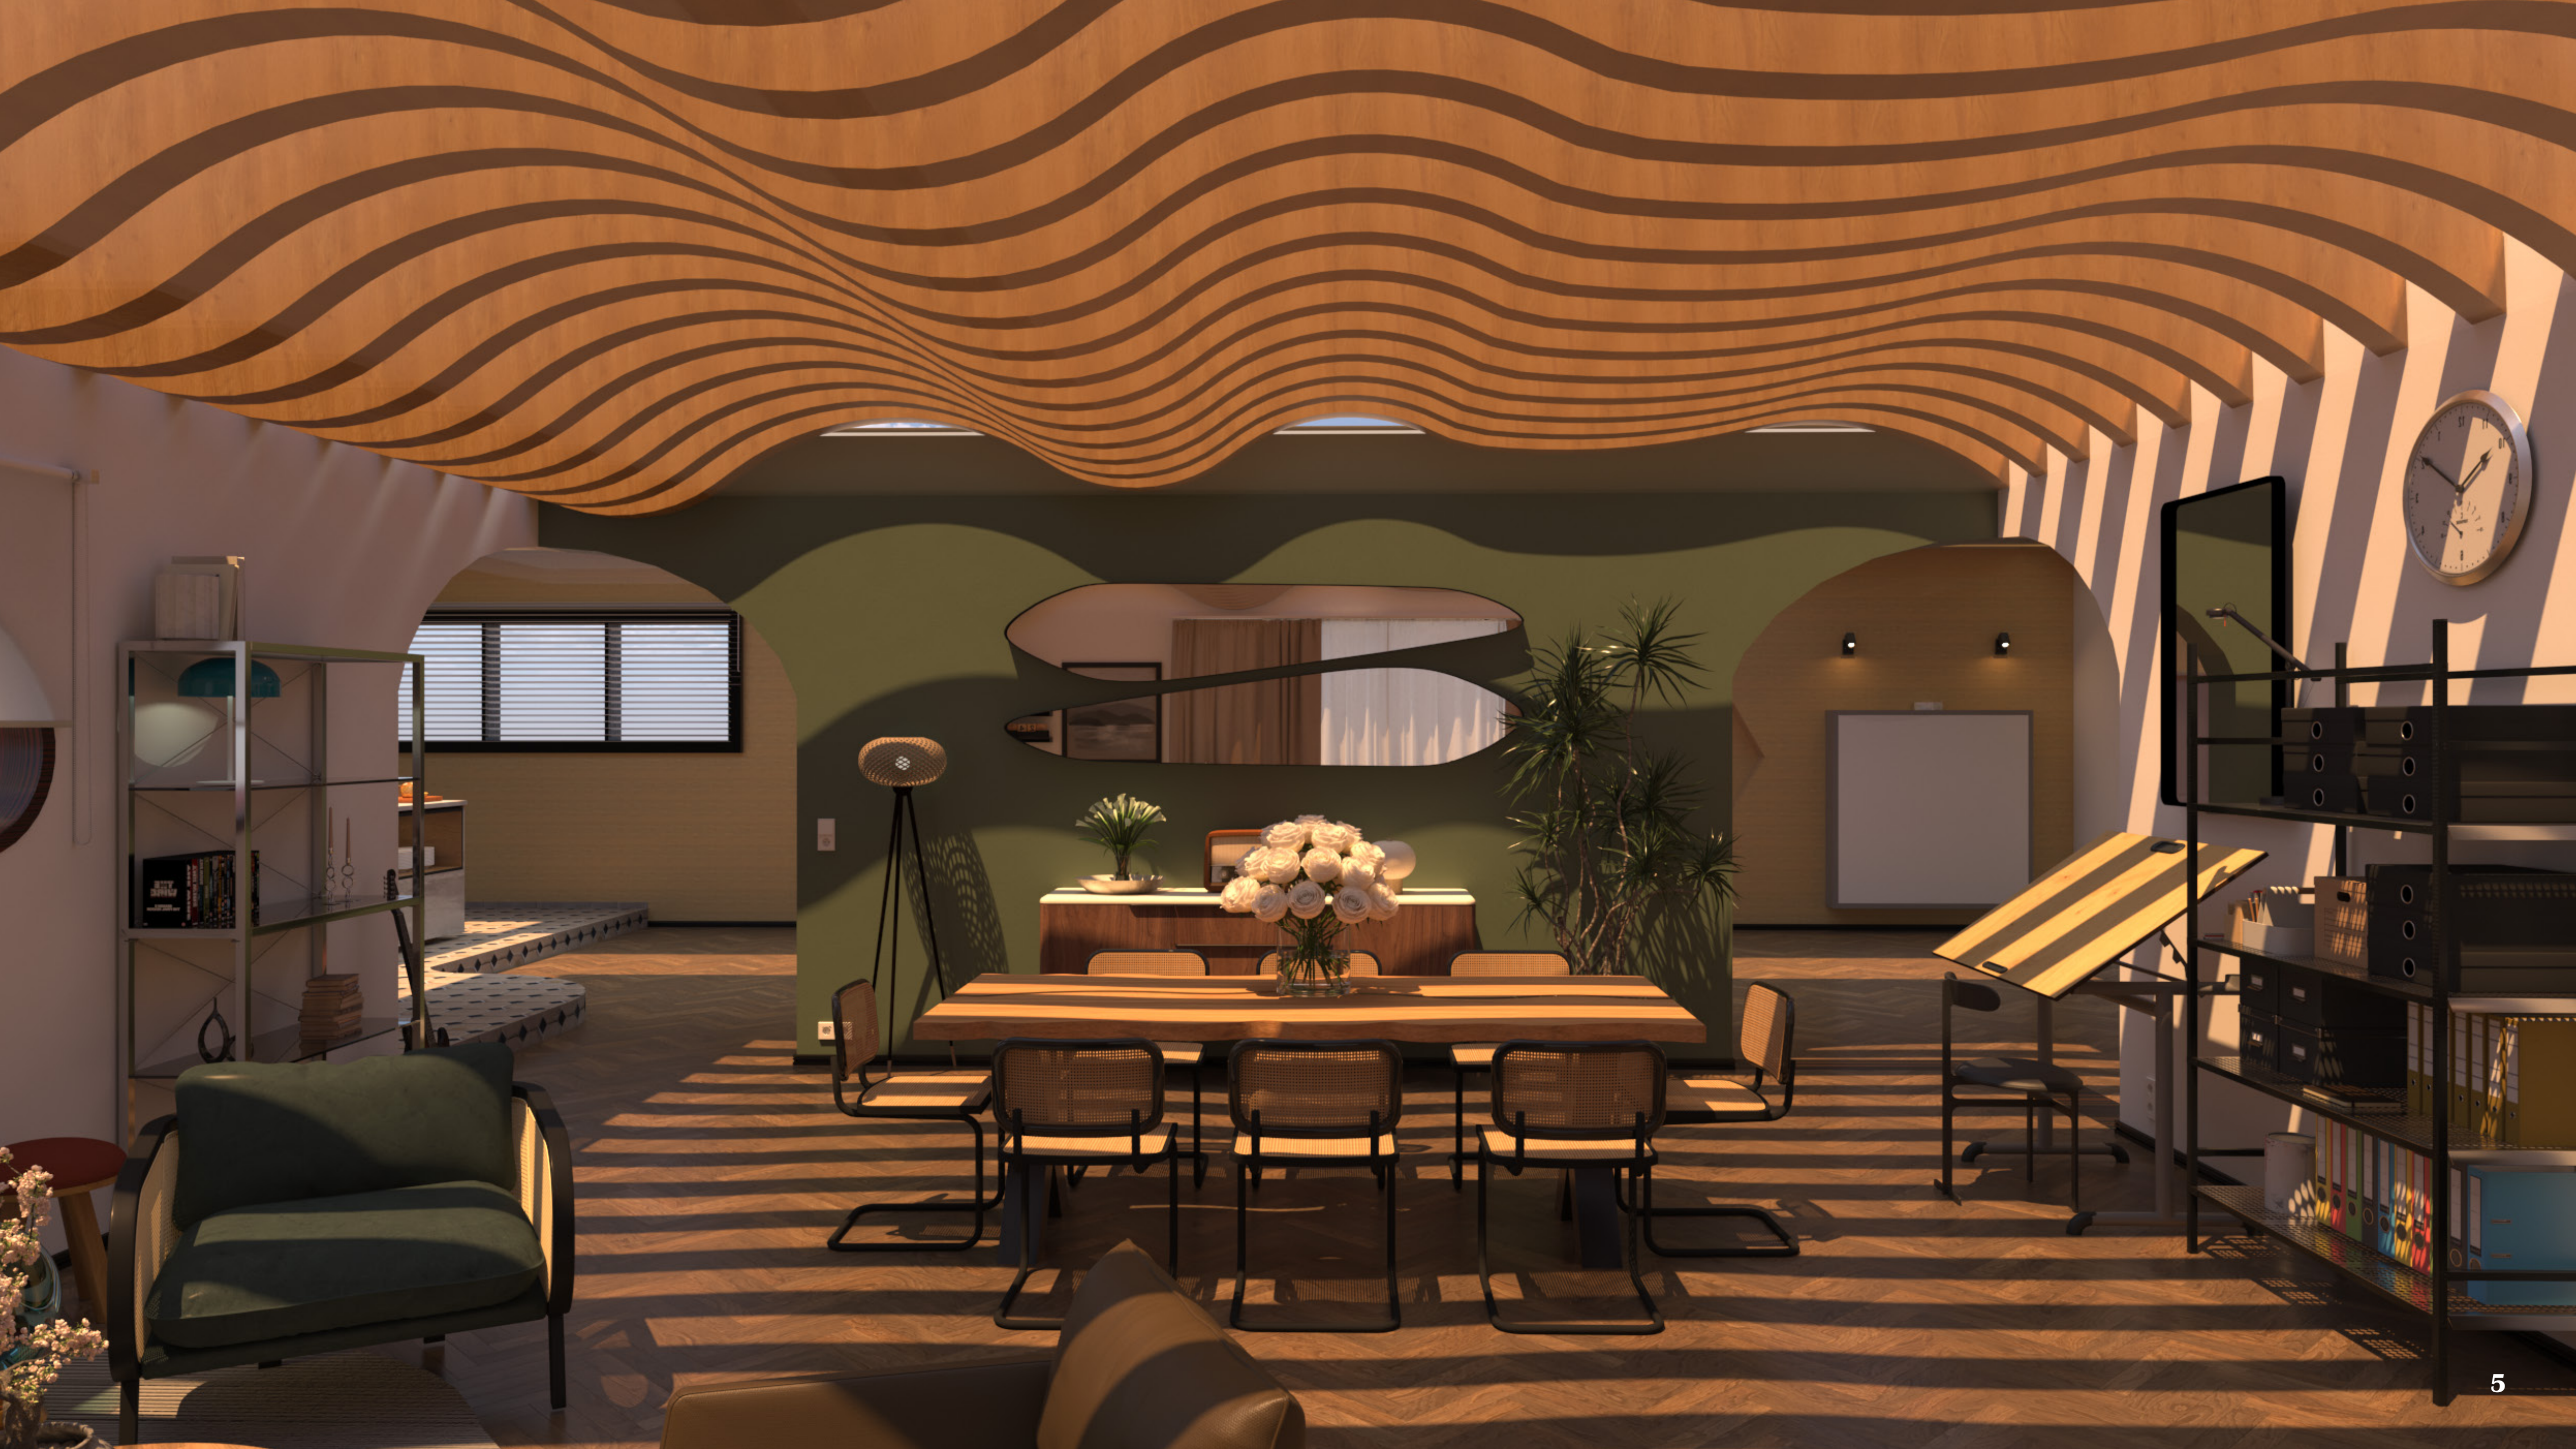

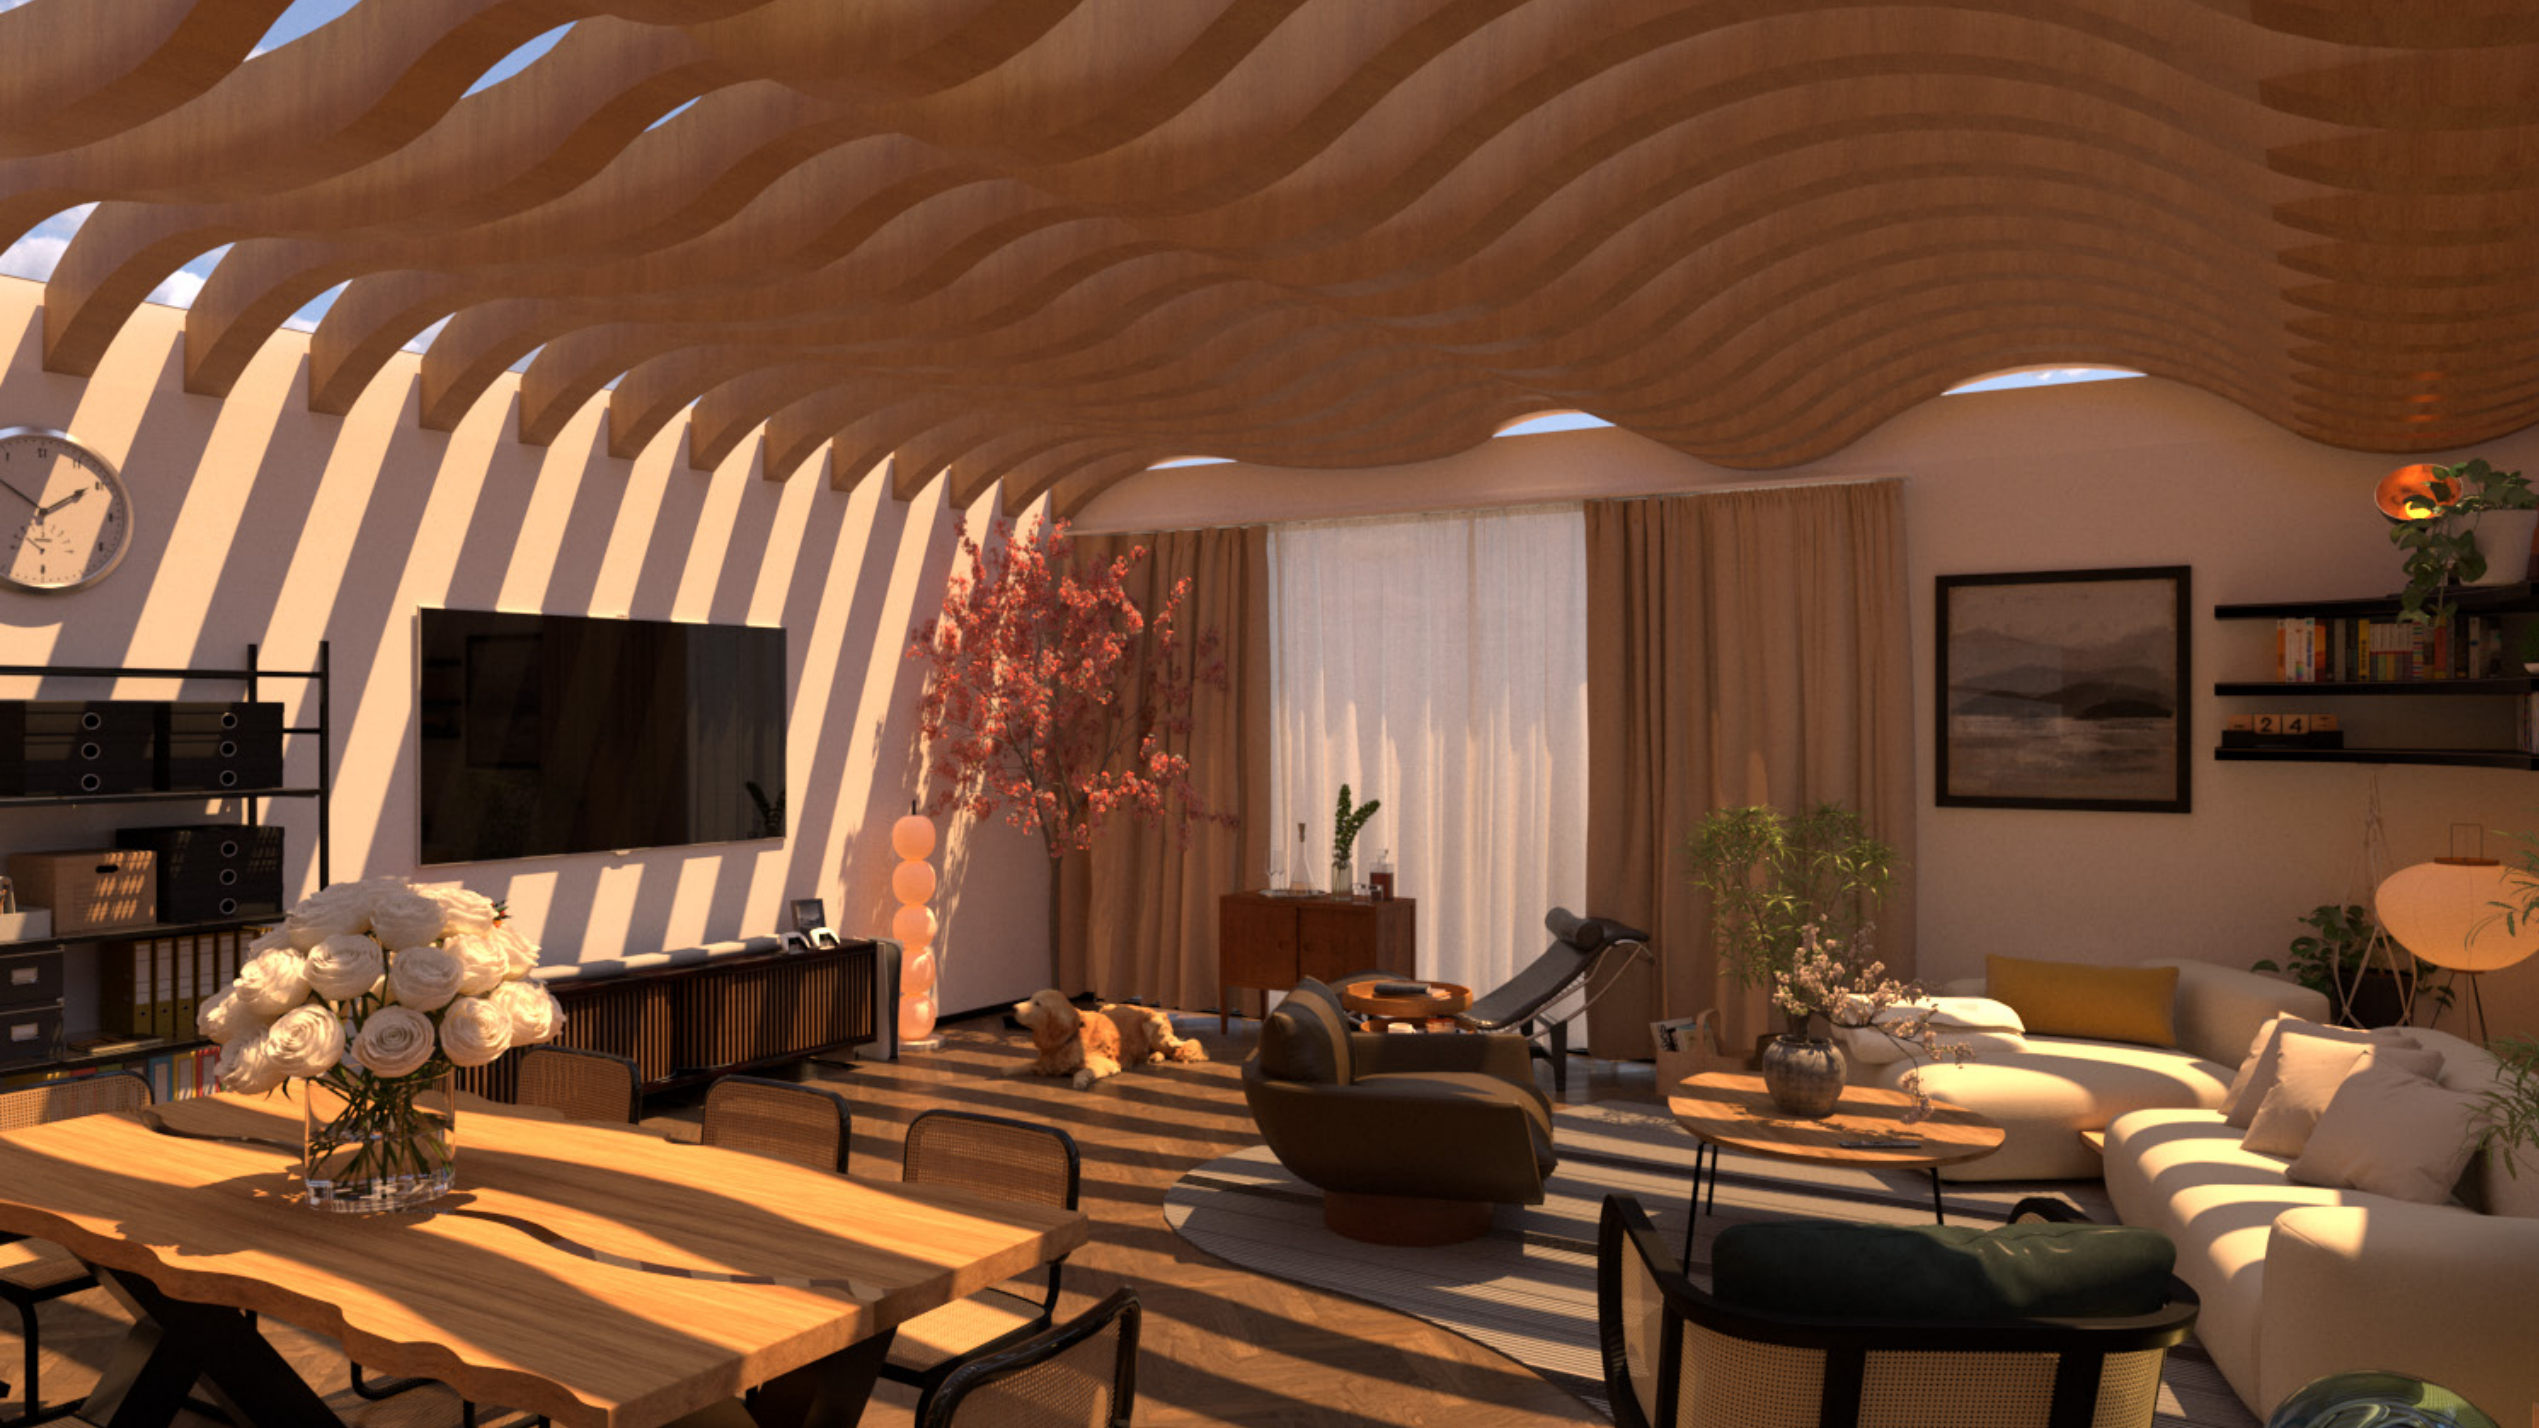

L'ATTENTE, REPENSÉE

UN ESPACE DE TRANSITION POUR APAISER LES VOYAGEURS

Lieu : Gare de Surgères, France (projet fictif)


Contexte : Réaménagement de l'espace d'attente pour améliorer le confort des voyageurs

Durée : Projet académique – 6 semaines


Ce projet réinvente l'espace d'attente de la gare de Surgères, en s'adressant particulièrement aux **voyageurs anxieux** ou **peu familiers avec le train**. **Trois zones** distinctes permettent une **transition progressive** : des assises hautes pour les départs imminents, un espace assis pour une attente modérée, et une zone de détente avec des assises basses pour se relaxer pleinement. Une ambiance lumineuse et sonore accompagne le parcours, offrant une expérience **apaisante et immersive**.




COUPE TRANSVERSALE

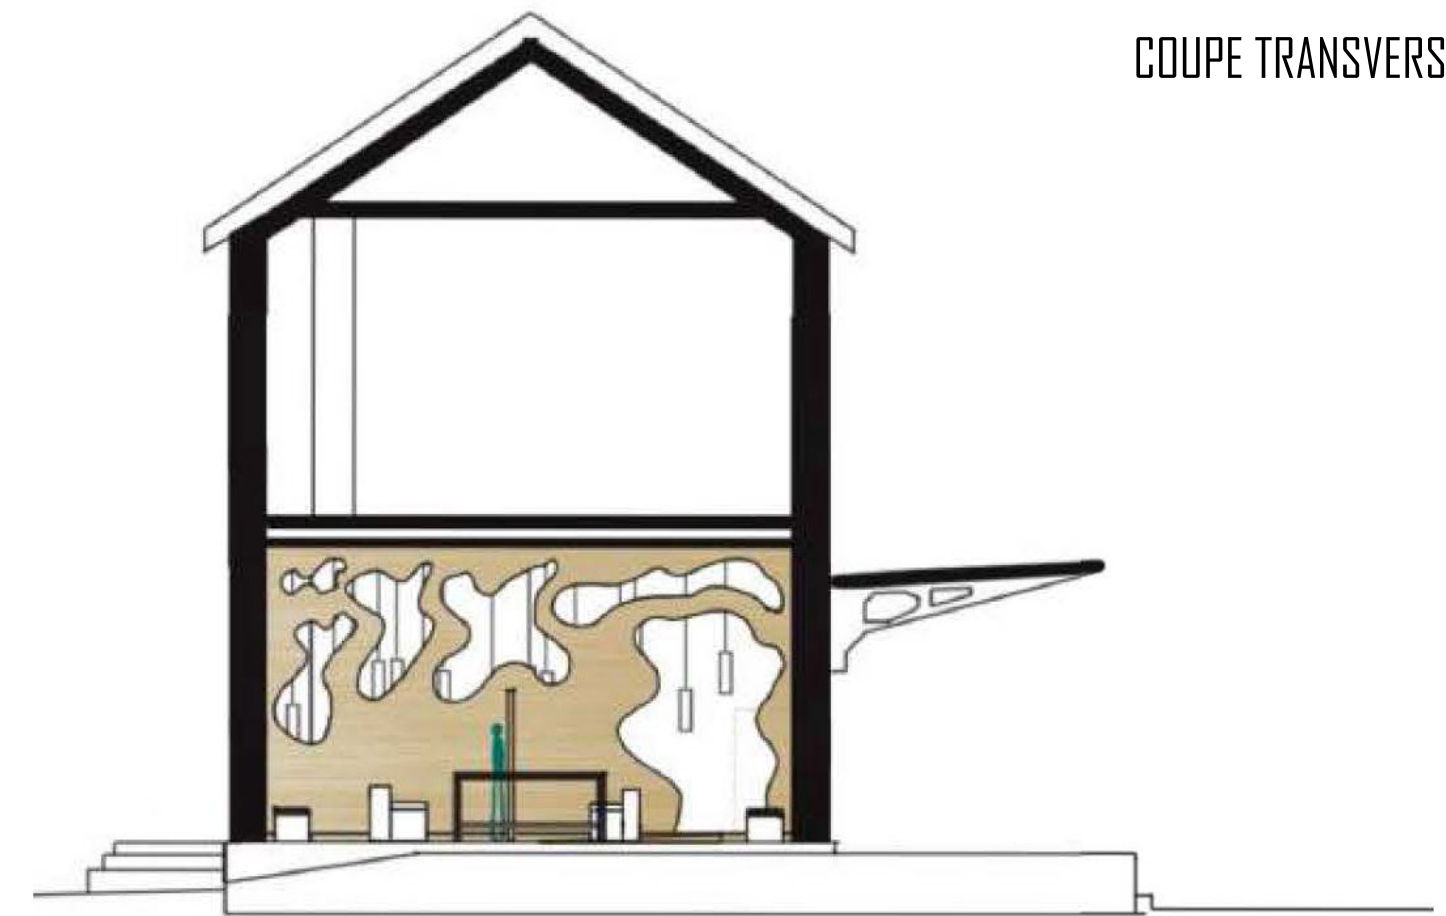

PLAN

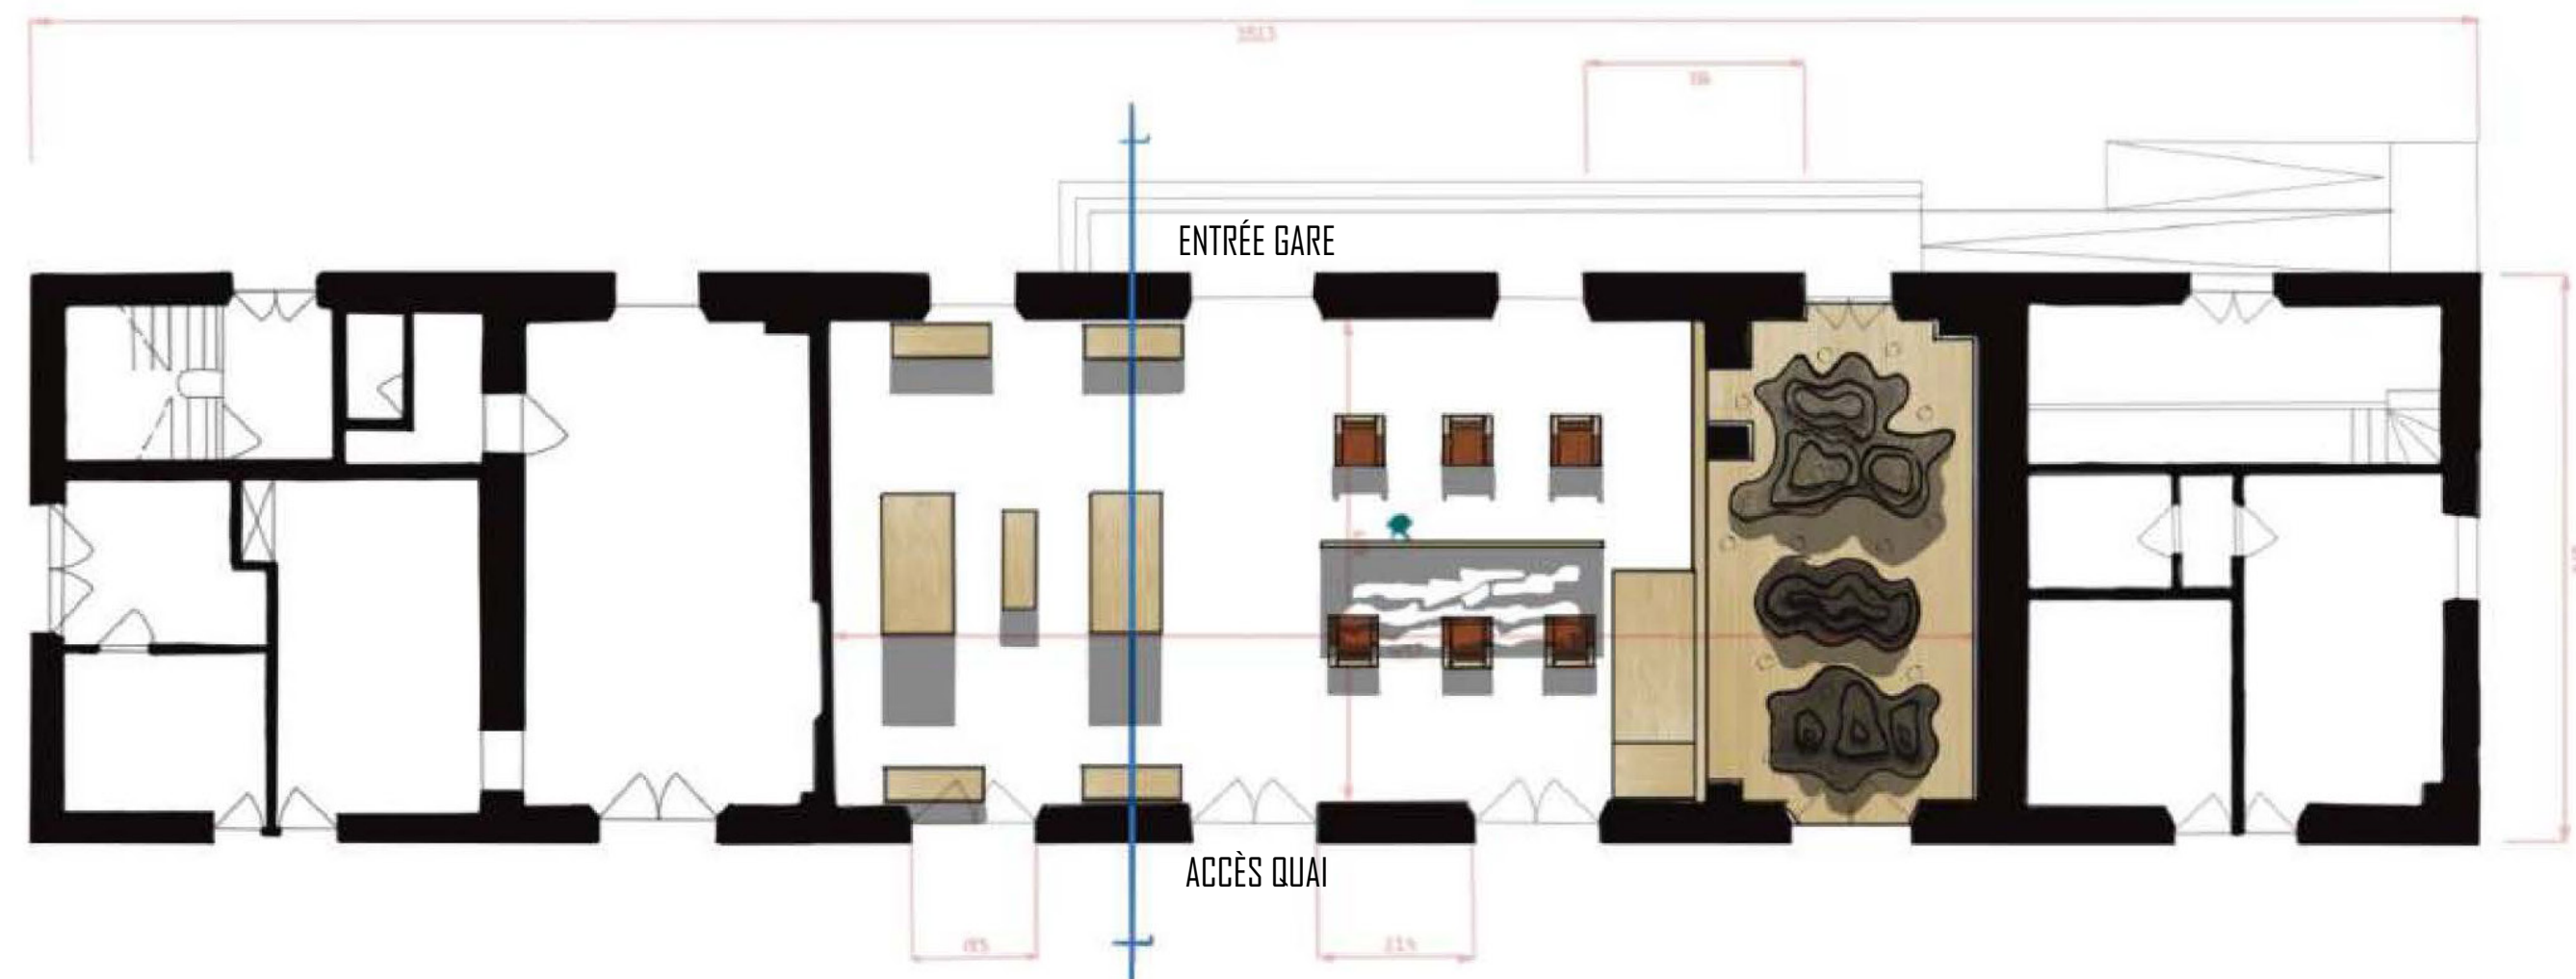

COUPE LONGITUDINALE

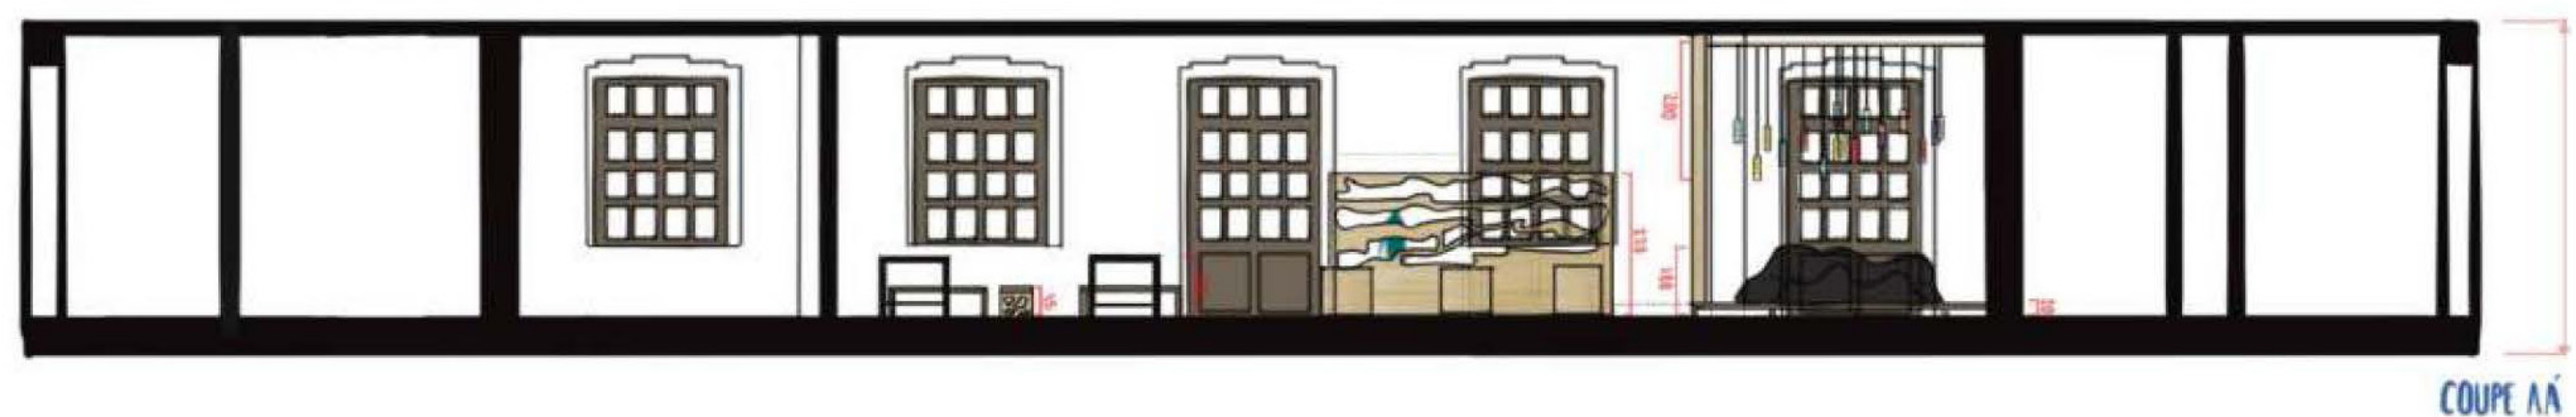

LUMIÈRE MATINALE


DOUCHE QUOTIDIENNE, CONFORT OPTIMAL

Lieu : Vincennes, France (projet fictif)

Contexte : Création d'une salle de bain optimisée autour de la lumière naturelle et du confort

Durée : Projet personnel – 2 jours

Ce projet de salle de bain propose un aménagement fluide et fonctionnel, avec un **mobilier entièrement encastré**. L'espace est structuré autour d'un **plafond incliné** et de **trois velux** qui laissent entrer la lumière du matin, idéale pour commencer la journée sous la chaleur du soleil. La circulation est optimisée grâce à de nombreux rangements discrets, sans encombrement. Une **grande hauteur sous plafond** au niveau de la douche renforce la sensation d'espace et de confort.

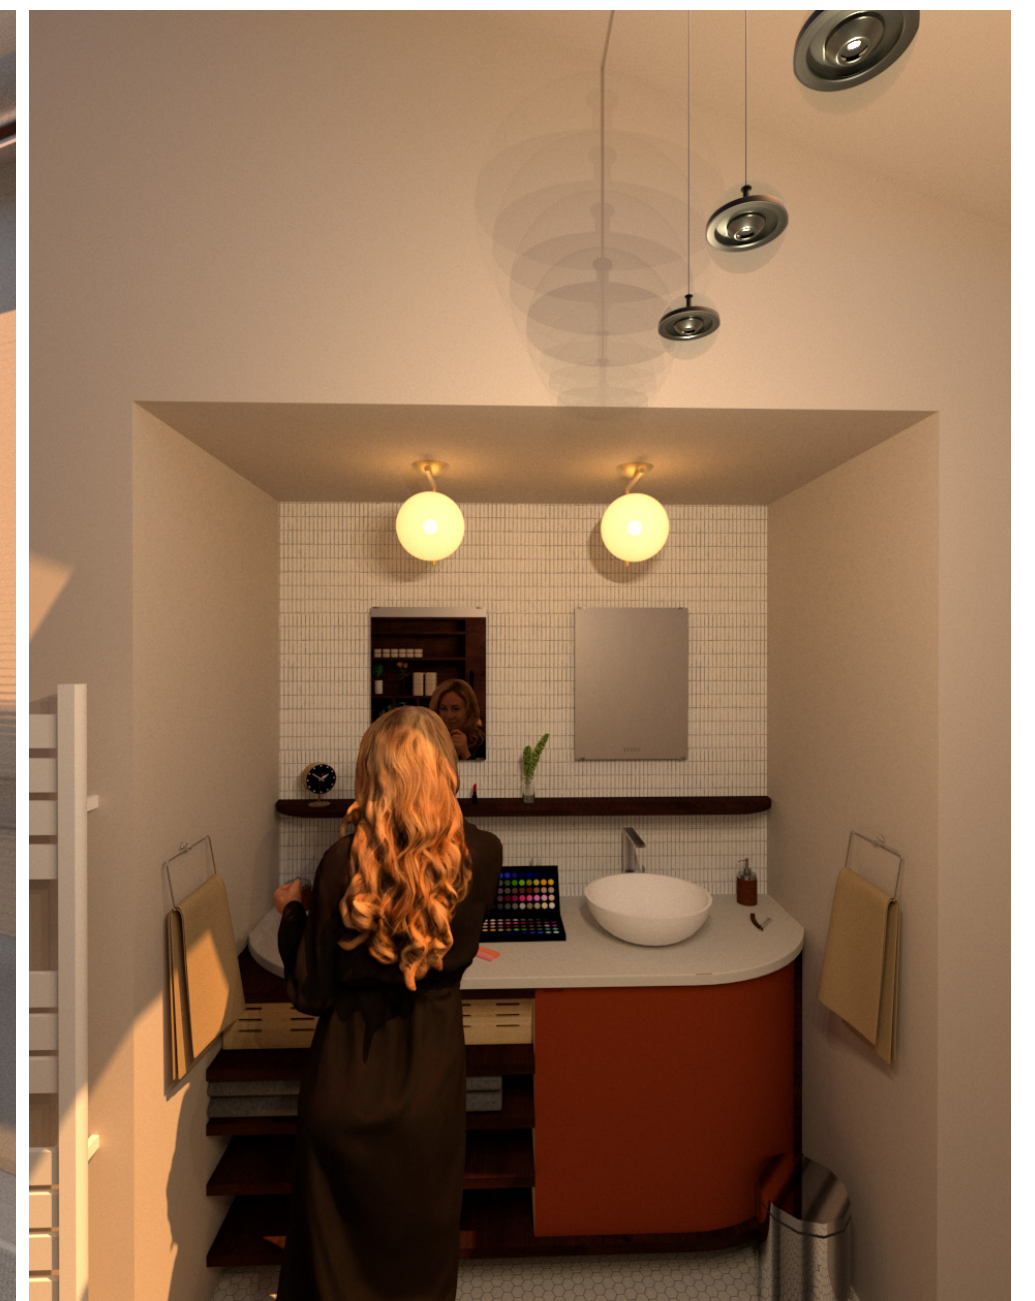

SOAPBOTTLE

UN STAND MINIMALISTE AU SERVICE D'UN PRODUIT DURABLE


Lieu : Paris, France (projet fictif - stand d'exposition)

Contexte : Réflexion autour de la scénographie produit dans un environnement éphémère et modulable

Durée : Projet académique (en binôme) – 1 semaine

Réalisé dans le cadre d'un projet de stand, cet espace met en valeur un produit **écoresponsable** autour d'un **concept minimaliste**. L'enjeu était de concevoir une **structure légère**, modulaire et facilement identifiable dans un contexte d'exposition. L'espace est optimisé pour la présentation produit tout en respectant une cohérence visuelle et environnementale.




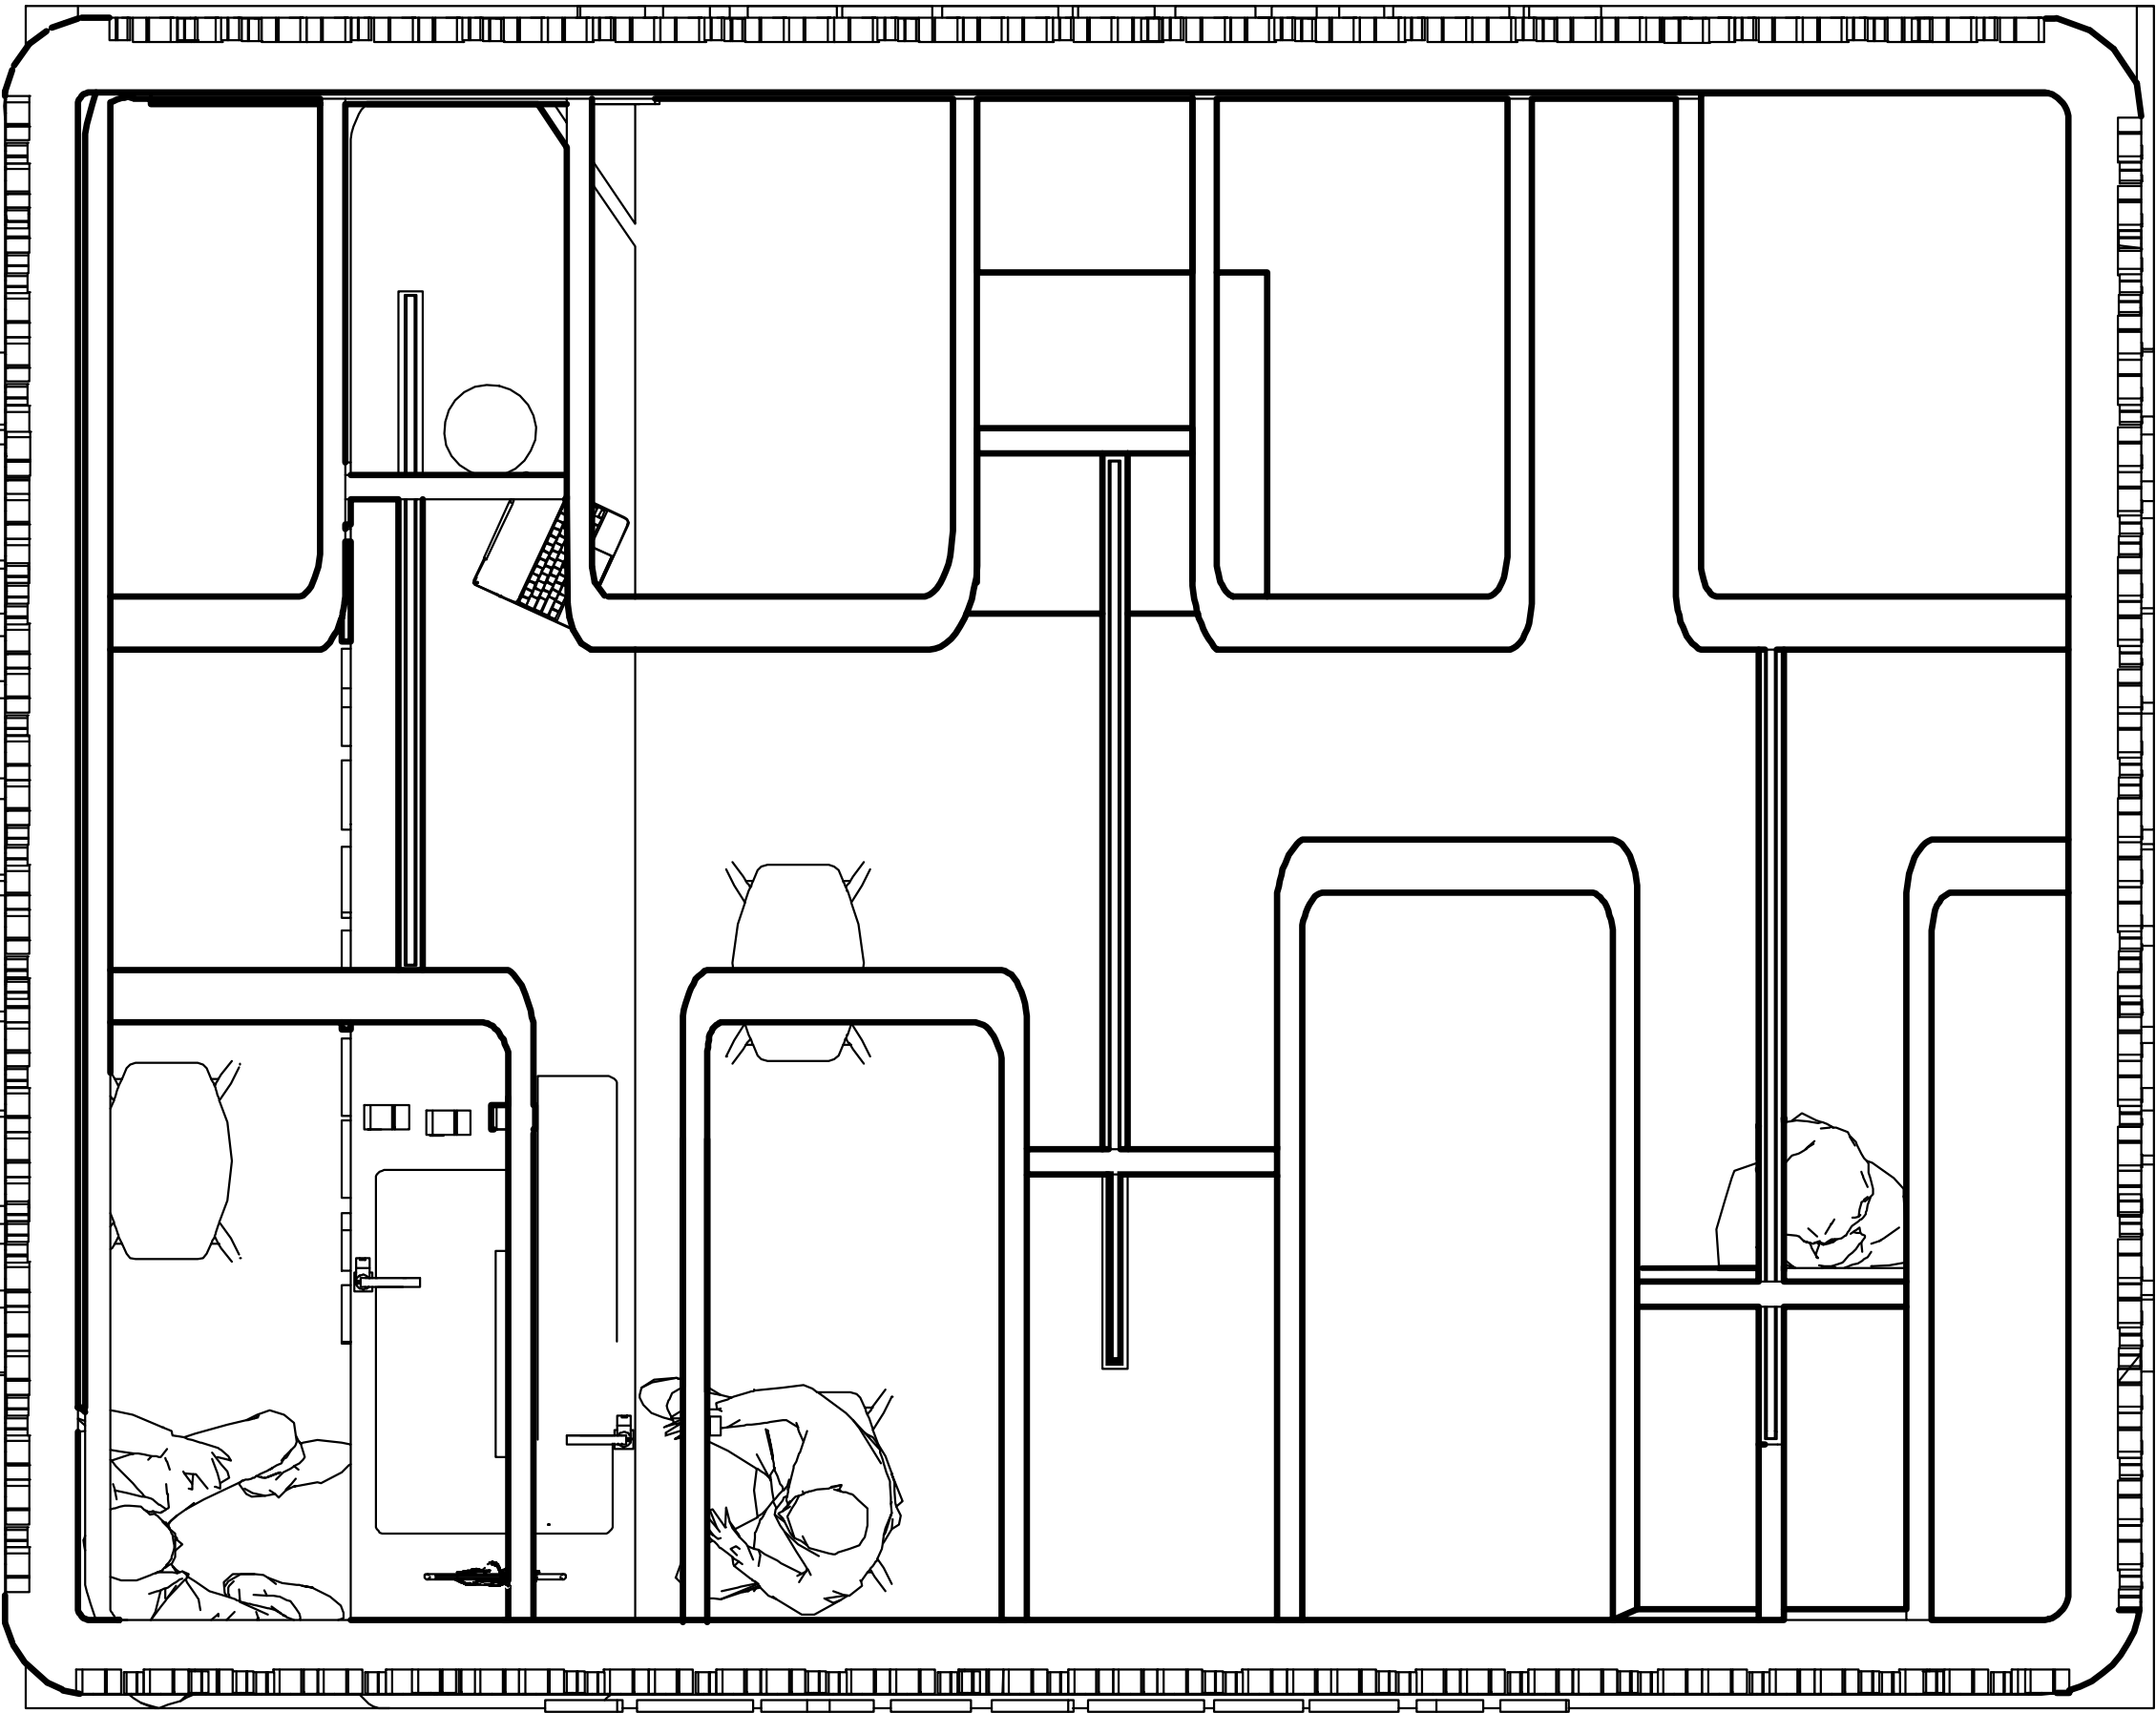

500

400

PLAN

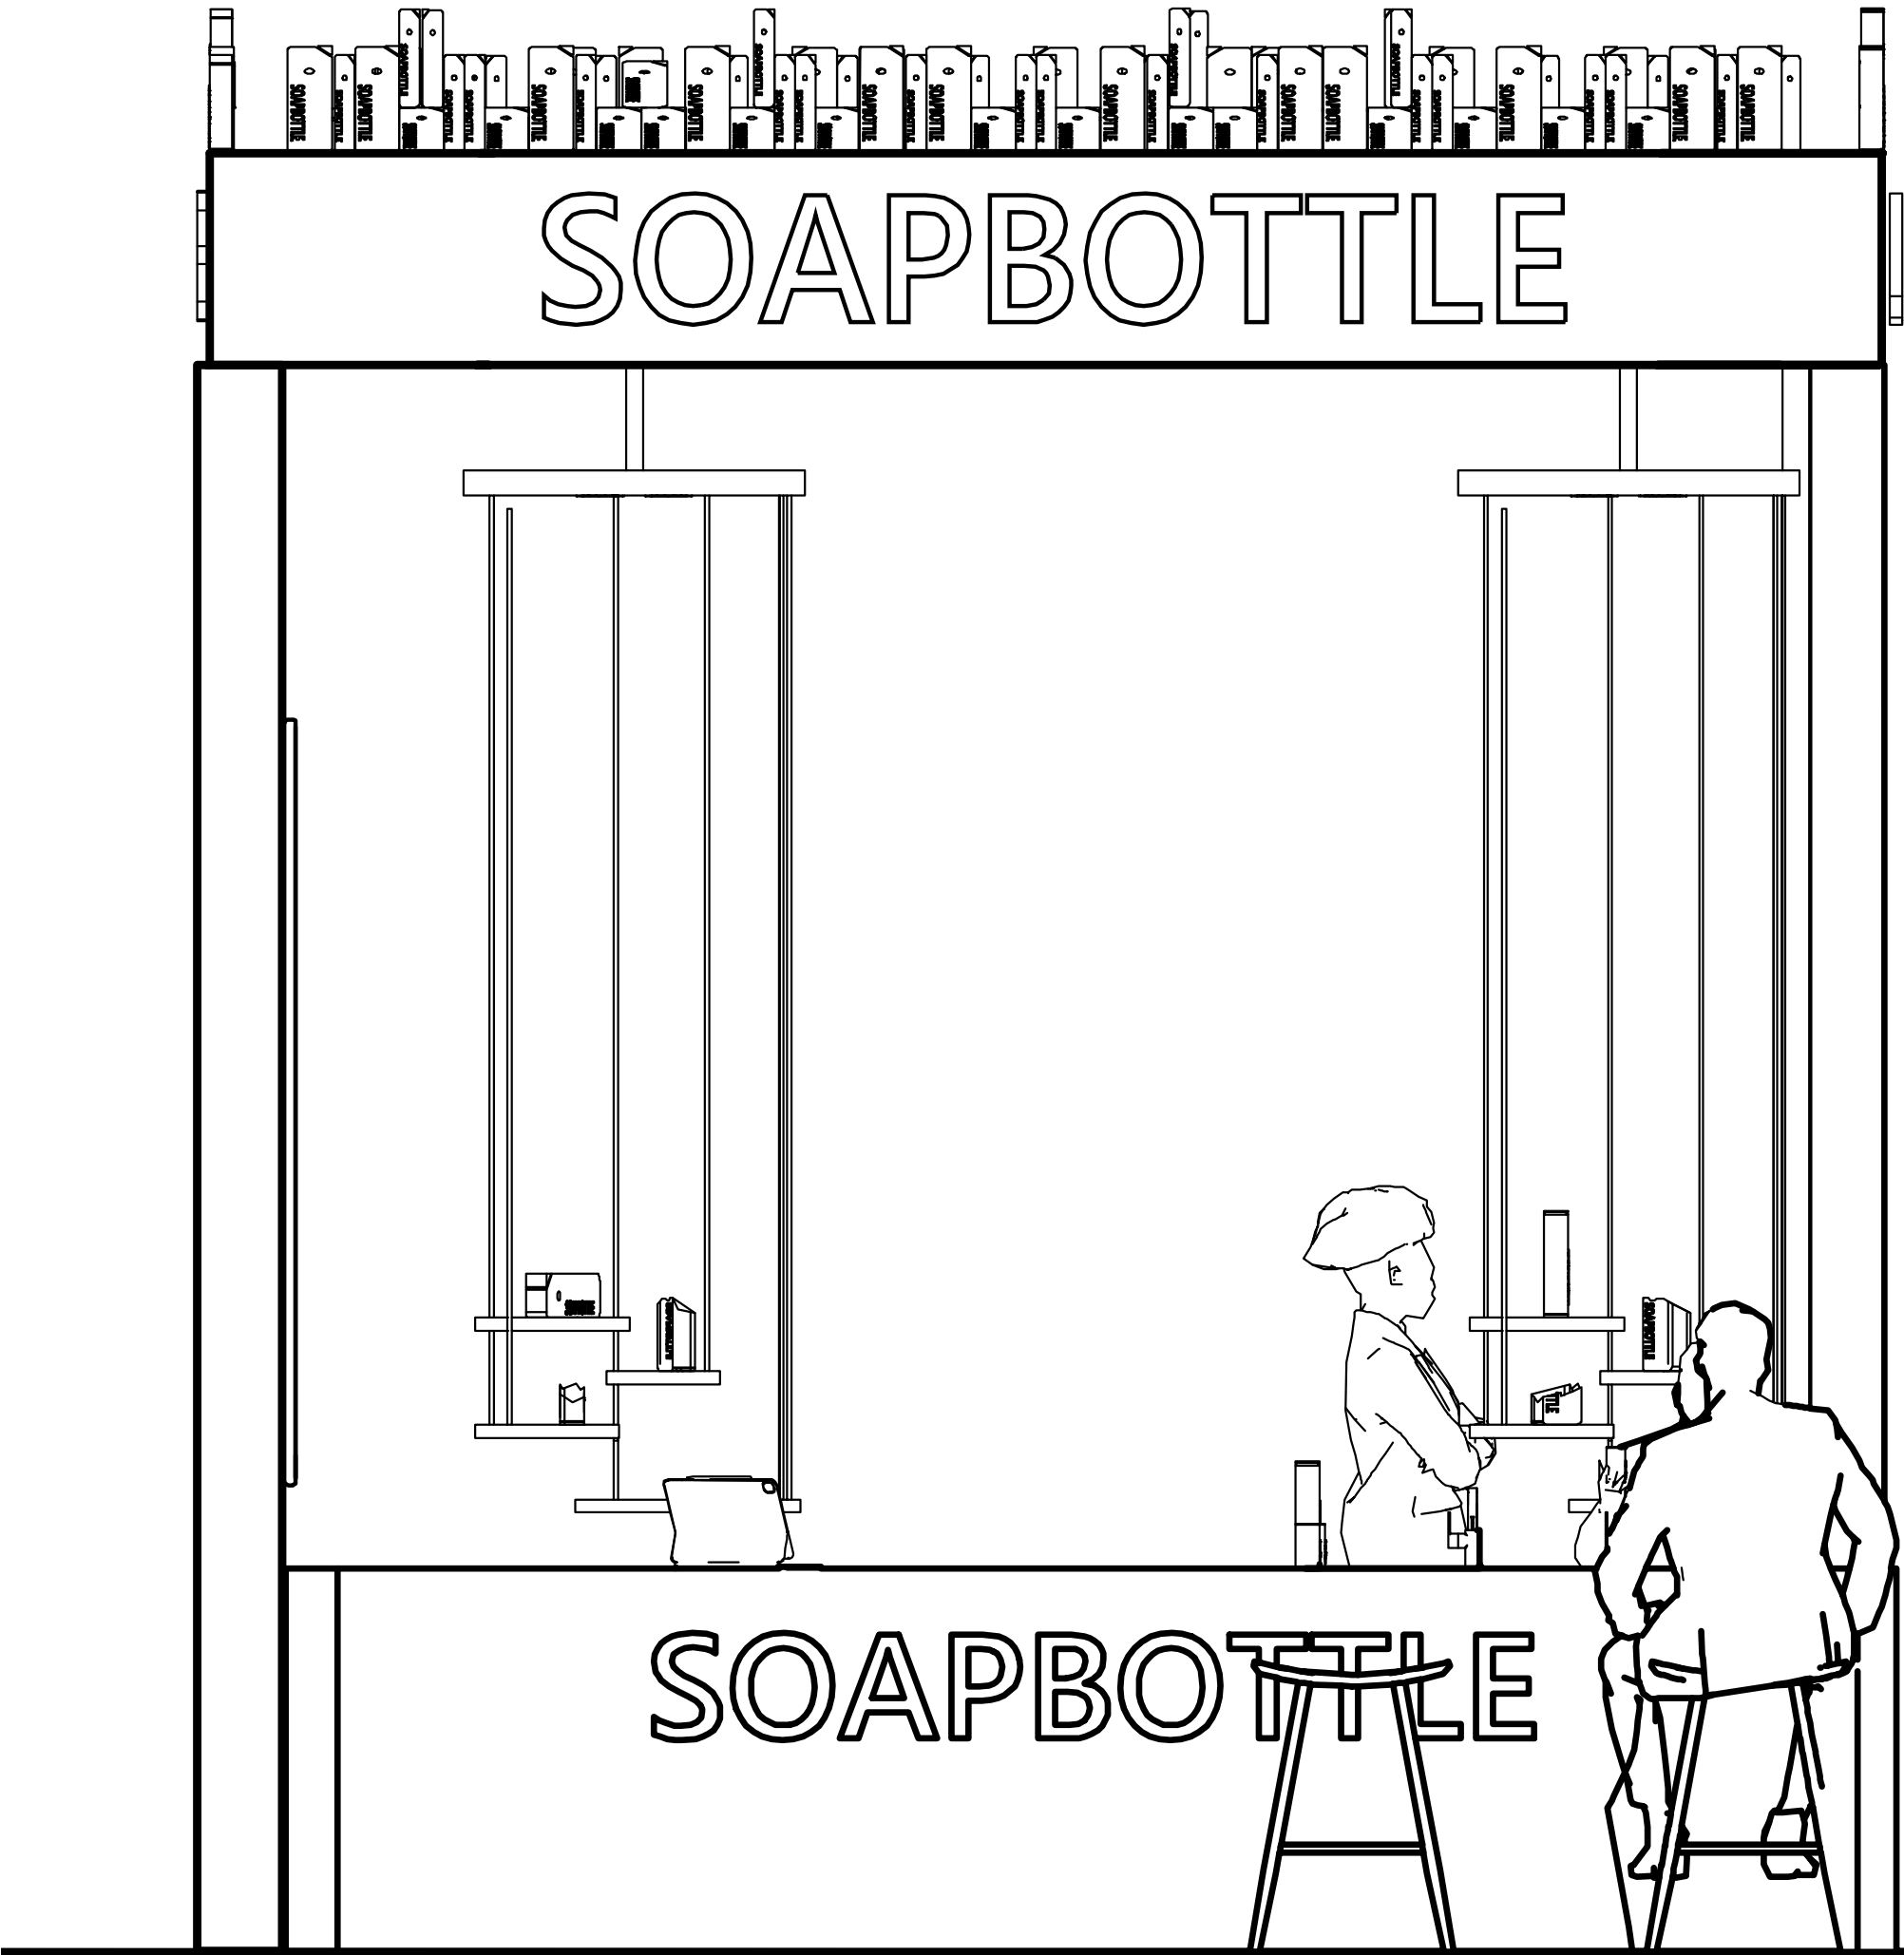

SOAPBOTTLE

SOAPBOTTLE

25

265

90

400

ÉLÉVATION

CABINET

L'HARMONIE ENTRE L'EAU, LE BOIS ET LA LUMIERE

Lieu : Grasse, France

Contexte : Réaménagement d'un cabinet médical avec une attention portée à la circulation et à l'ambiance

Durée : Projet professionnel – 4 semaines

Ce projet de réaménagement d'un **cabinet médical** propose une nouvelle organisation des espaces pour répondre aux besoins des praticiens et des patients. Il intègre des **zones d'attente**, des **cabinets de consultation**, des **espaces techniques** et une circulation logique. Le choix des matériaux et des couleurs a été guidé par une volonté de créer un environnement **rassurant et fonctionnel**.



ESPACES RÉSERVÉS AUX MÉDECINS

CUISINE

WC

WC PMR


CABINET 3

SALLE D'ATTENTE

ENTRÉE

CABINET 1

CABINET 2

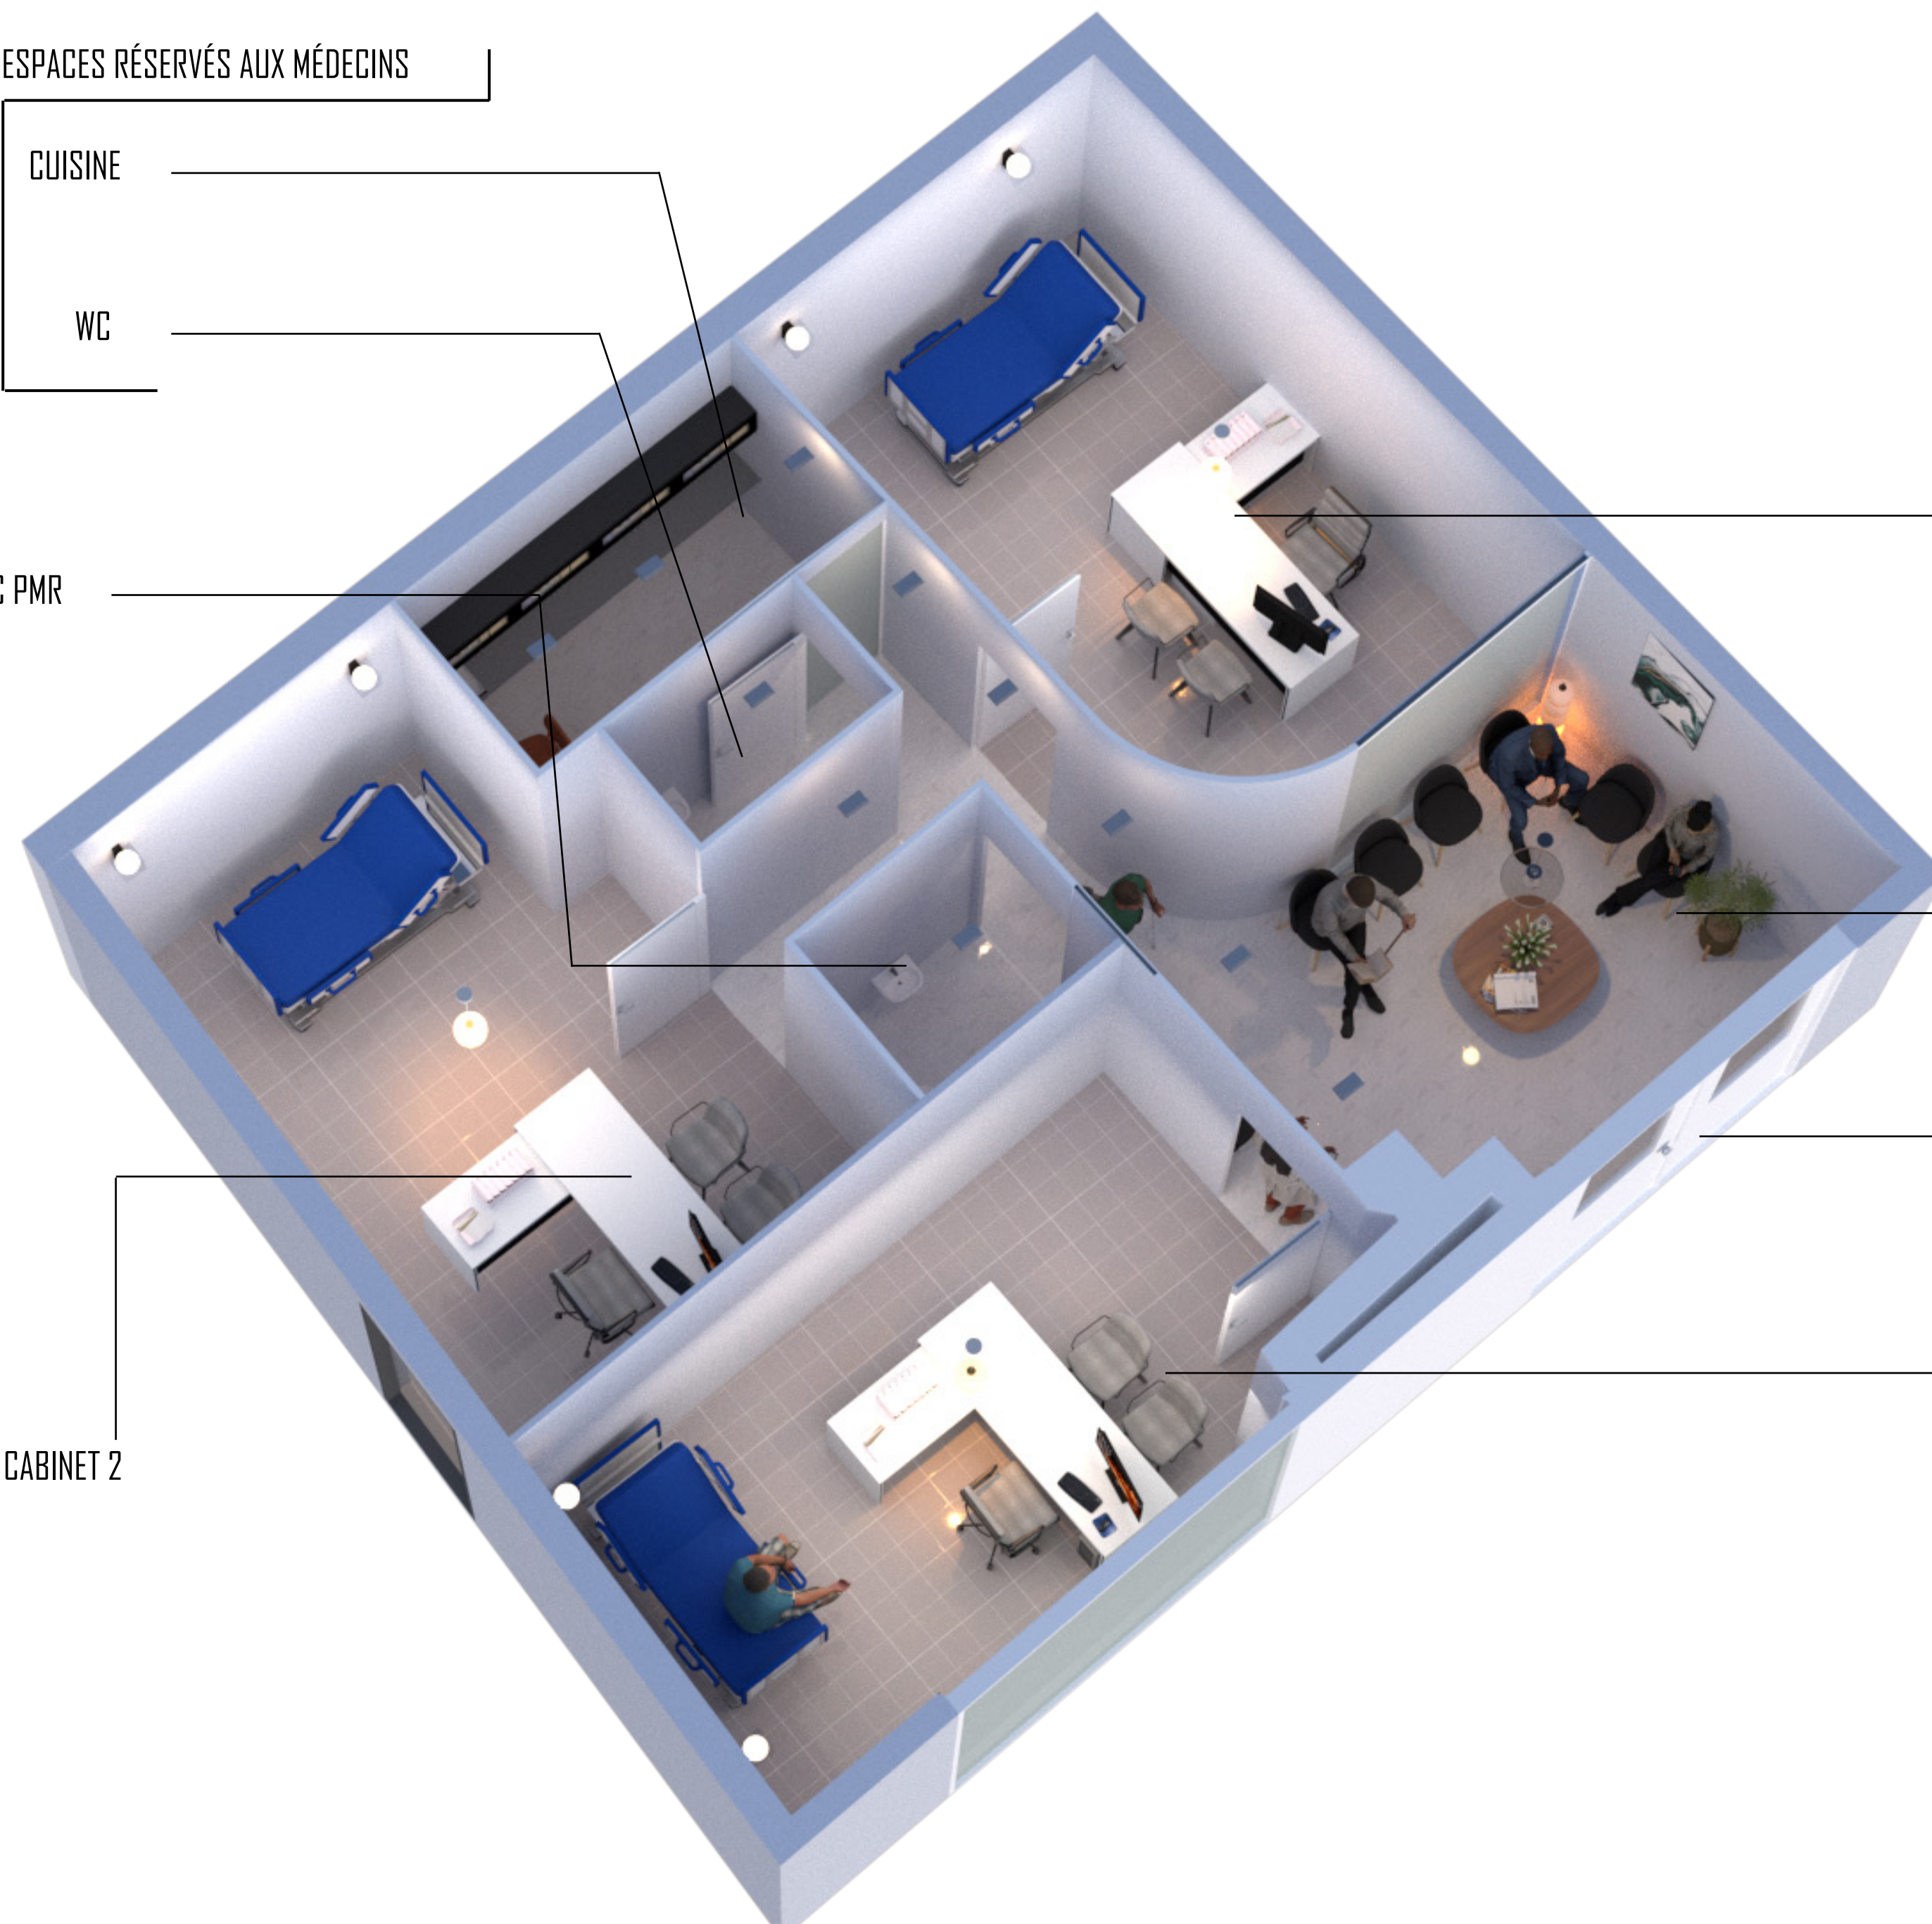

AT HOME

UNE NOUVELLE LECTURE DU QUOTIDIEN

Lieu : Pontault-Combault, France

Contexte : Réaménagement d'un salon existant pour optimiser l'aménagement et la lumière naturelle


Durée : Projet personnel – 1 semaine

Ce projet de **rénovation intérieure** concerne un salon existant, repensé pour optimiser la circulation, **améliorer le confort d'usage** et renforcer la cohérence esthétique de l'ensemble.

L'intervention se concentre sur la **reconfiguration du mobilier**, l'introduction de matériaux aux tonalités chaleureuses, et la mise en valeur de la lumière naturelle.

Un soin particulier a été apporté à l'équilibre entre les **pleins et les vides**, les axes de vue et les zones fonctionnelles, afin de créer un espace à la fois **fluide**, lisible et propice au quotidien.



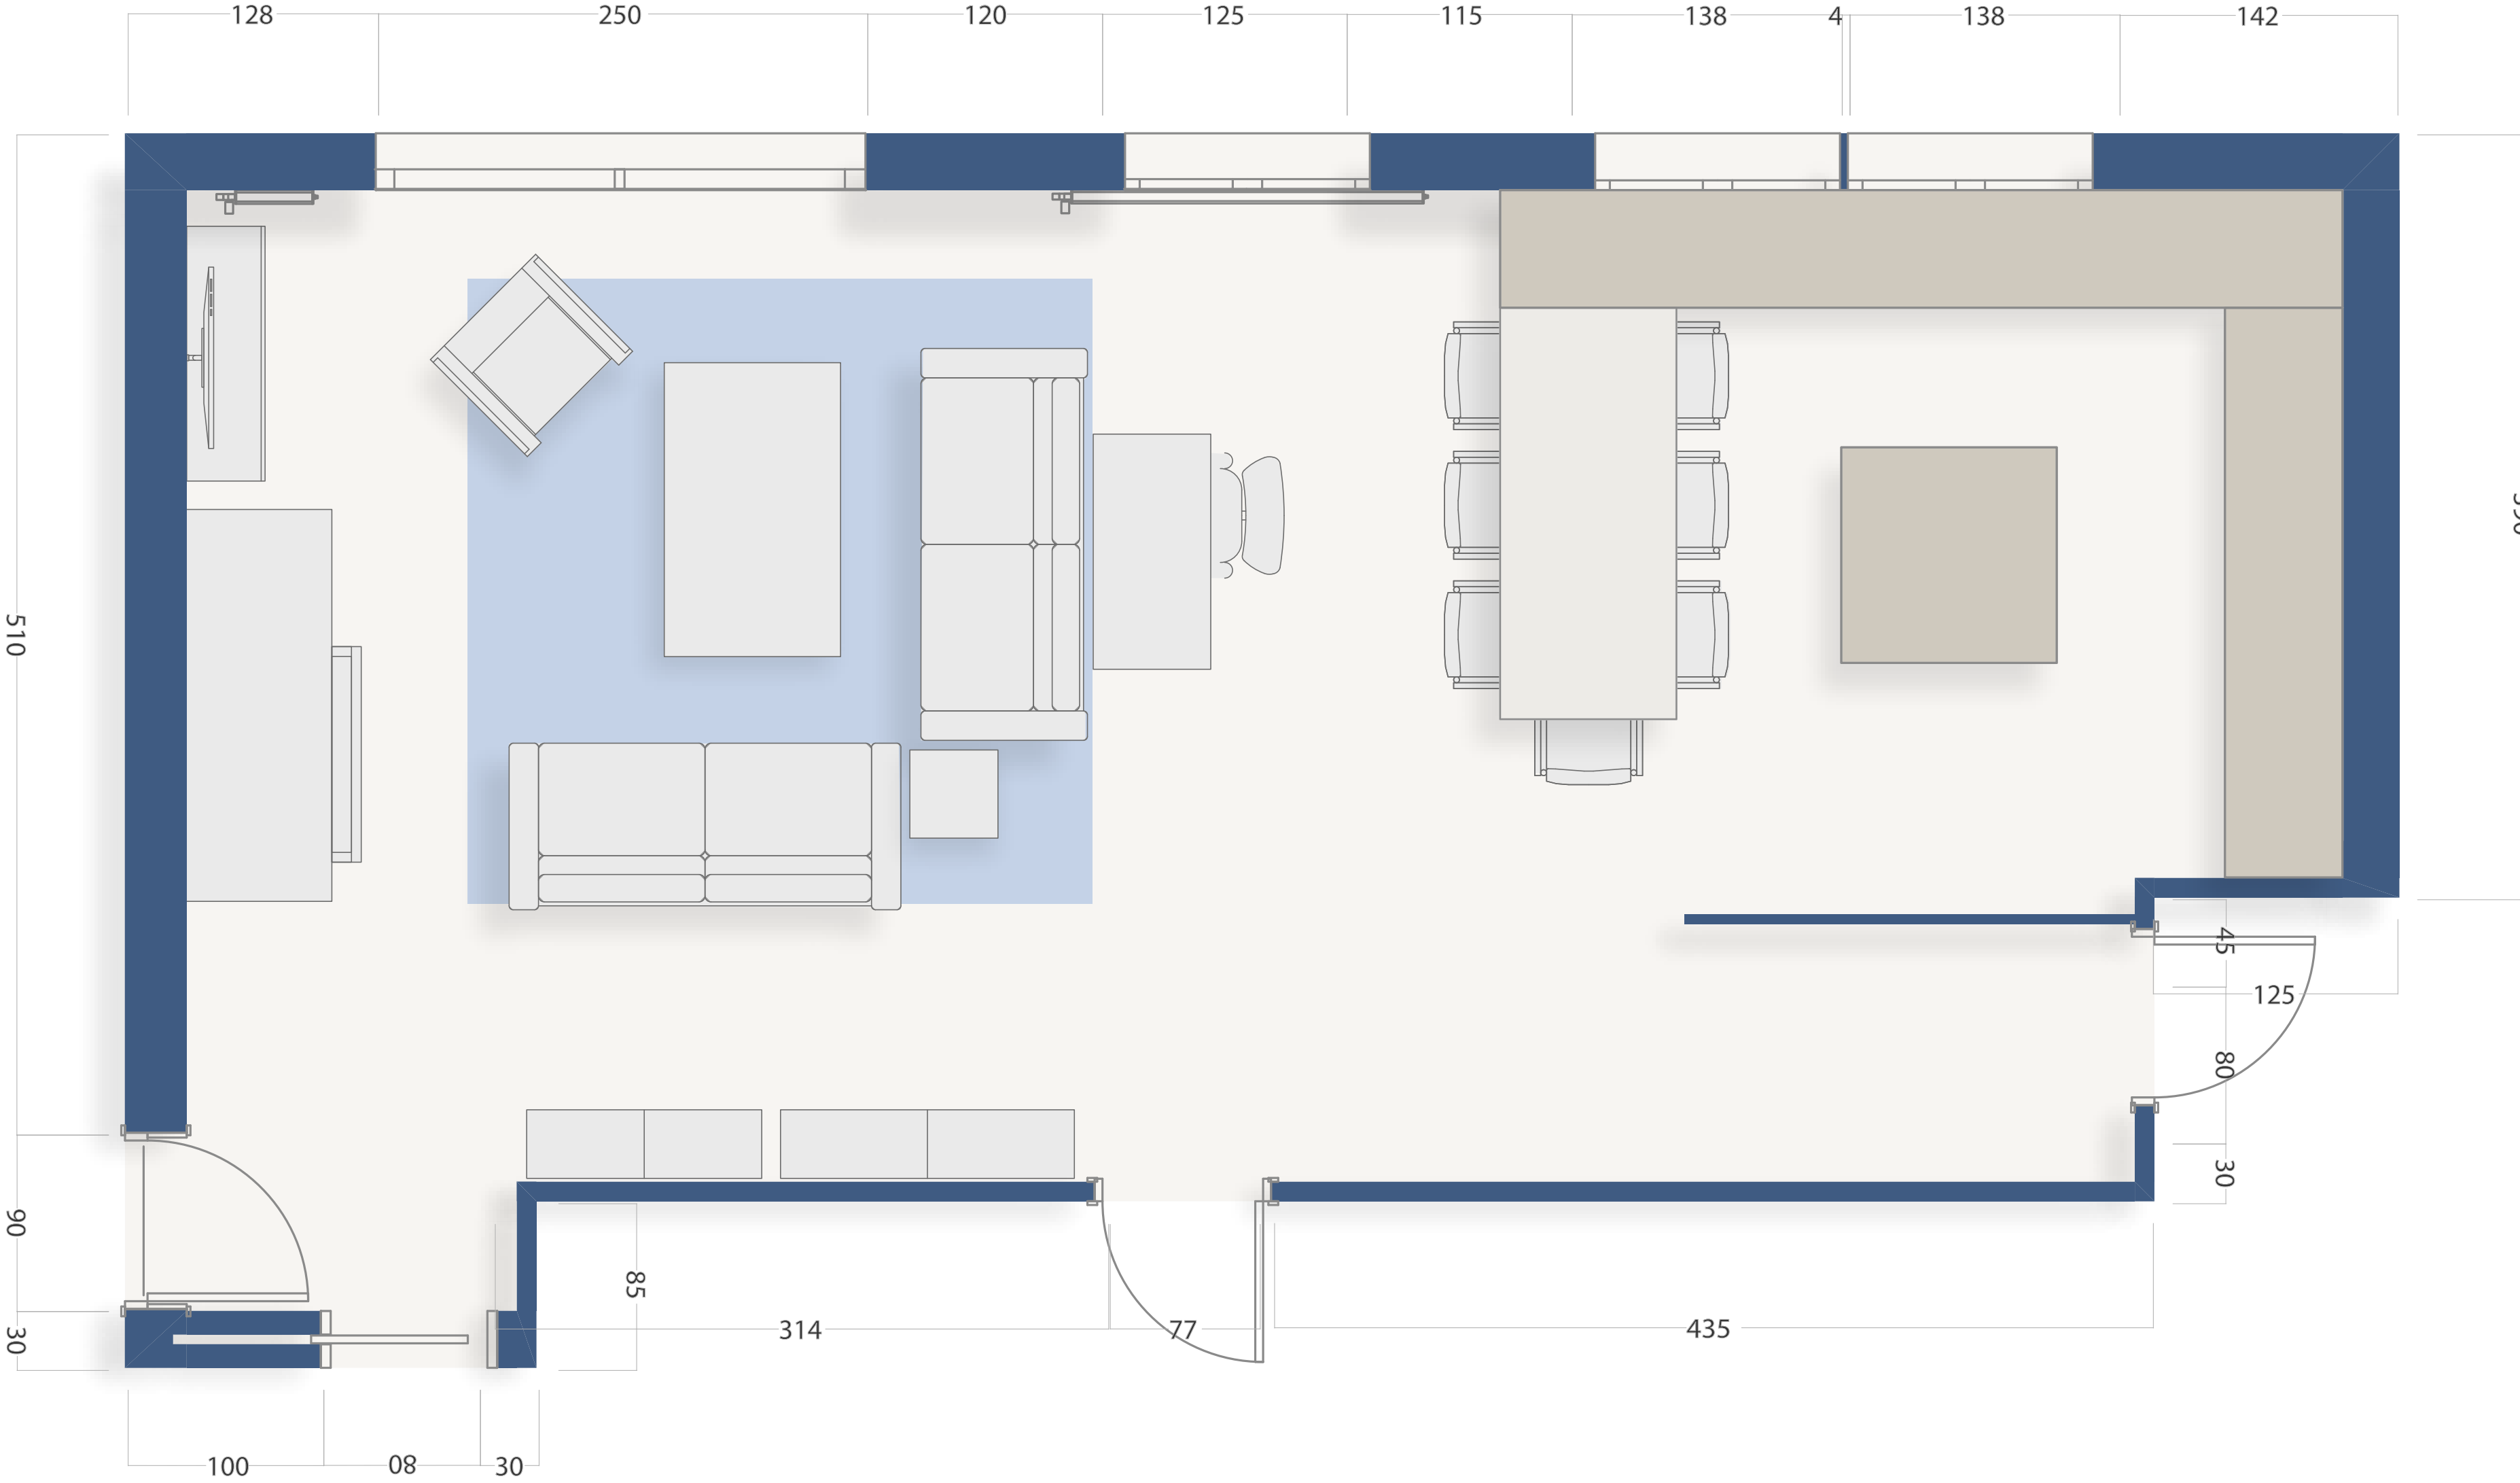

MERCI

07 81 37 22 90

maevatheolade2013@gmail.com