


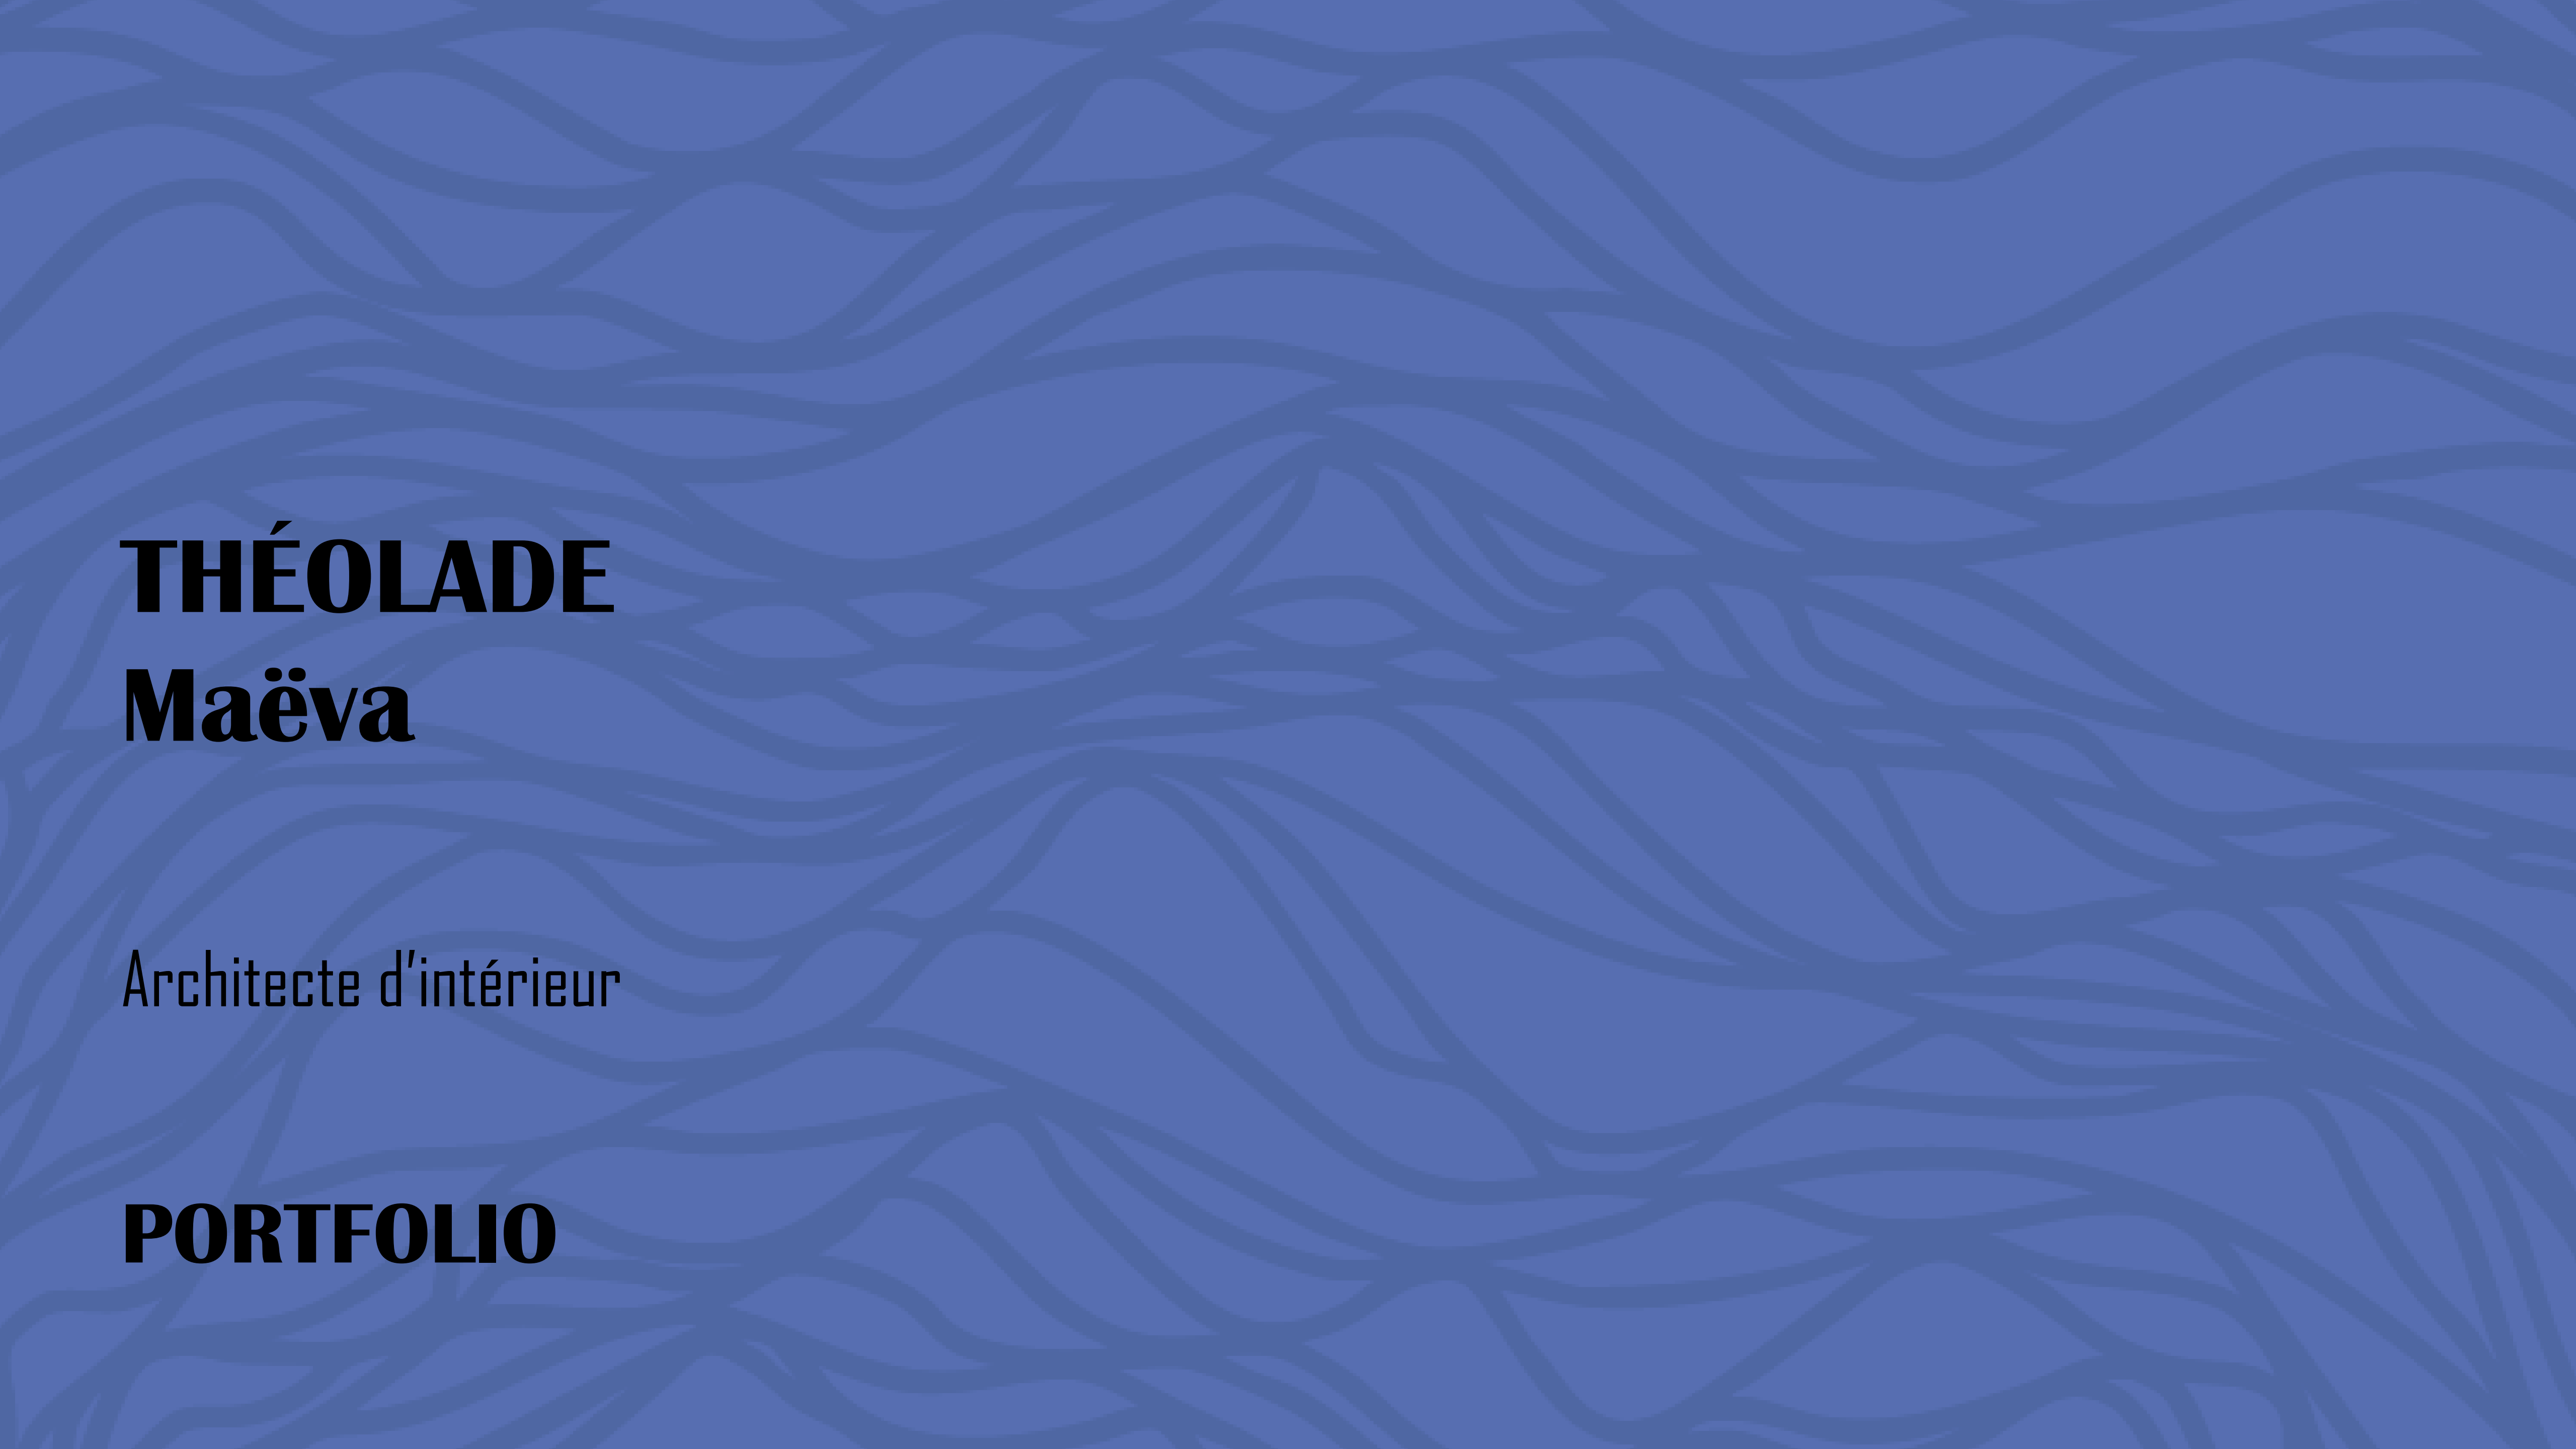

THÉOLADE

Maëva

Architecte d'intérieur

PORTFOLIO

Architecte d'intérieur récemment diplômée, je développe des projets mêlant fonctionnalité, identité visuelle et attention portée aux usages.

À travers ce portfolio, je présente une sélection de projets académiques, professionnels et personnels, allant de l'aménagement intérieur à la scénographie et à la conception d'espaces immersifs. Plans, modélisations, rendus et recherches de matériaux traduisent les différentes étapes de ma démarche de conception.

La lumière naturelle occupe une place importante dans mon travail. J'aime concevoir des éléments ajourés, proches du principe du moucharabieh, afin de filtrer la lumière et de faire évoluer les ombres, les matières et la perception de l'espace au fil de la journée.

SOMMAIRE

LE CERCLE DU SON

FLUENCE

WAVEWOOD

L'ATTENTE, REPENSÉE

LUMIÈRE MATINALE

SOAPBOTTLE

CABINET

LE CERCLE DU SON

UNE EXPÉRIENCE IMMERSIVE AUTOUR DE L'ÉCOUTE MUSICALE

Lieu : Parc de la Villette, Paris, France (projet fictif)

Contexte : Création d'un lieu dédié à l'écoute musicale immersive, individuelle et collective

Durée : Projet de fin d'études – Mastère 2025-2026

Le Cercle du Son explore la manière dont l'architecture peut transformer **l'écoute musicale** en expérience **spatiale** et **collective**. Implanté au Parc de la Villette, le projet propose un parcours entre partage et intimité, articulé autour d'un espace **d'écoute collective** et de **capsules individuelles**. Formes enveloppantes, dispositifs acoustiques, lumière et matérialité composent un environnement **immersif** où l'espace s'efface progressivement au **profit du son**.



PARC DE LA VILLETTE - LE SITE


Le projet s'implante au cœur du Parc de la Villette, dans le 19^e arrondissement de Paris, au sein de la Folie N6.

PLAN DE SITUATION



0 25 50 75 100m

PLAN MASSE

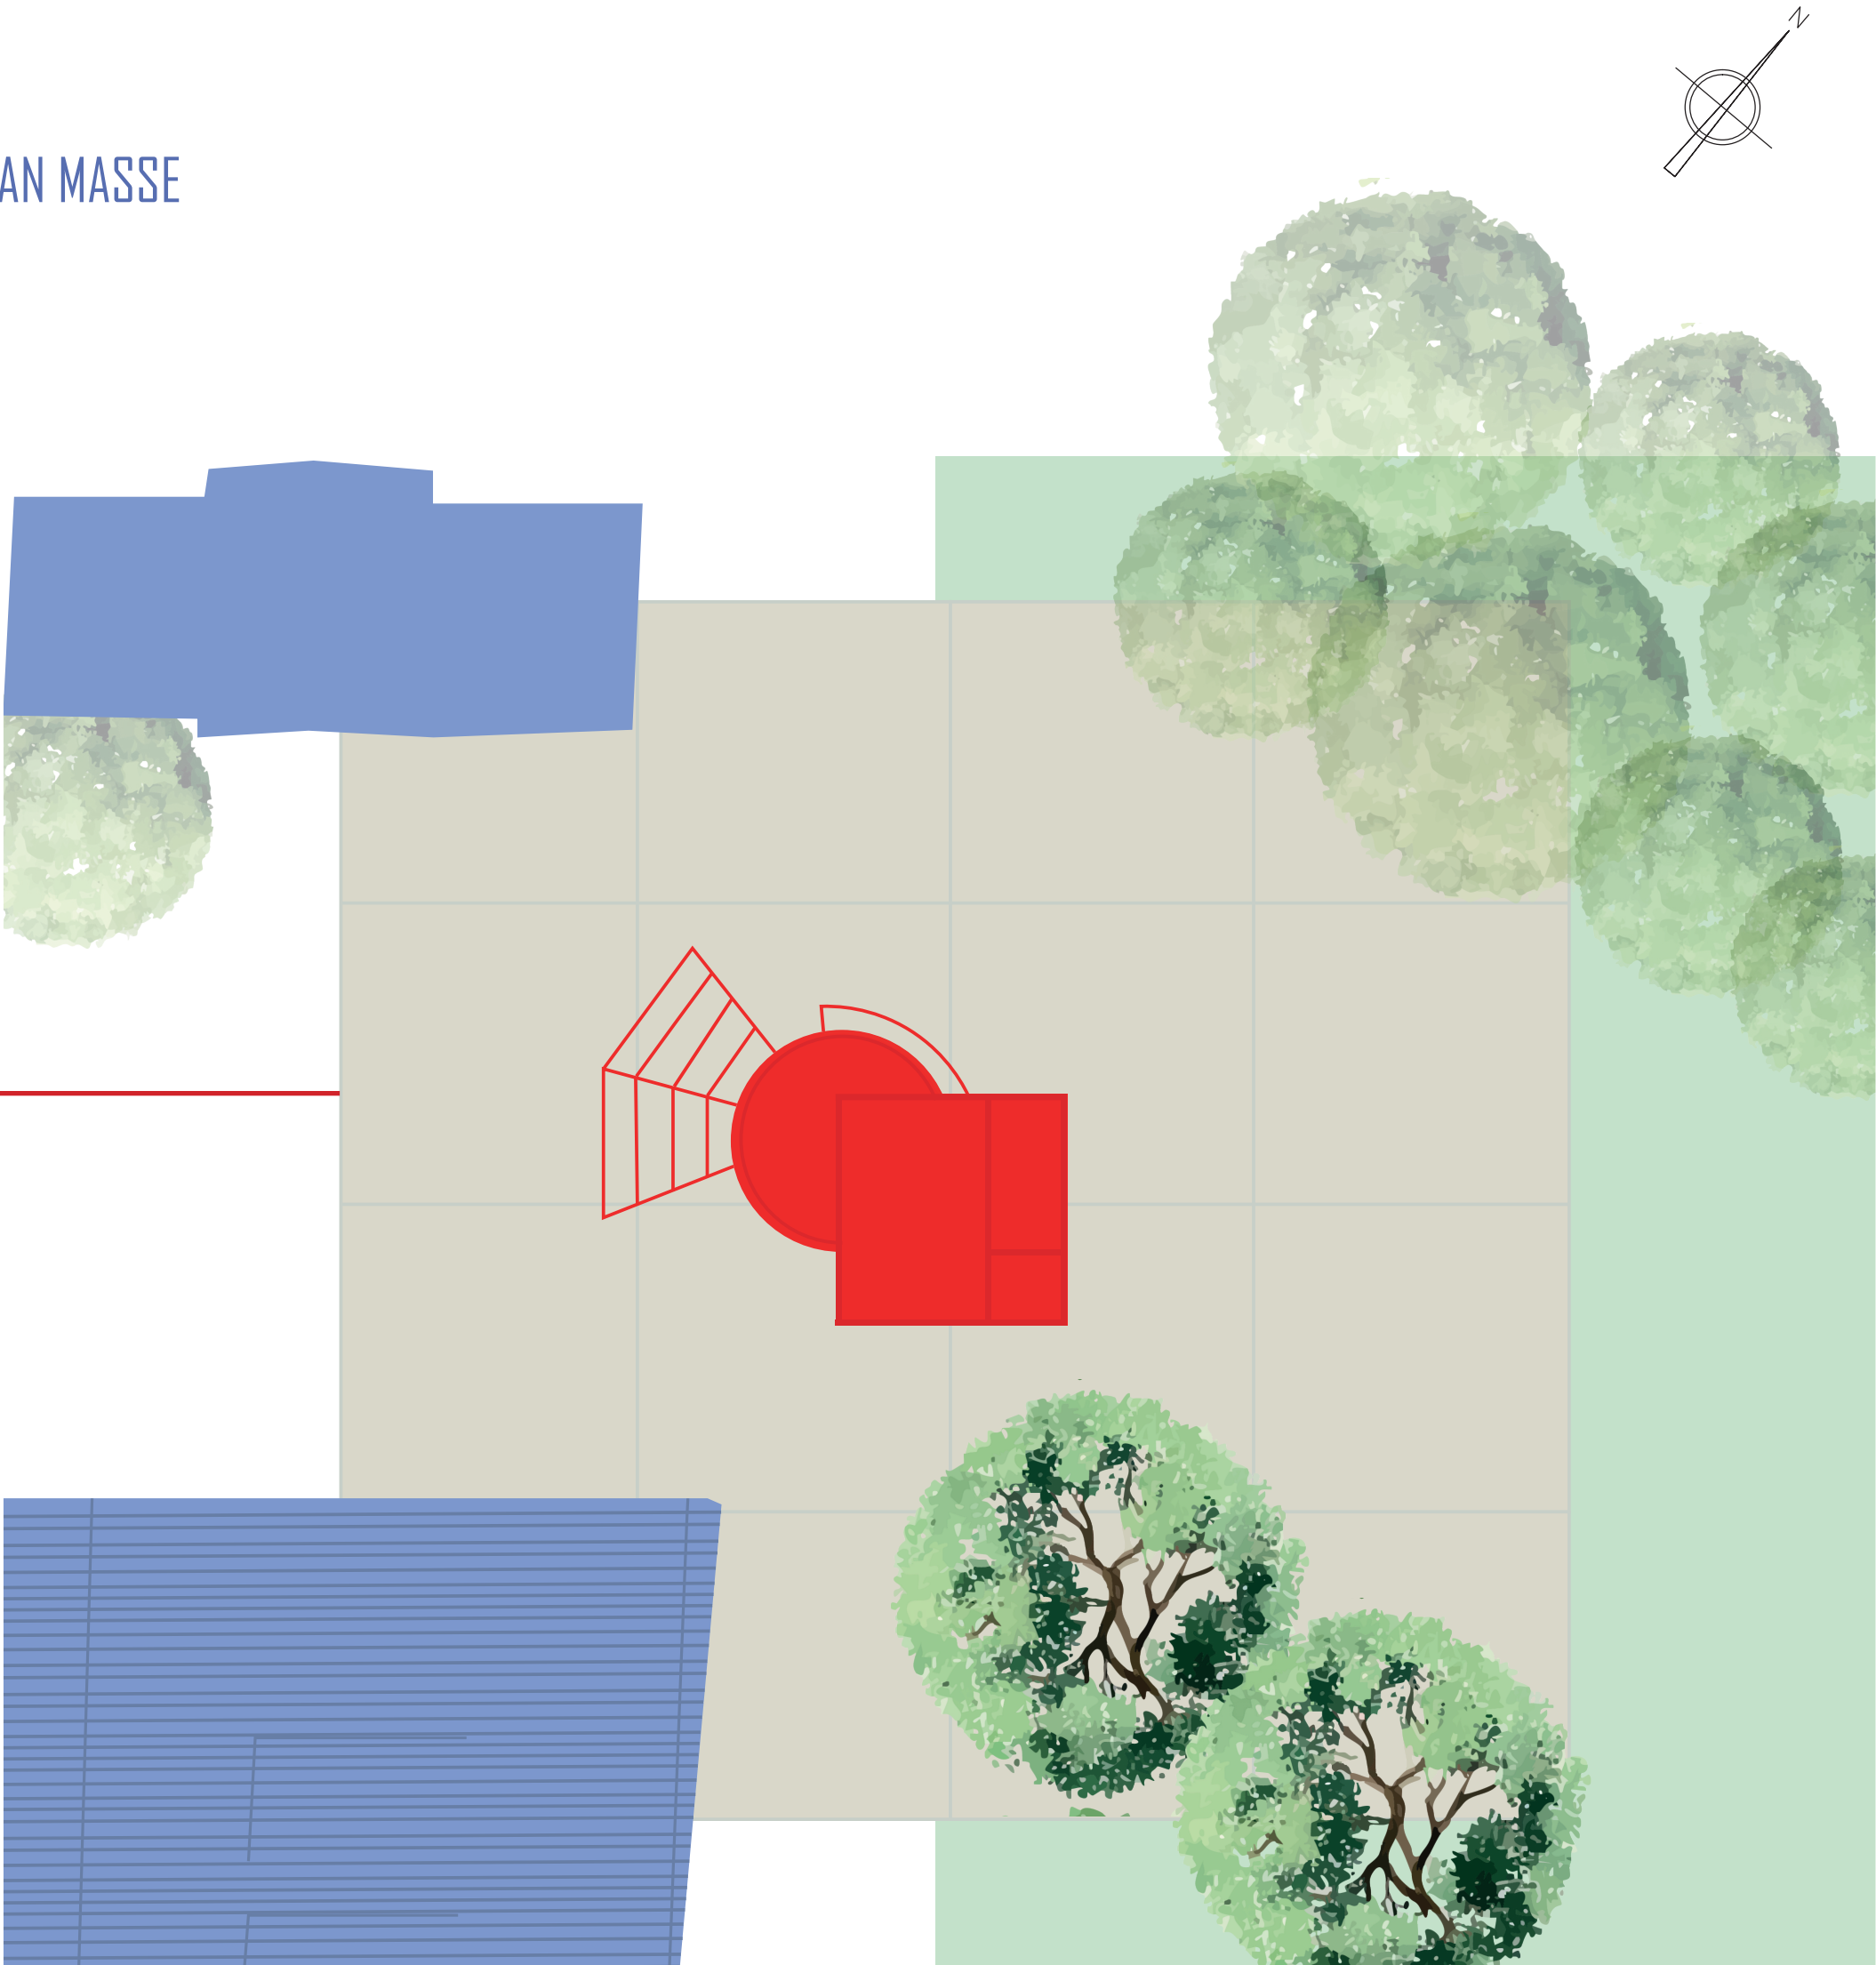


PARIS 19^e — PARC DE LA VILLETTE — FOLIE N6 / 276 m²


1/250

PLANS GÉNÉRAUX


PLAN RDC

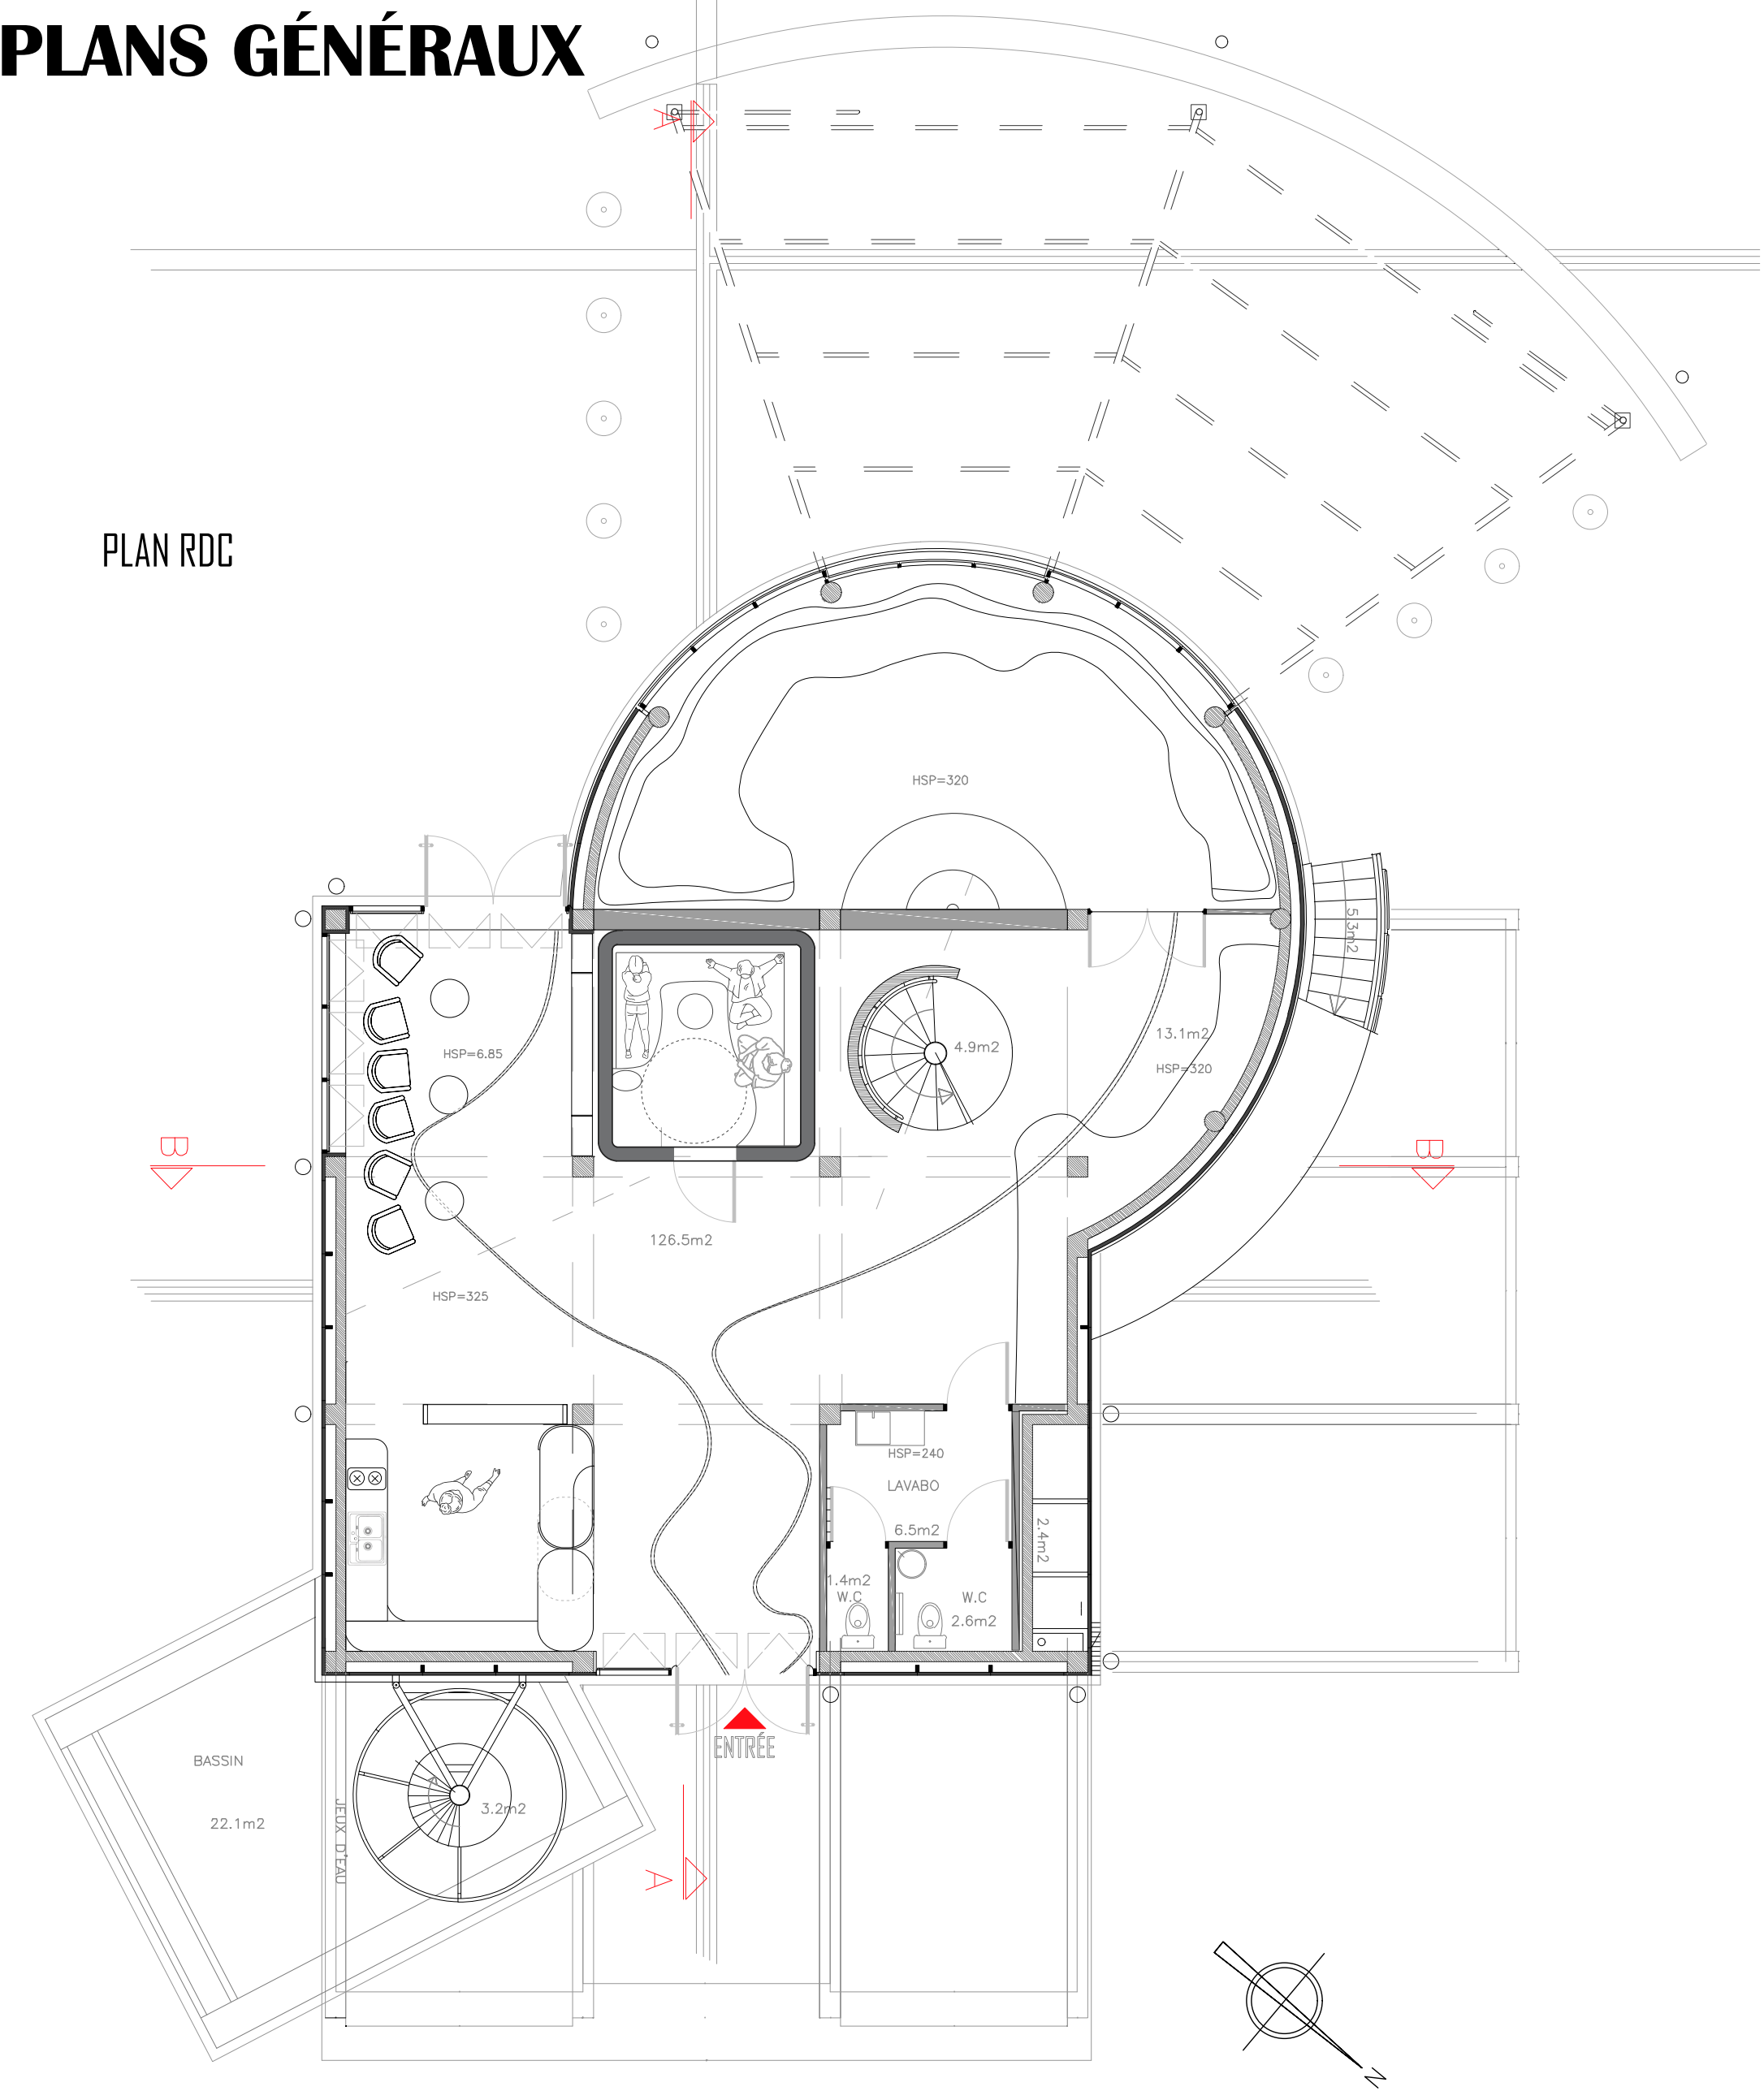

PLAN R+1

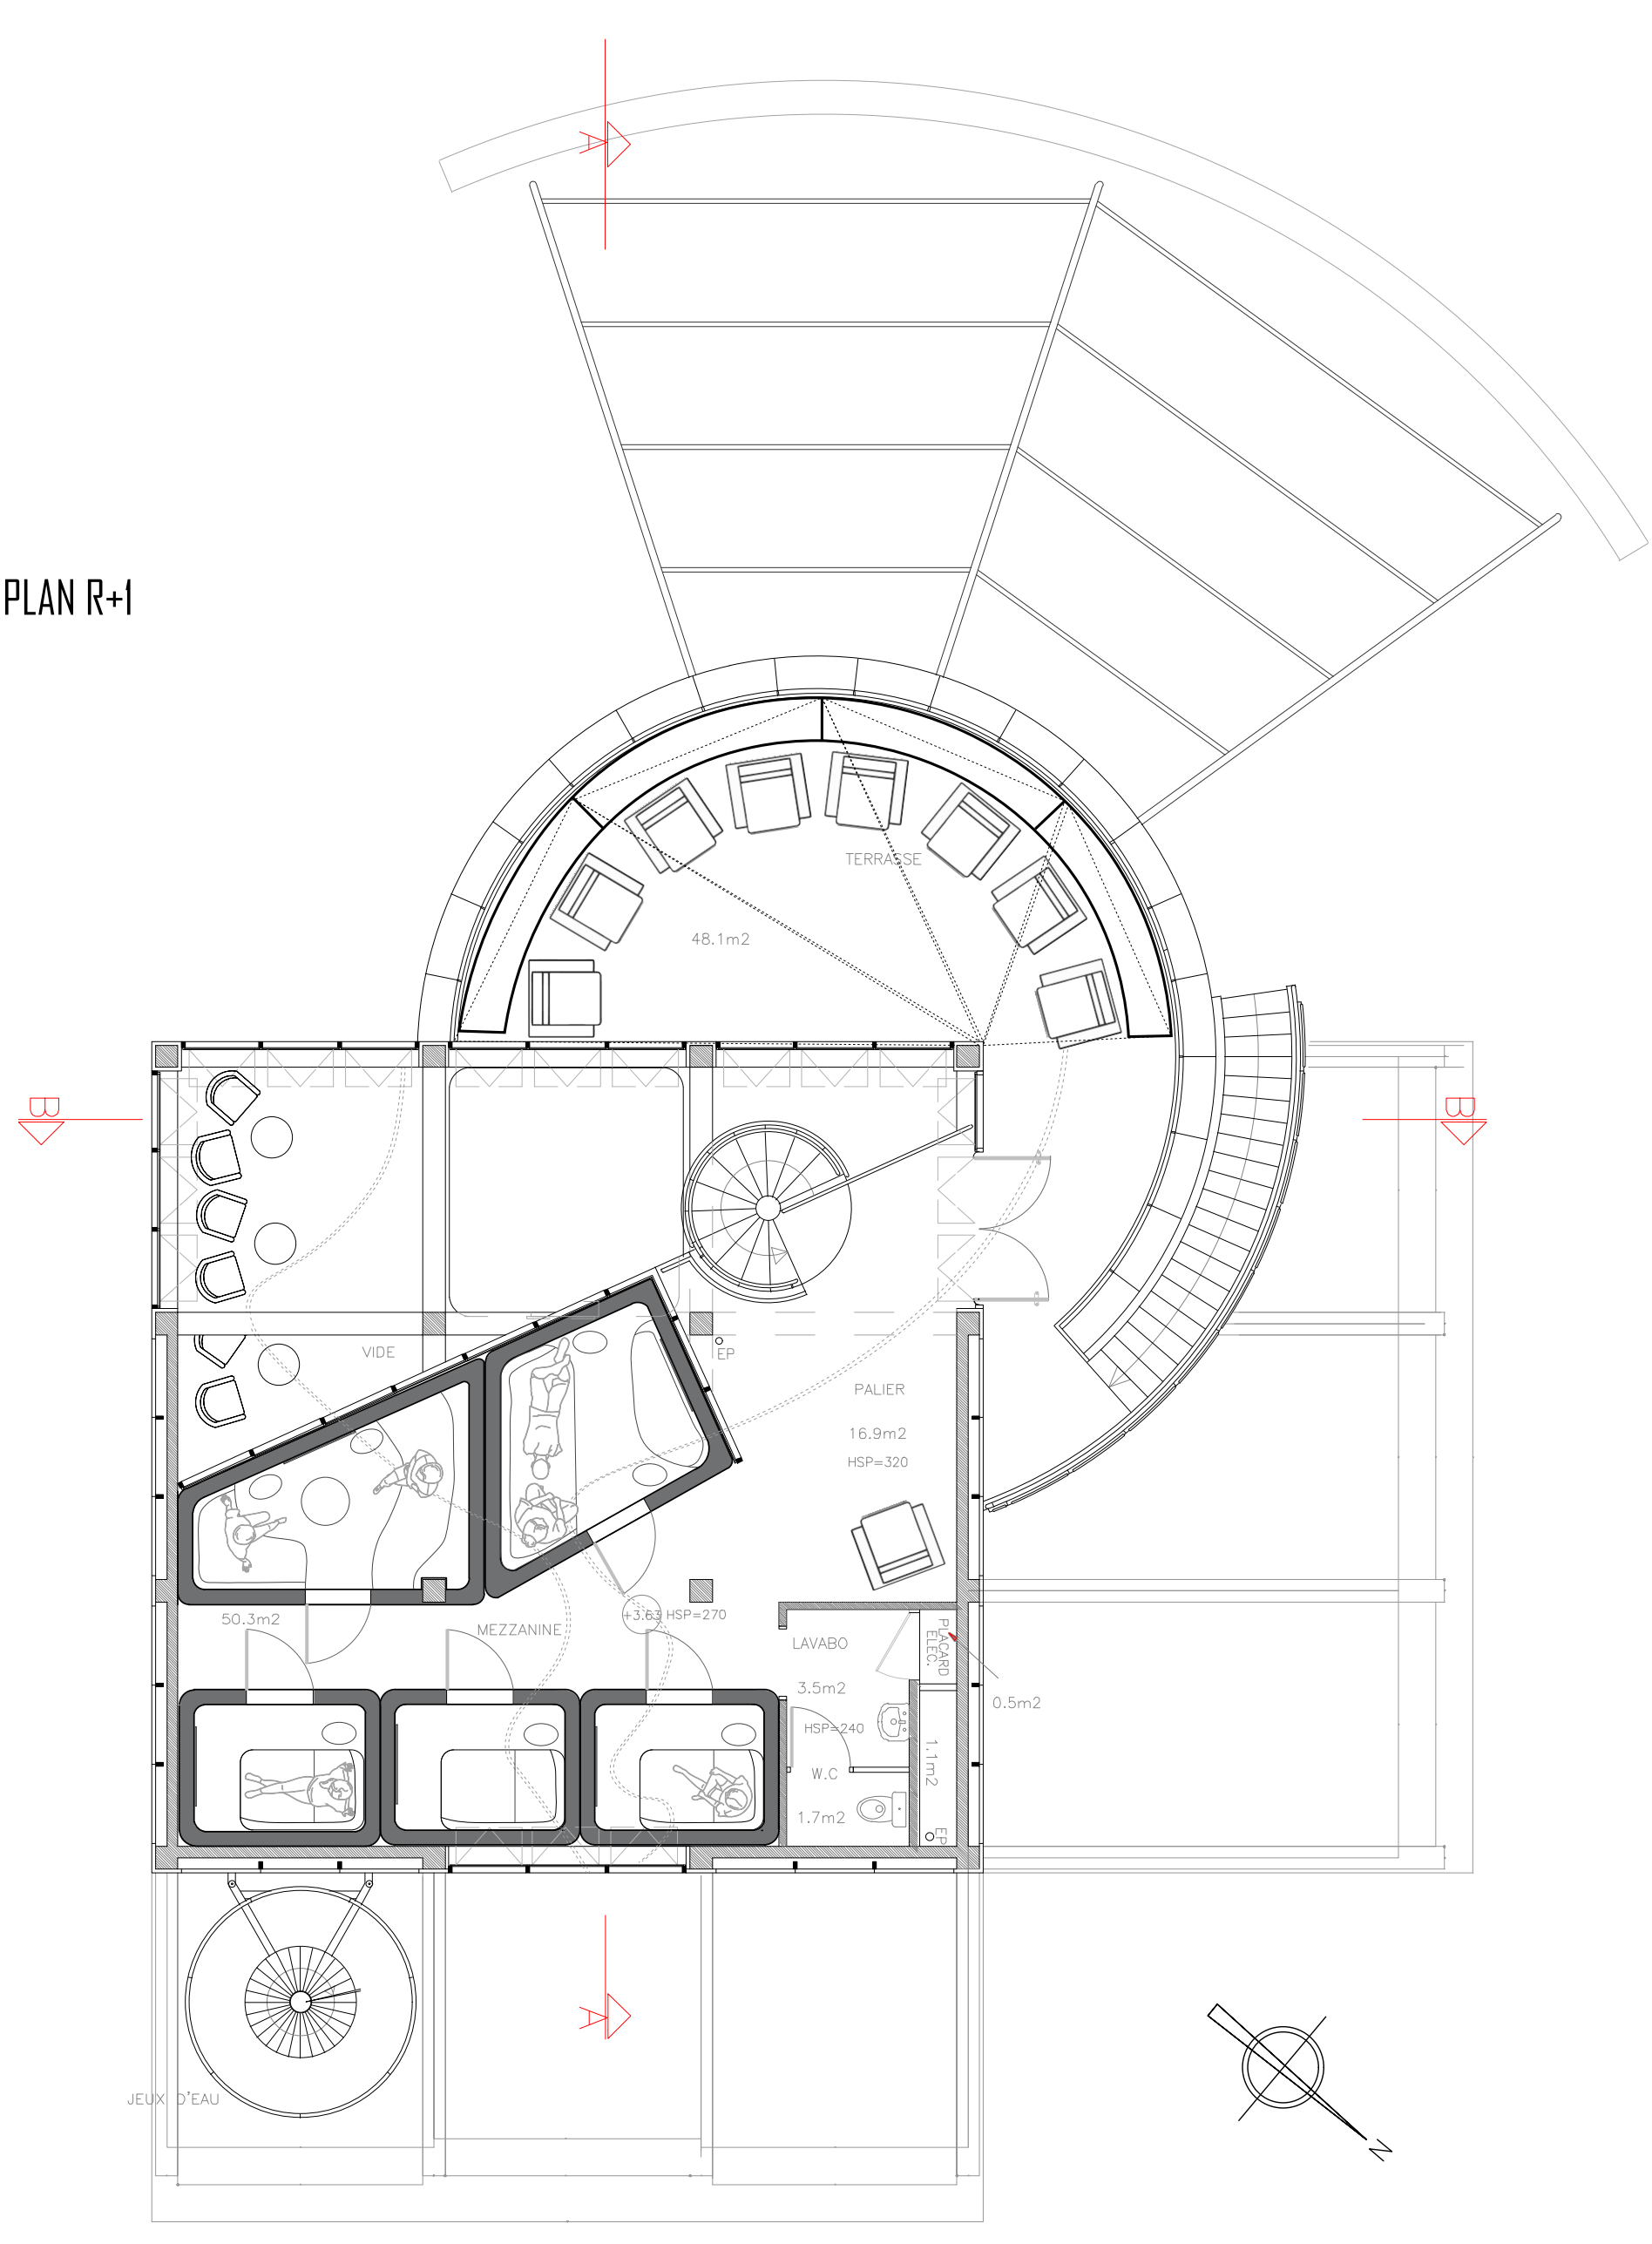


COUPE GÉNÉRALE

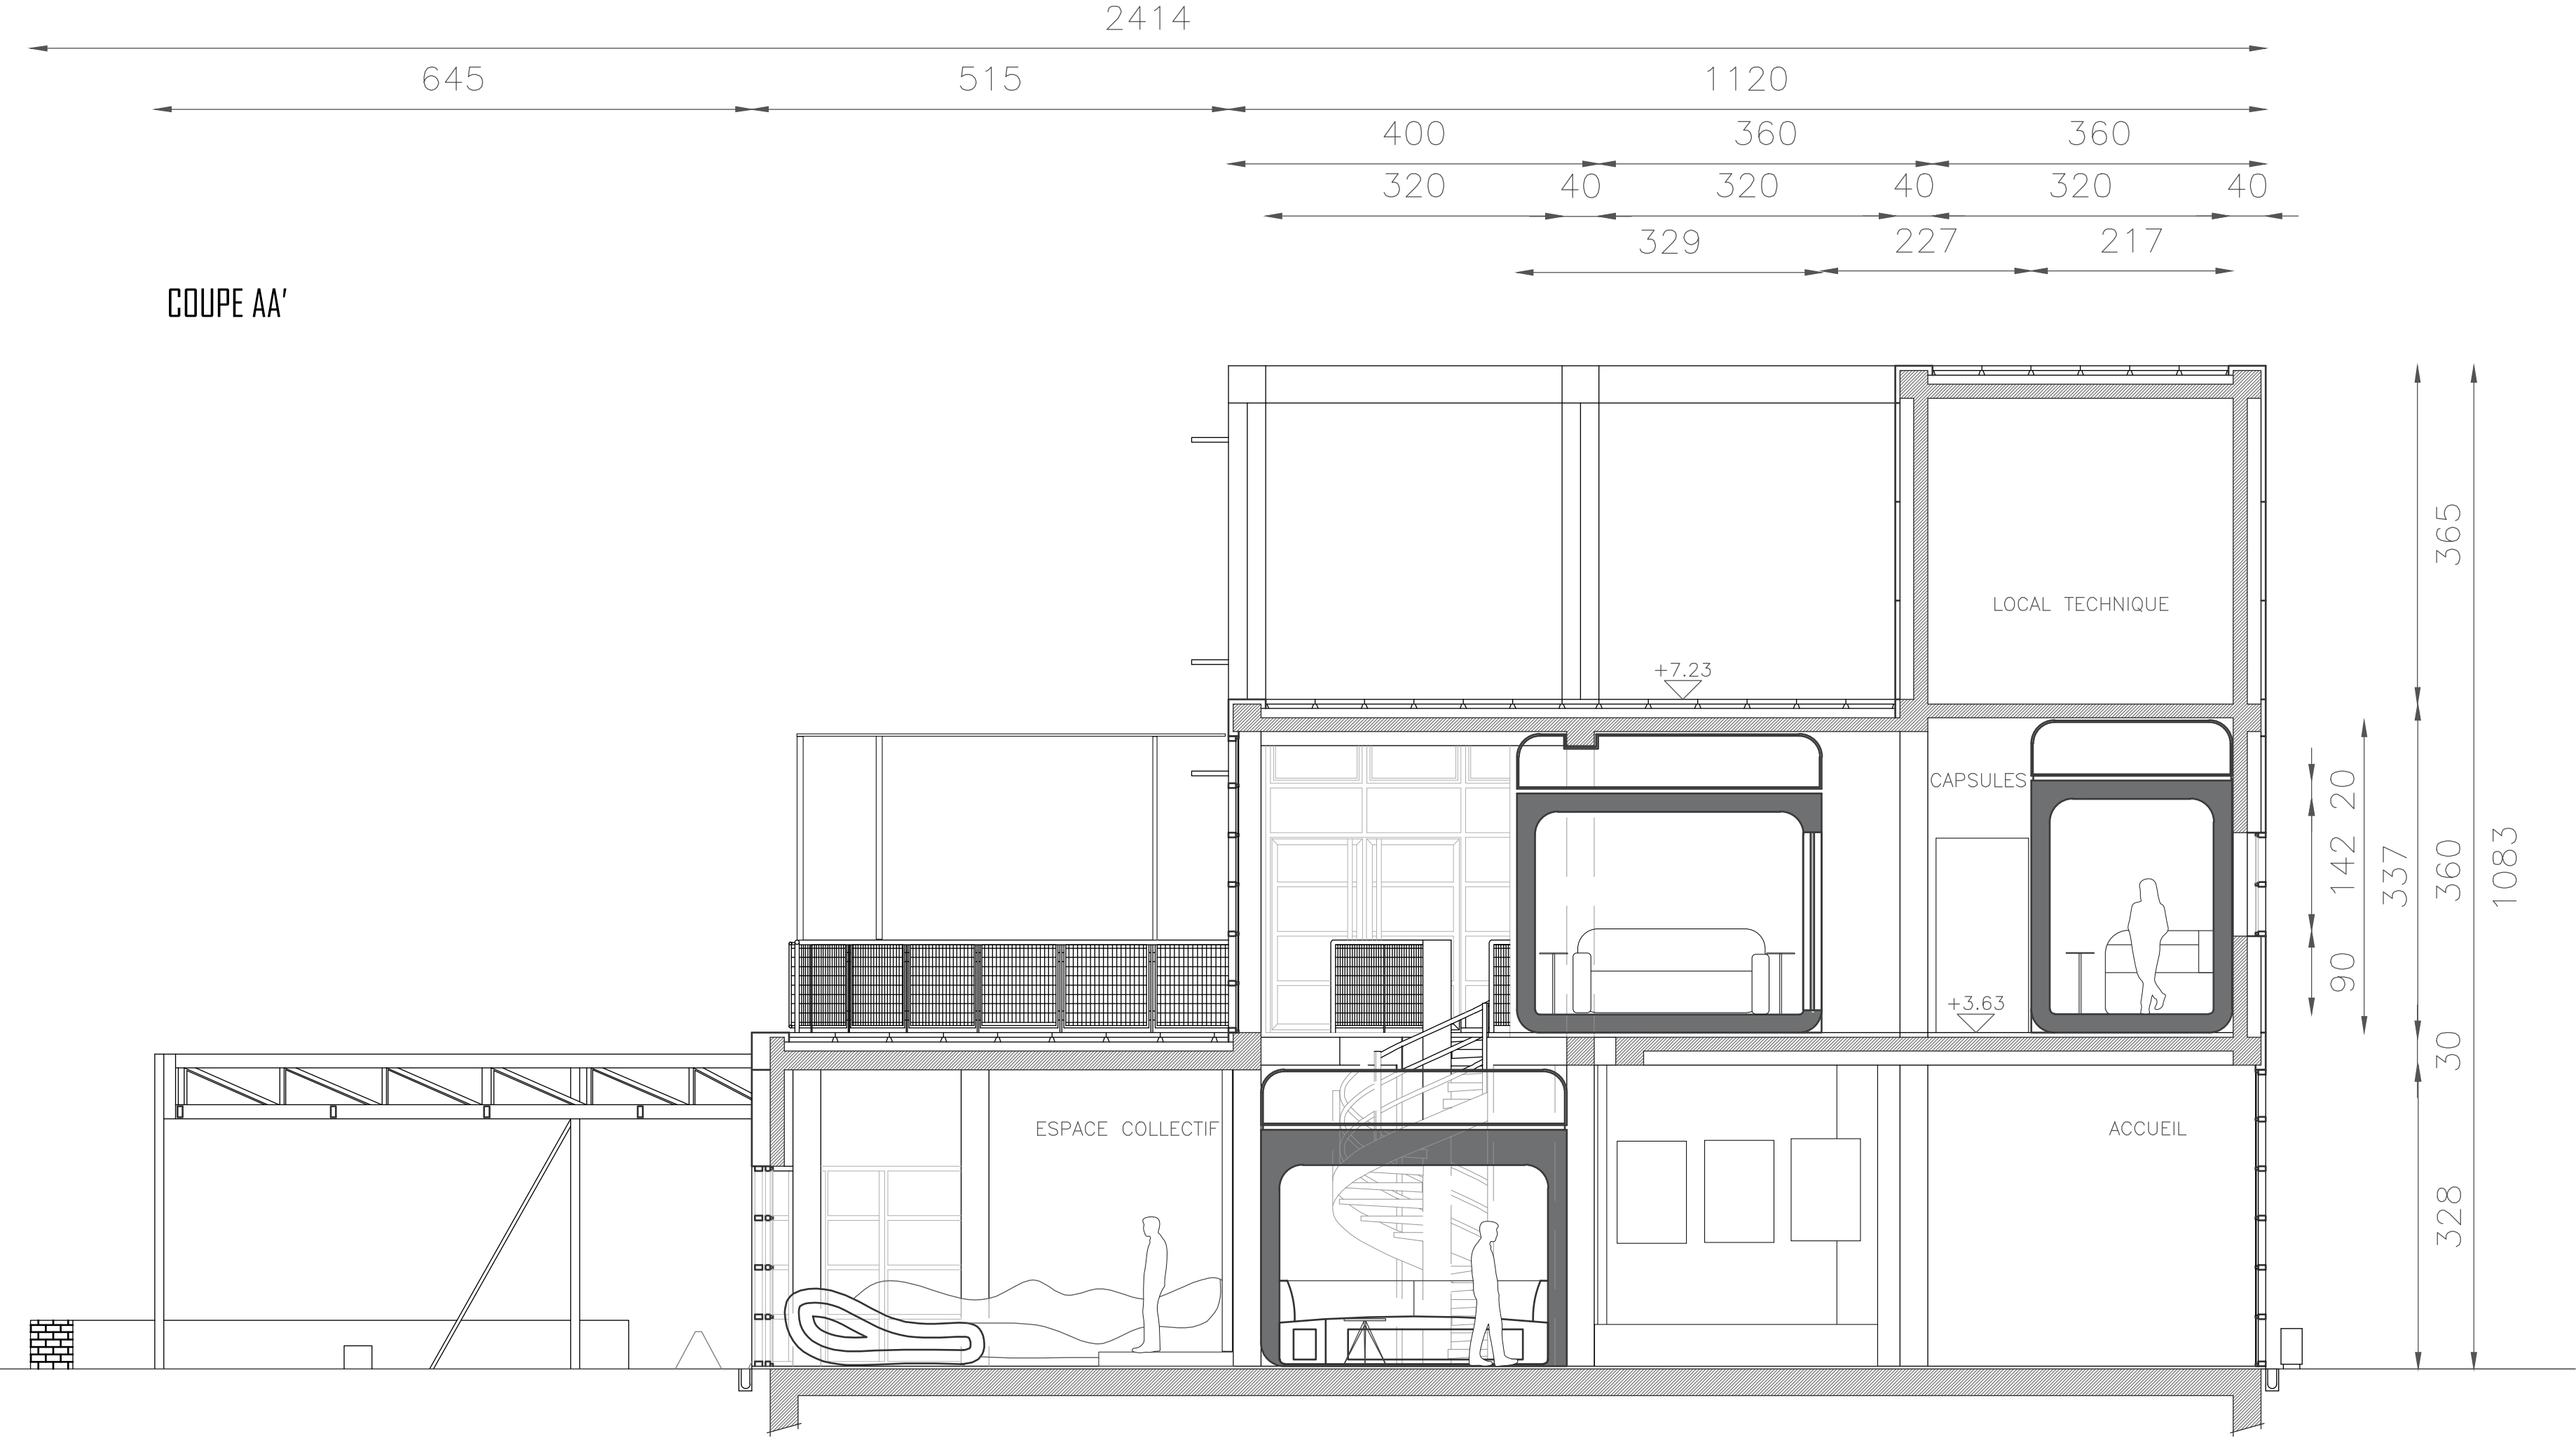


CONSTRUCTION DES CAPSULES

COUPE & PLAN - CAPSULE 01


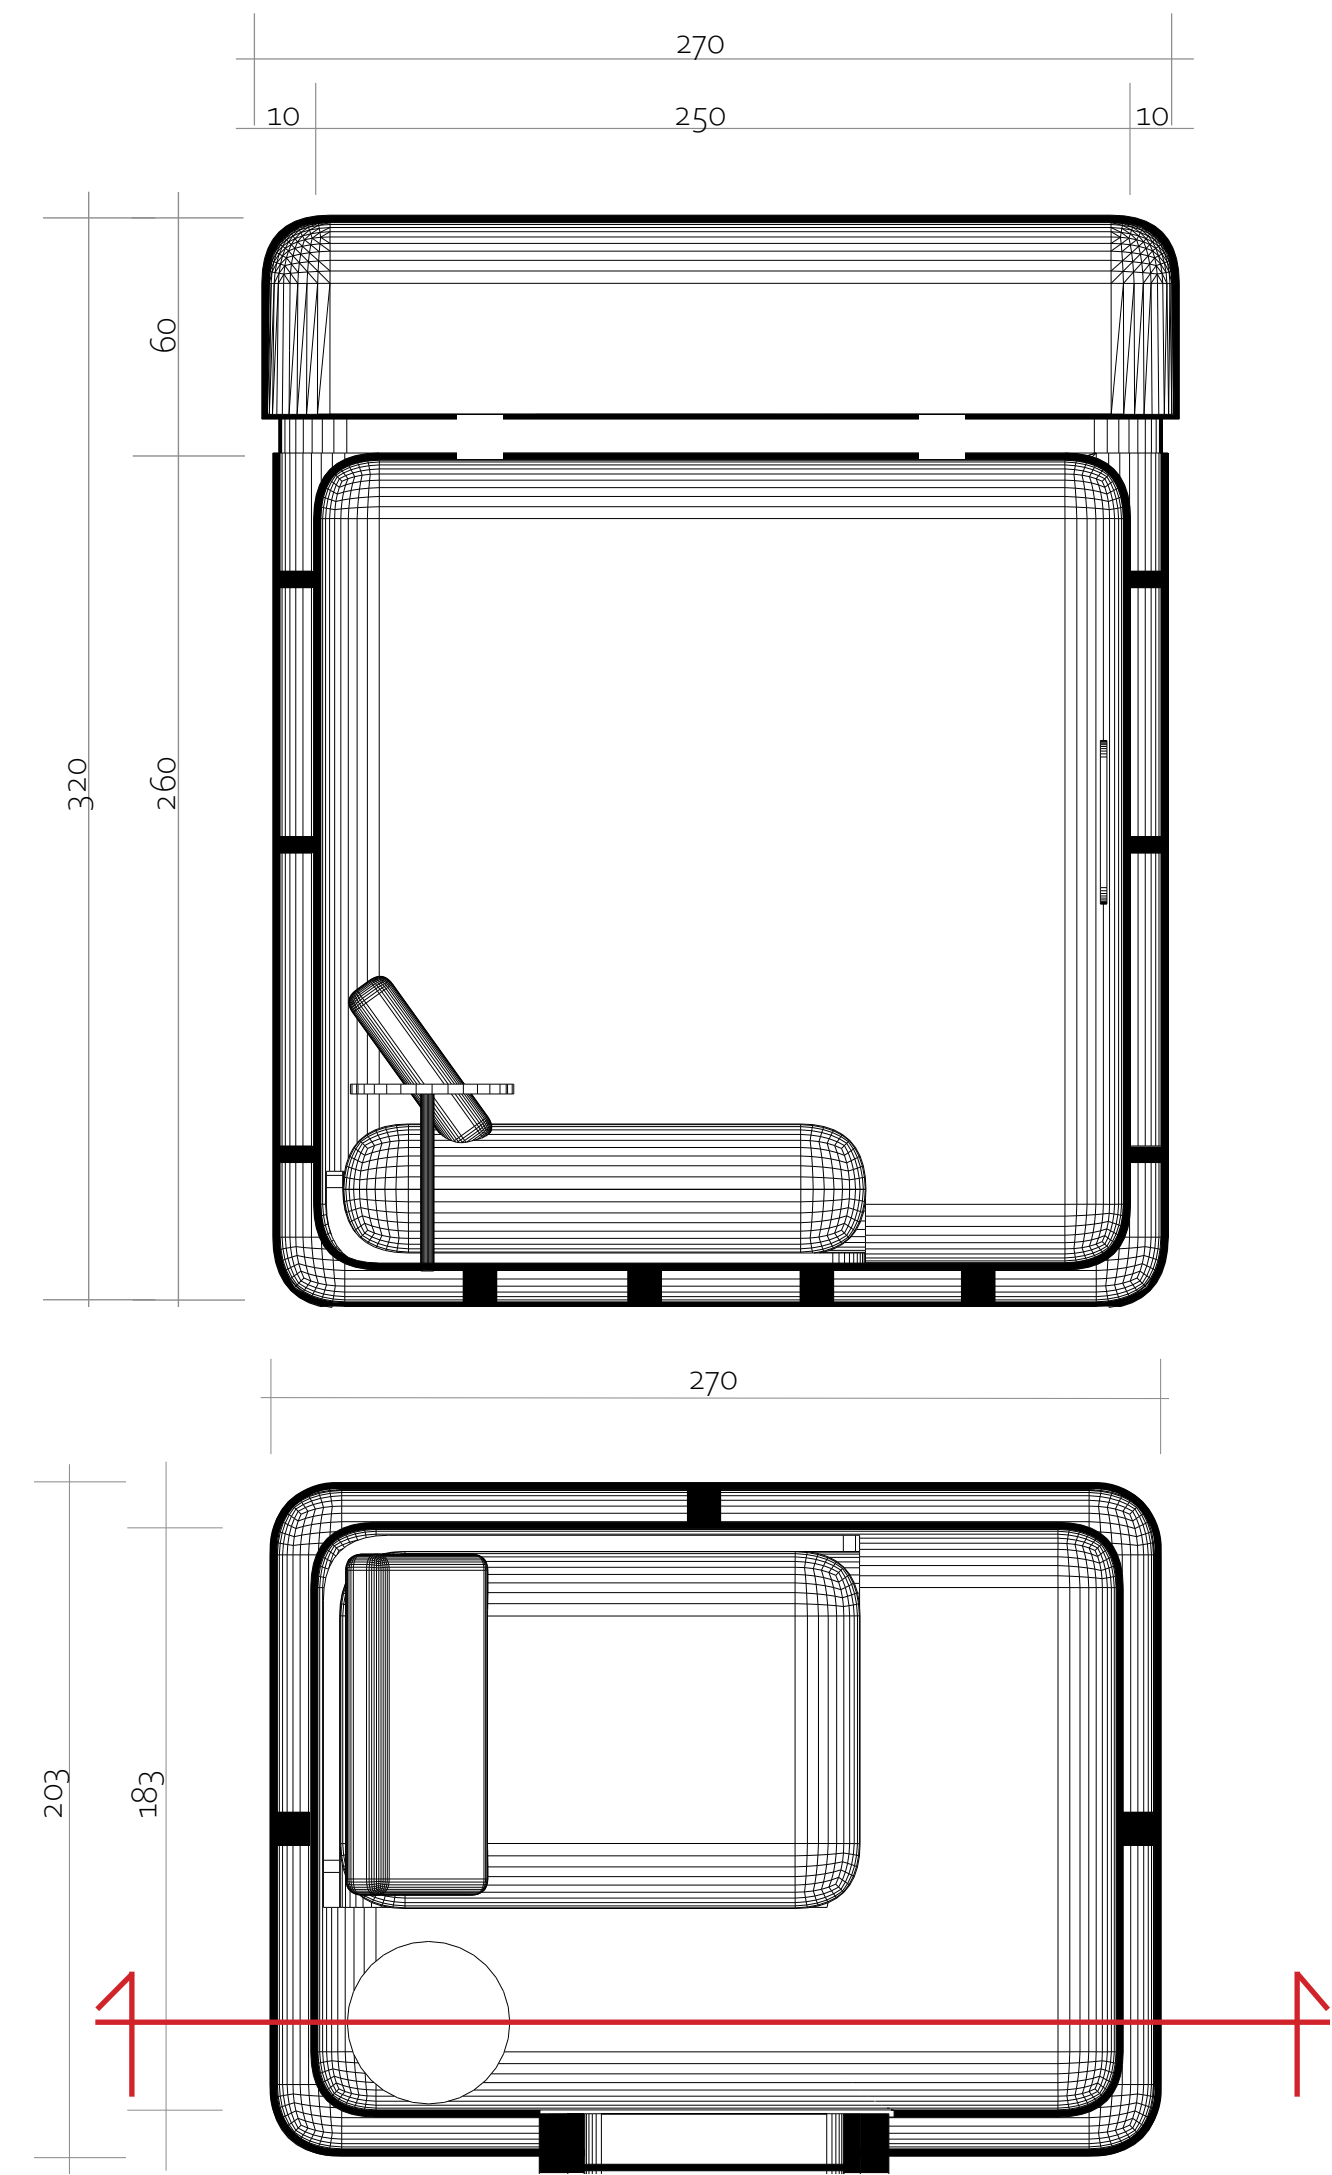


AXONOMETRIE ÉCLATÉE - CAPSULE 01

- 01 - TOITURE / COQUE SUPÉRIEURE
- 02 - MOBILIER (ÉCRAN / ASSISE / TABLE)
- 03 - COQUE INTÉRIEURE
- 04 - COQUE EXTÉRIEURE
- 05 - DORMANT DE PORTE
- 06 - VITRE
- 06 - VANTAIL

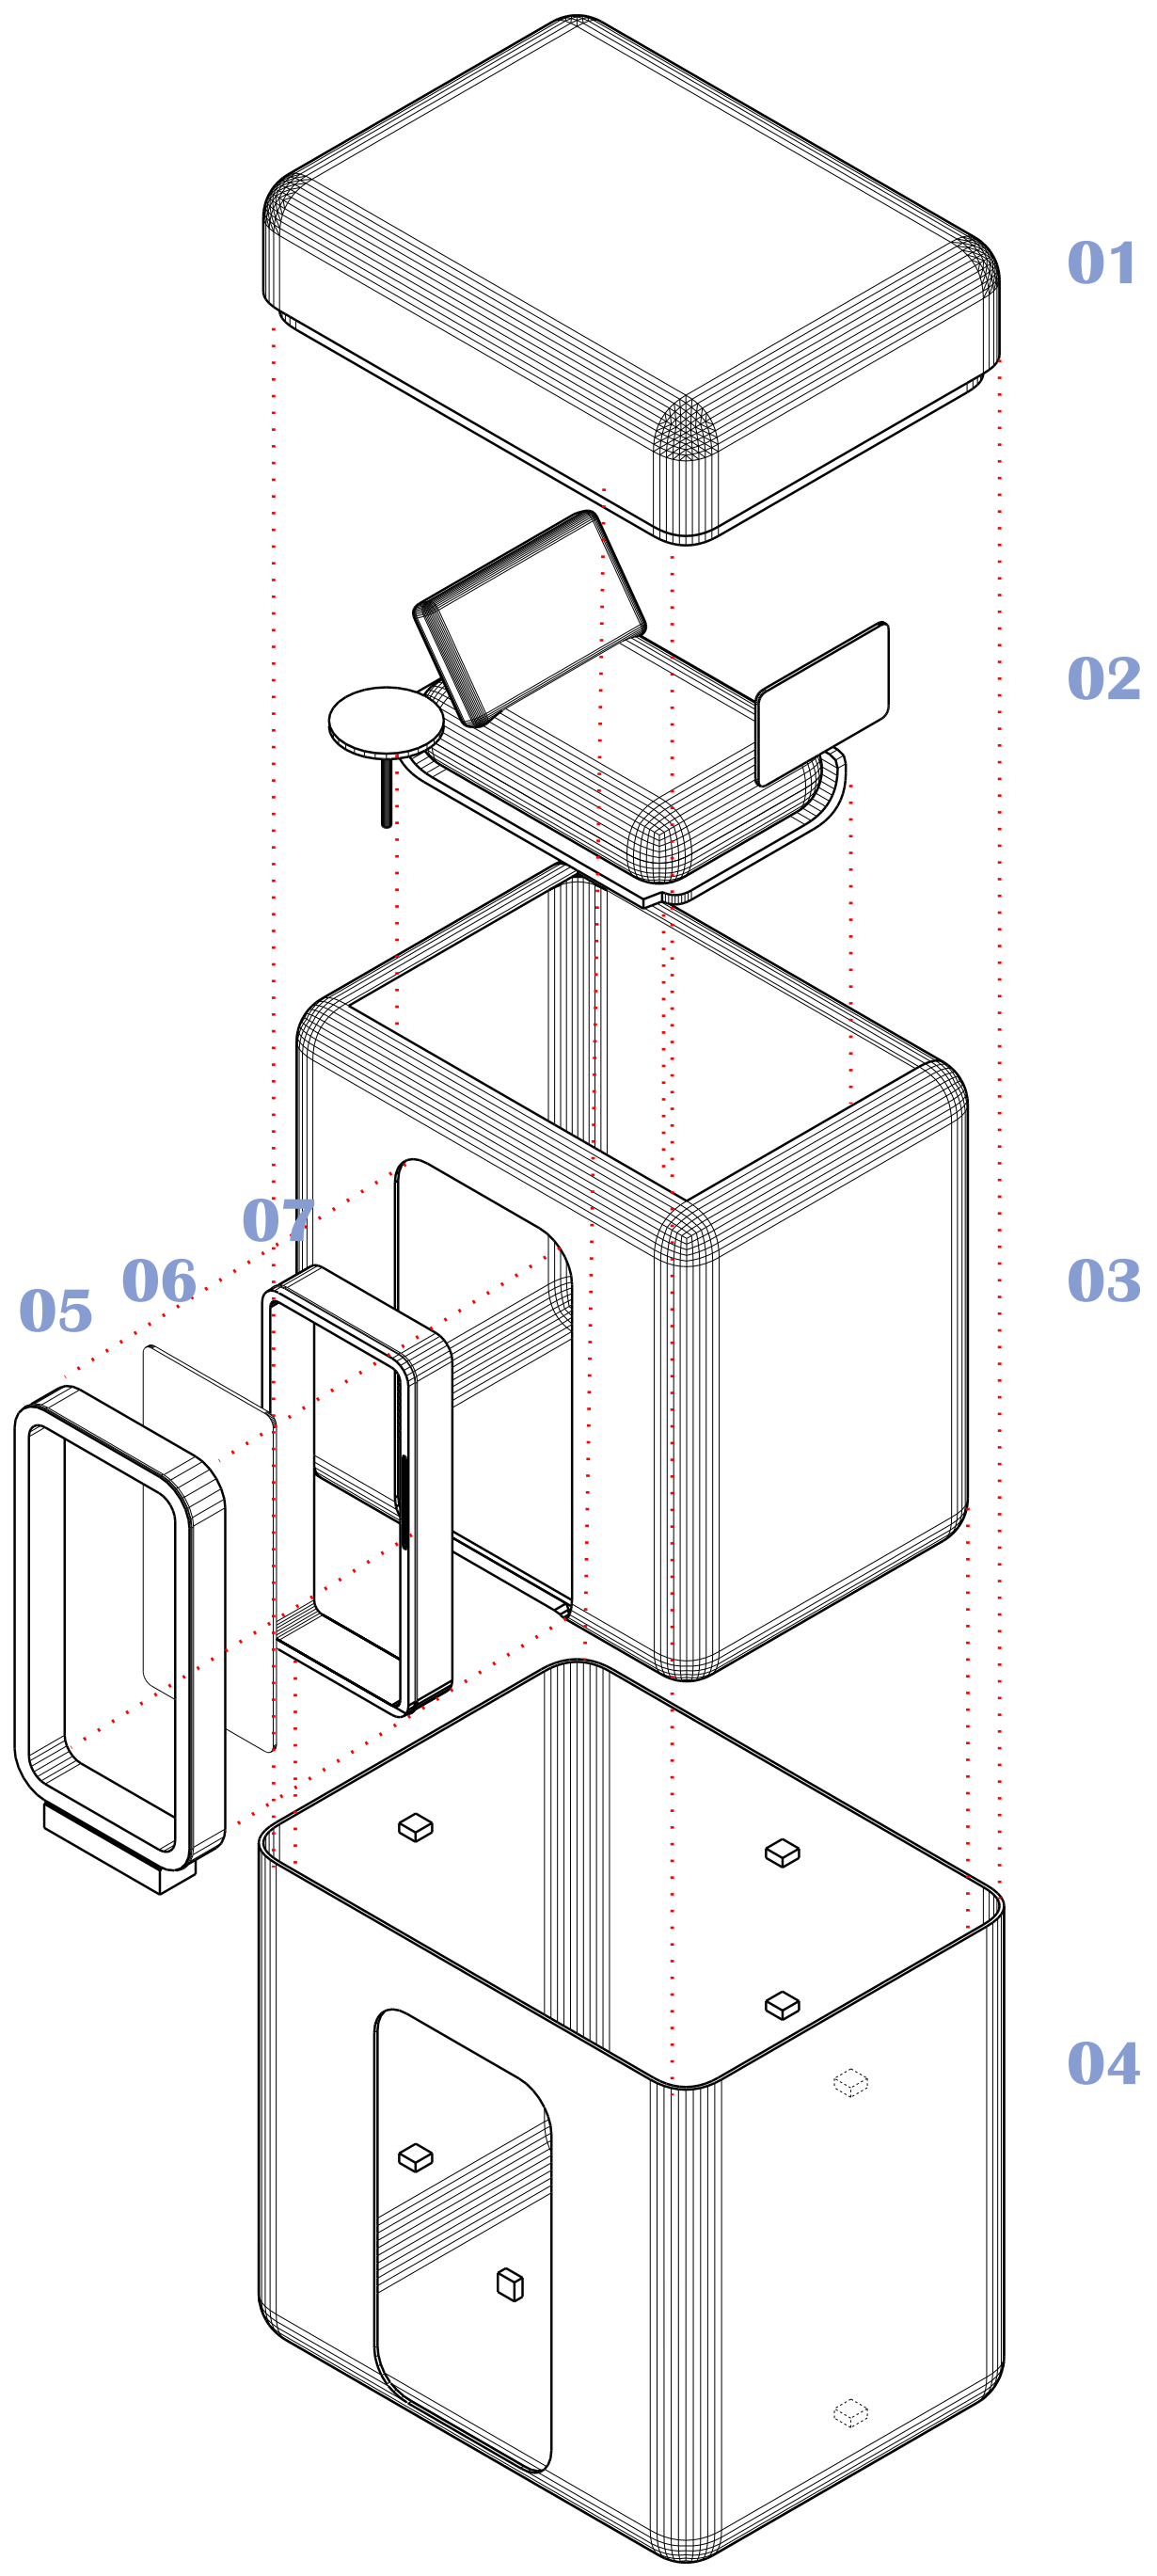


CONSTRUCTION L'ASSISE DE L'ESPACE D'ÉCOUTE COLLECTIVE

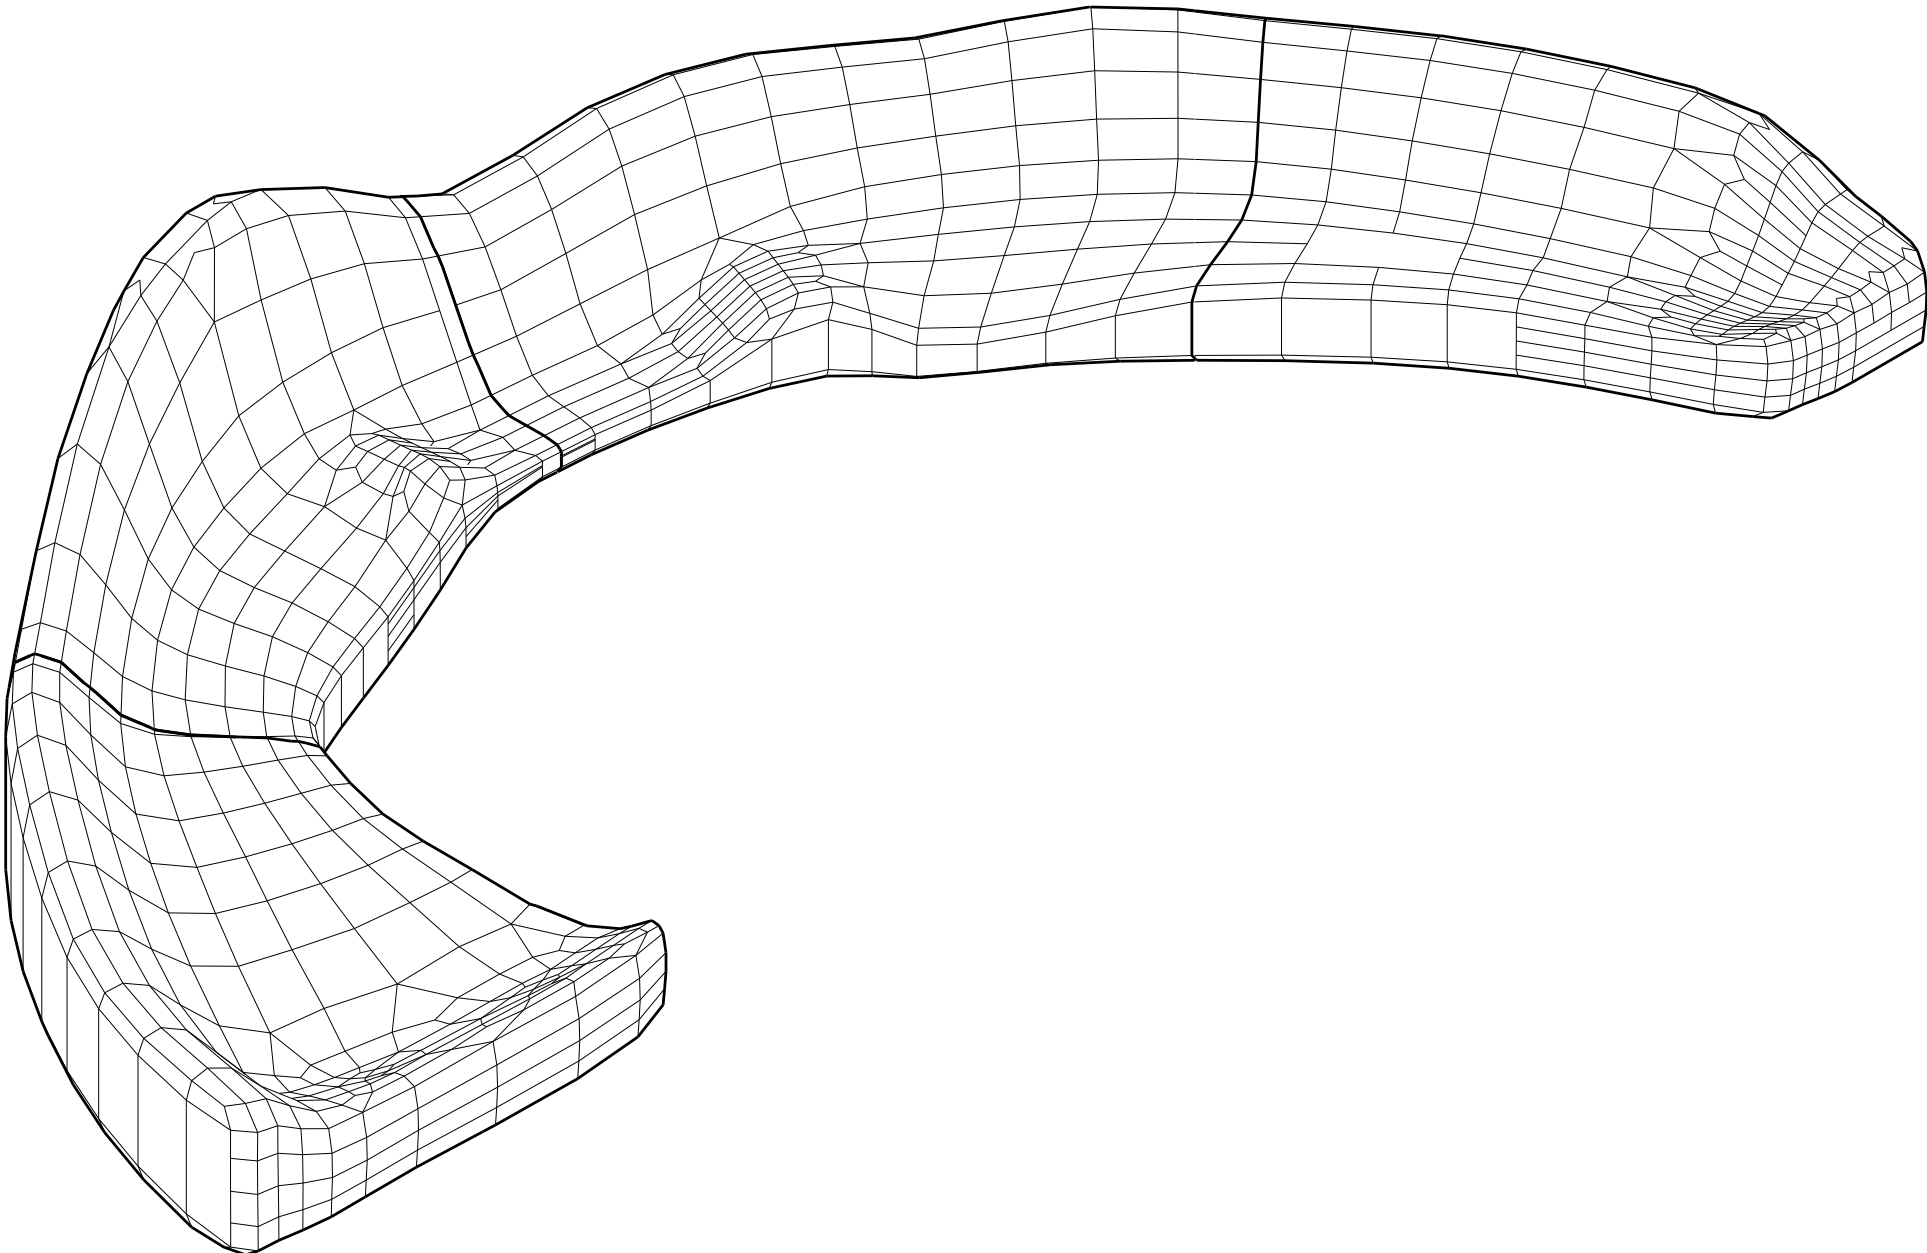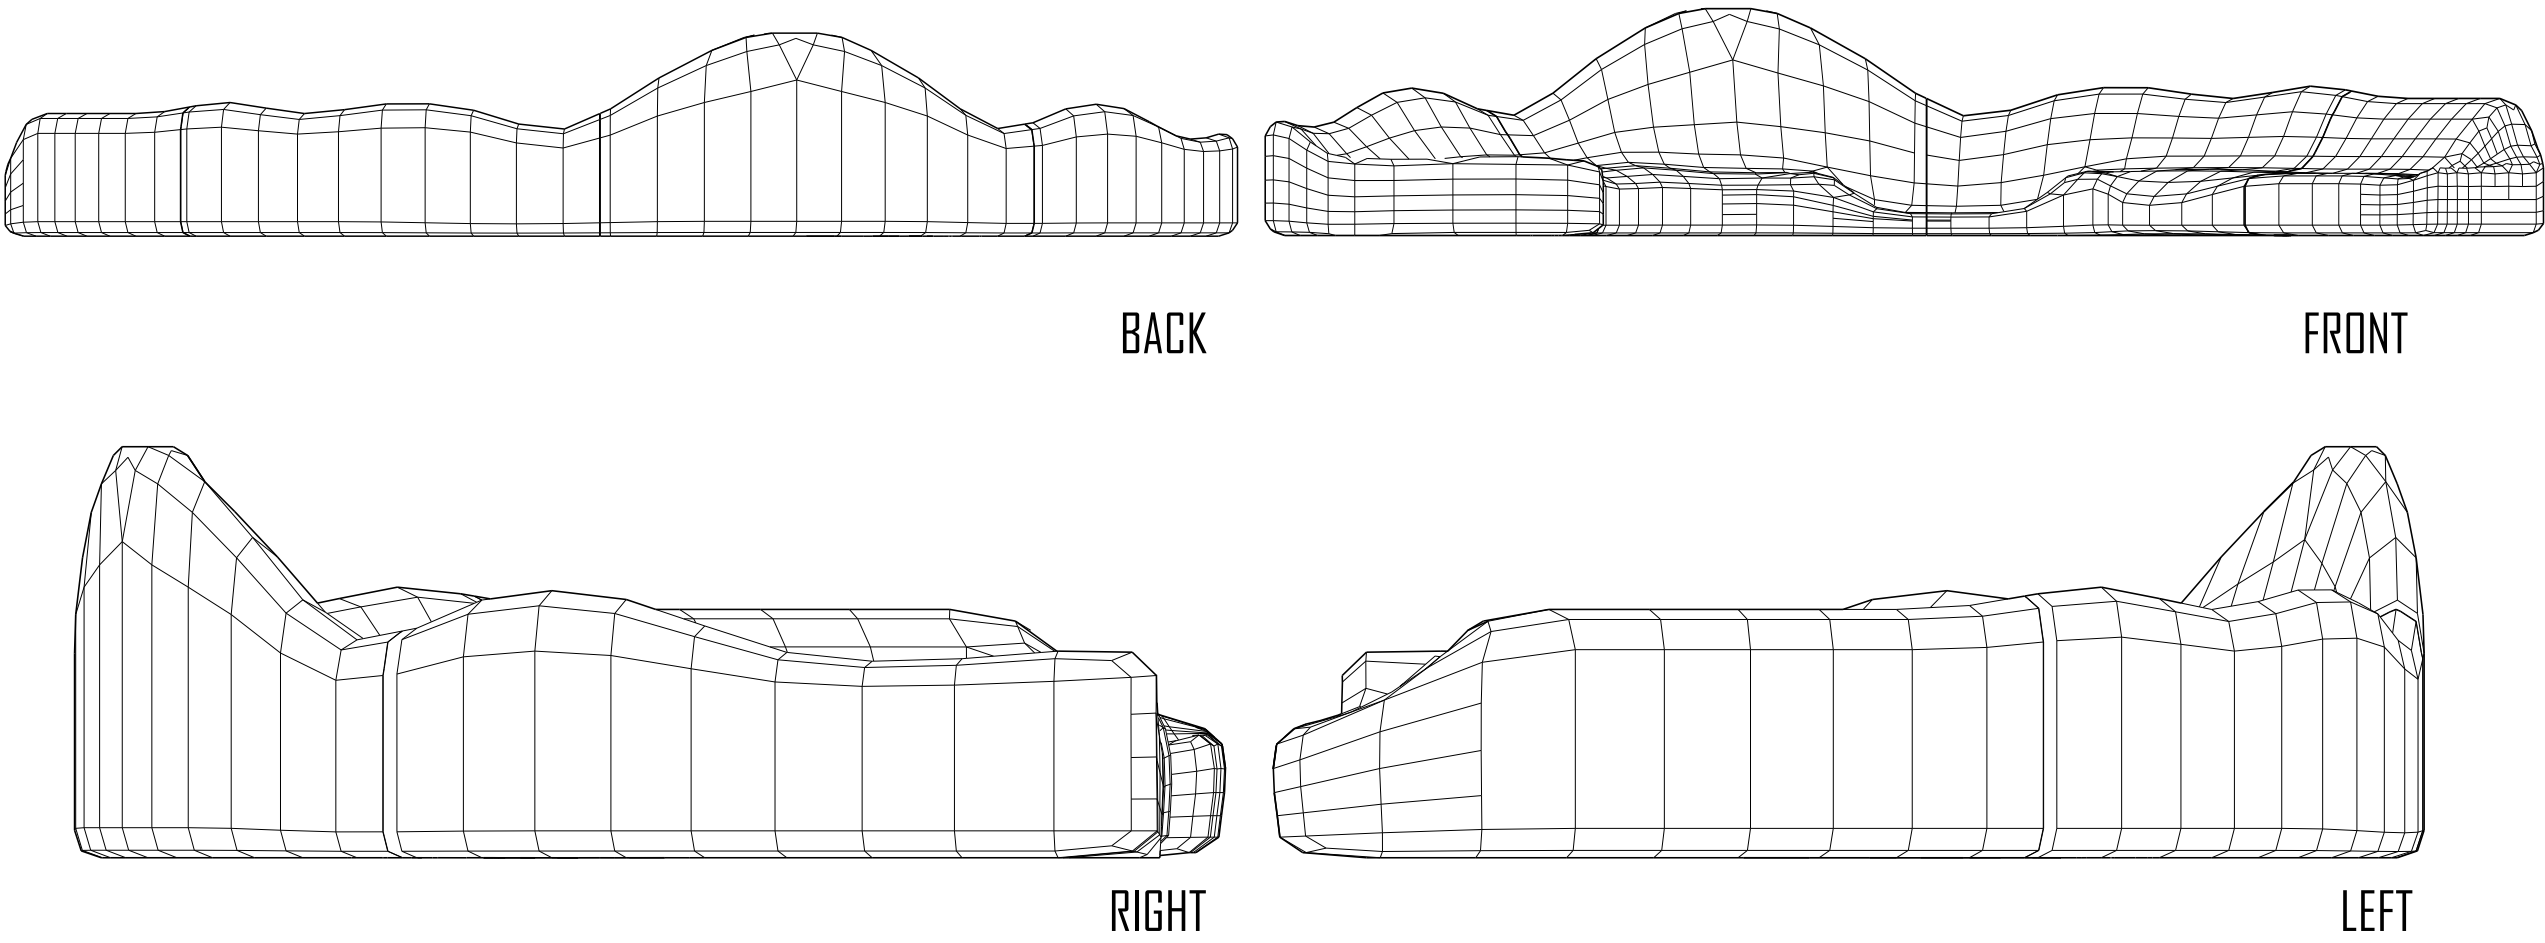

AXONOMÉTRIE

AXONOMÉTRIE ÉCLATÉE

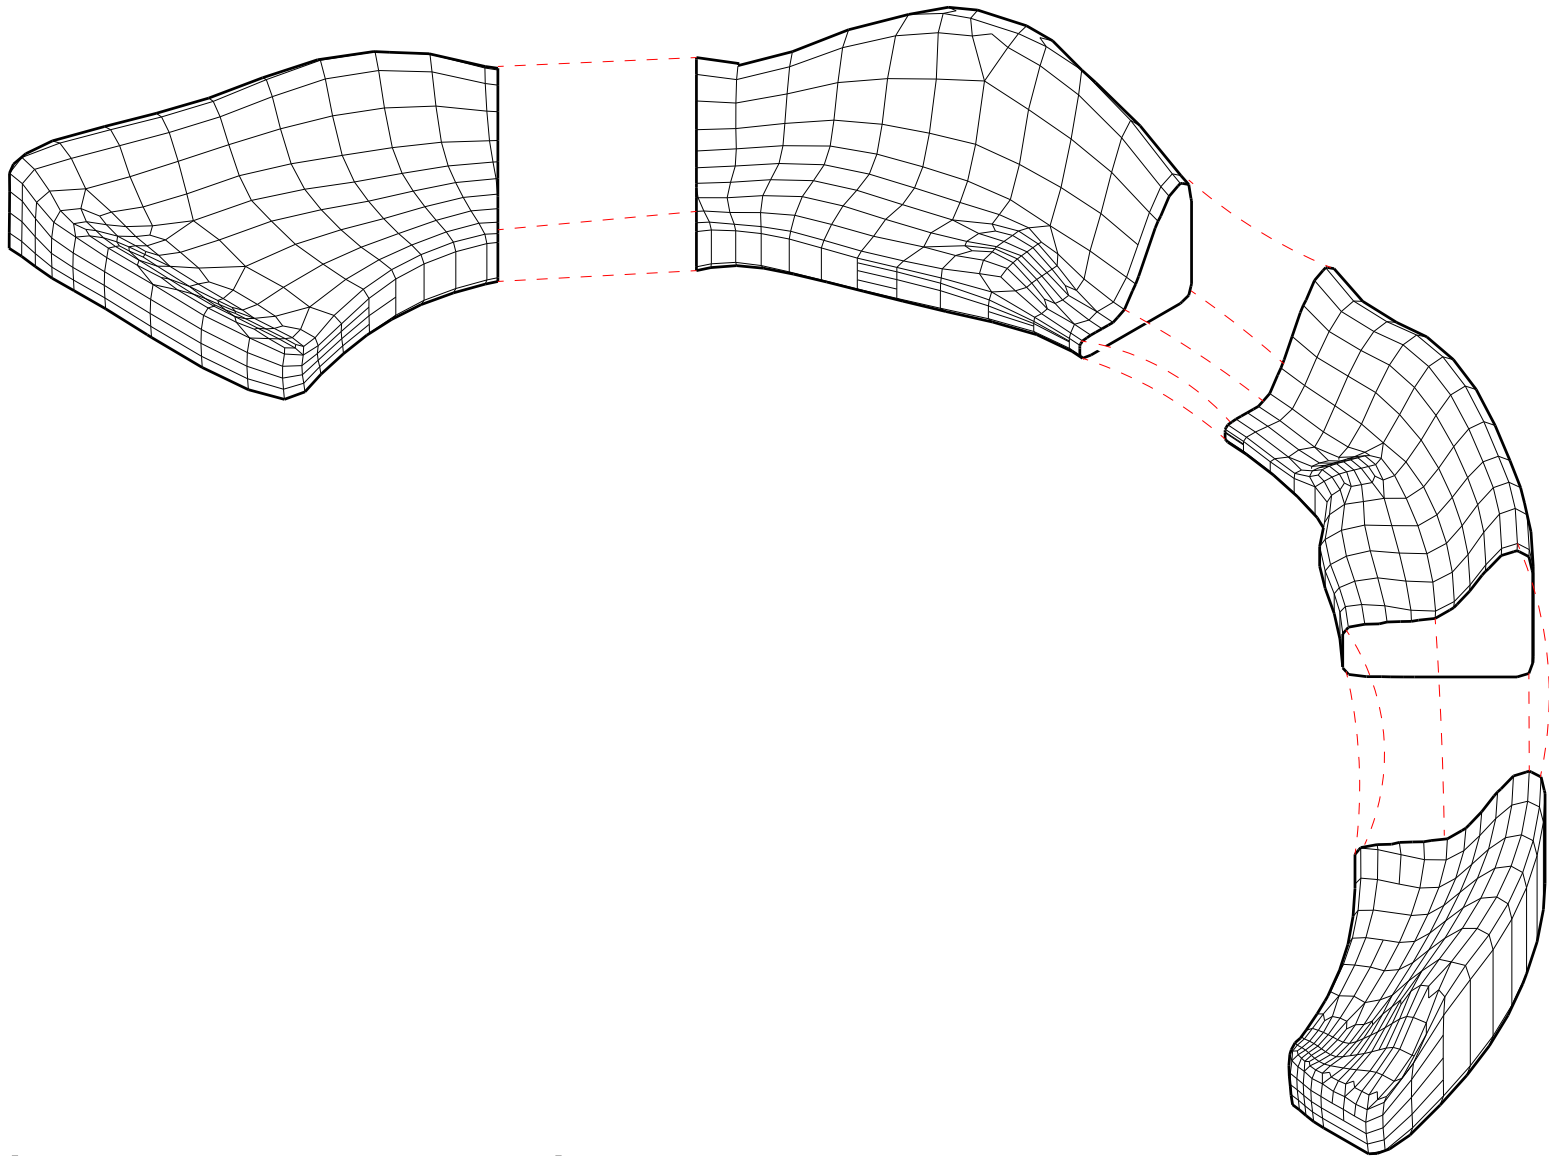

DÉTAIL A - COUPE SUR L'INTÉRIEUR D'UN MODULE

01 - Revêtement textile

Tissu acoustique / tissu d'ameublement

02 - Quate de finition

Couche souple de finition

03 - Mousse de confort


Mousse haute résilience

04 - Mousse de maintien

Mousse haute densité


05 - Ossature bois massif

Structure porteuse interne

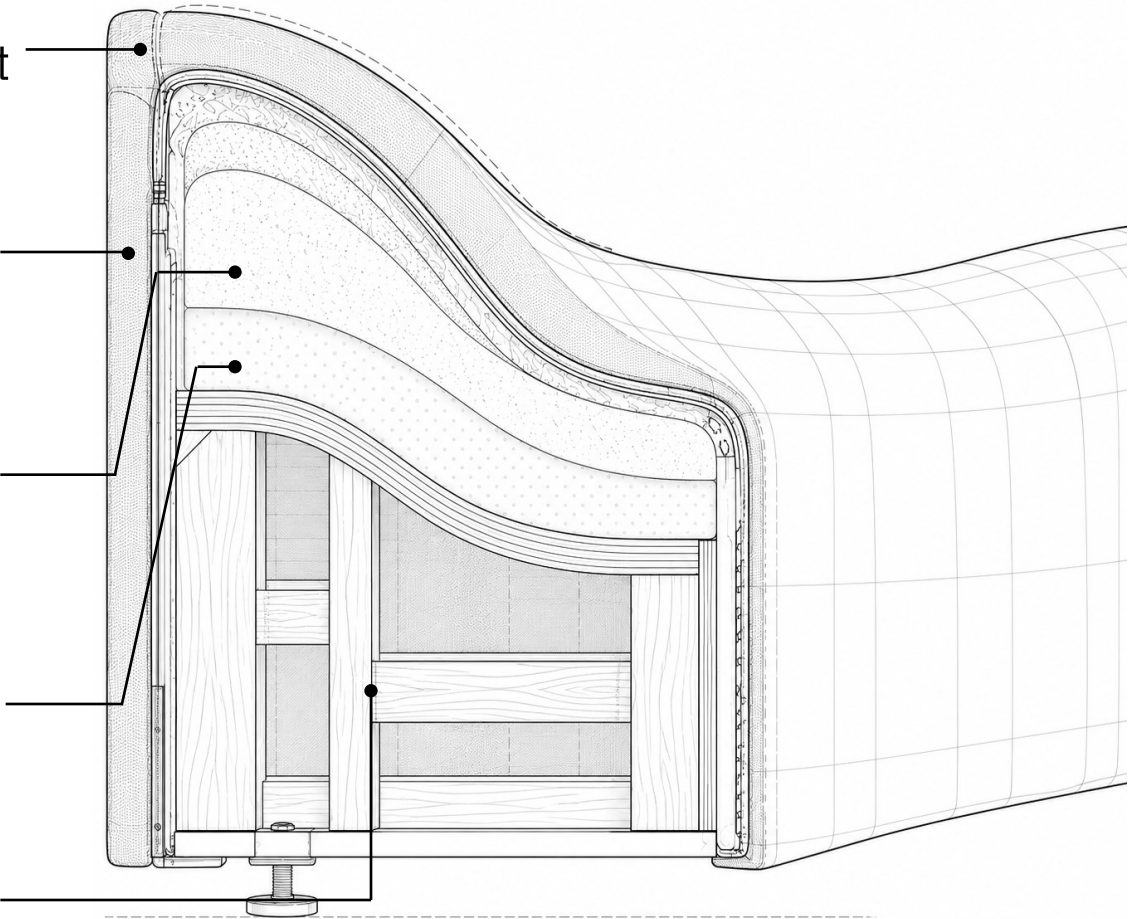

MATÉRIAUX

- 01 - IMPACT ACOUSTIC — TRACK WALL — LINEN 107
- 02 - ENDUIT À L'ARGILE — TEINTE TERRE / TAUPE
- 03 - CORTEX — CORKNATURA — LIÈGE RUSTIQUE VERNIS
- 04 - ARCELORMITTAL — INDATEN®
- 05 - BALSAN — ULTRASOFT SONIC CONFORT — 550
- 06 - KVADRAT — VIDAR 4 — BEIGE
- 07 - SHINNOKI — SMOKED WALNUT
- 08 - ZAHNER — OSCURA™ BLACKENED STEEL
- 09 - INOX EMBOSSÉ SUR MESURE — MOTIF ONDE SONORE

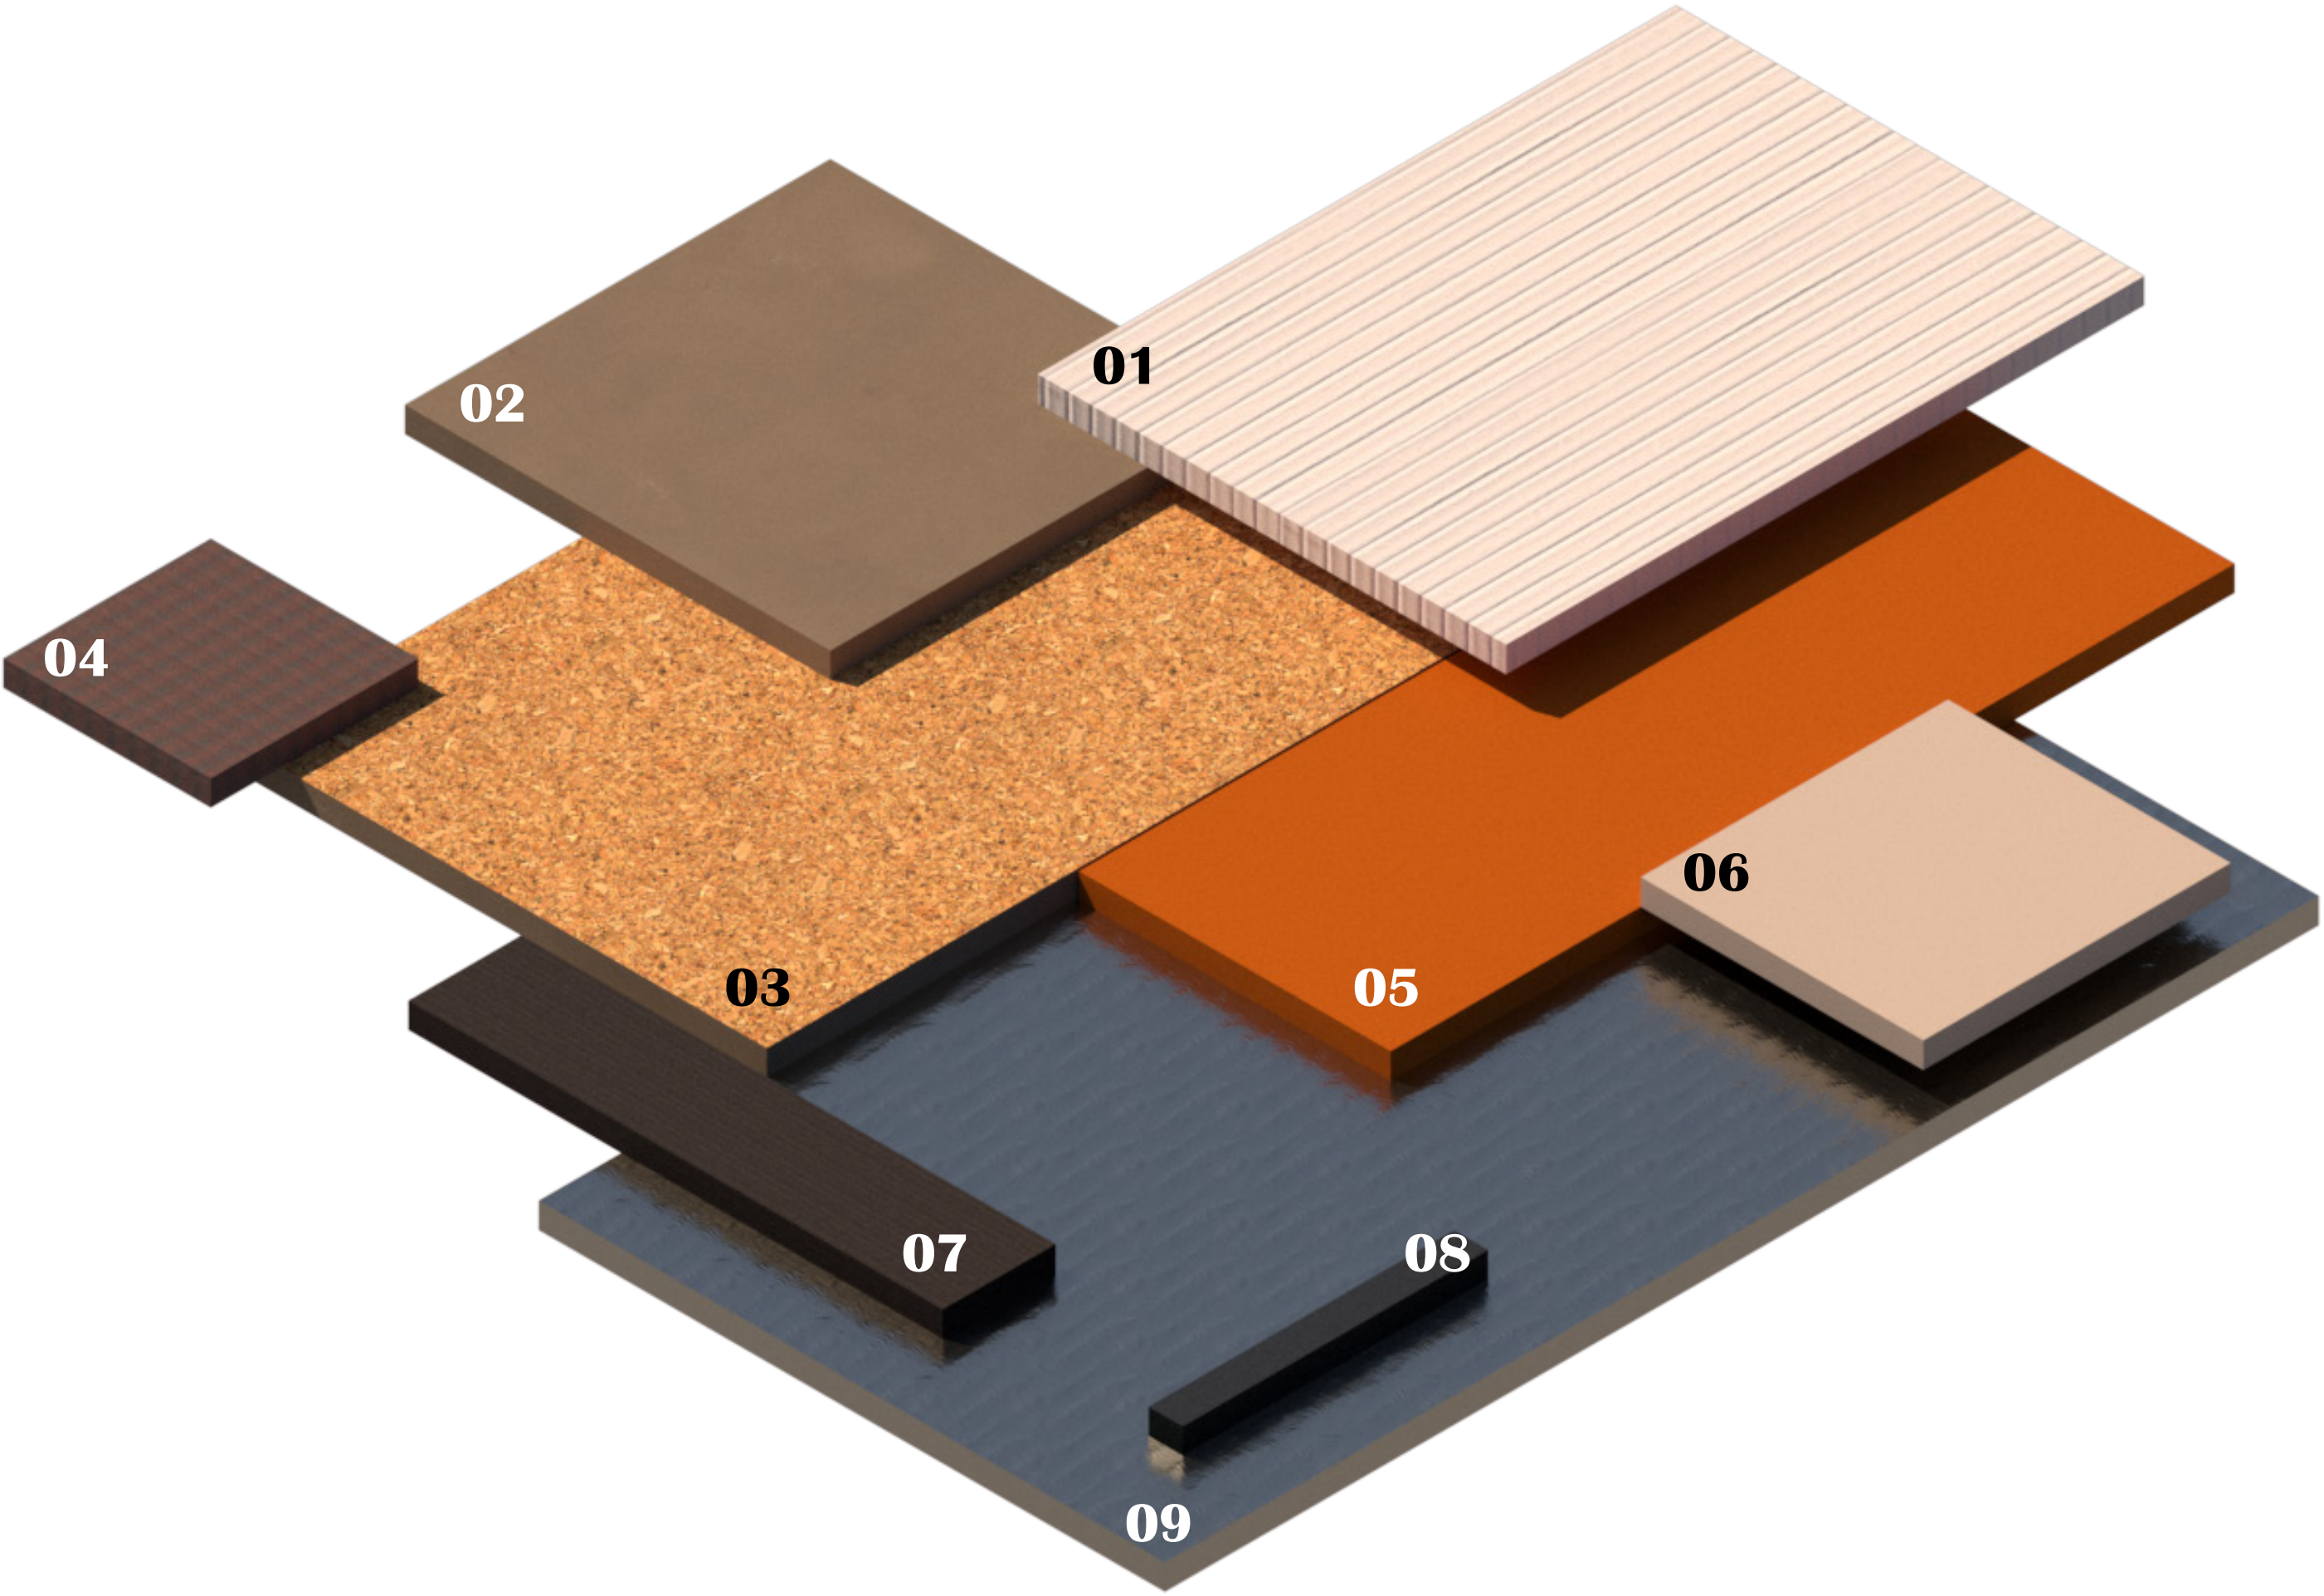





FLUENCE

L'HARMONIE ENTRE L'EAU, LE BOIS ET LA LUMIÈRE


Lieu : Vancouver, Canada (projet fictif)

Contexte : Expérimentation d'un espace fluide en bois, autour du mouvement et de la matière

Durée : Projet personnel – 2 semaines

Ce projet propose une expérience immersive où sport, détente et convivialité se rencontrent dans un même lieu. L'architecture met en valeur des matériaux nobles comme le bois, créant une atmosphère chaleureuse et raffinée. L'espace s'organise autour de trois pôles distincts : **une piscine** élégante au cœur du projet, **une salle de sport** intégrée pour une approche complète du bien-être, et **un espace de restauration** pensé comme un lieu de rencontre et de relaxation. L'harmonie entre les textures et la lumière sublime l'ensemble, offrant un cadre apaisant et sophistiqué.




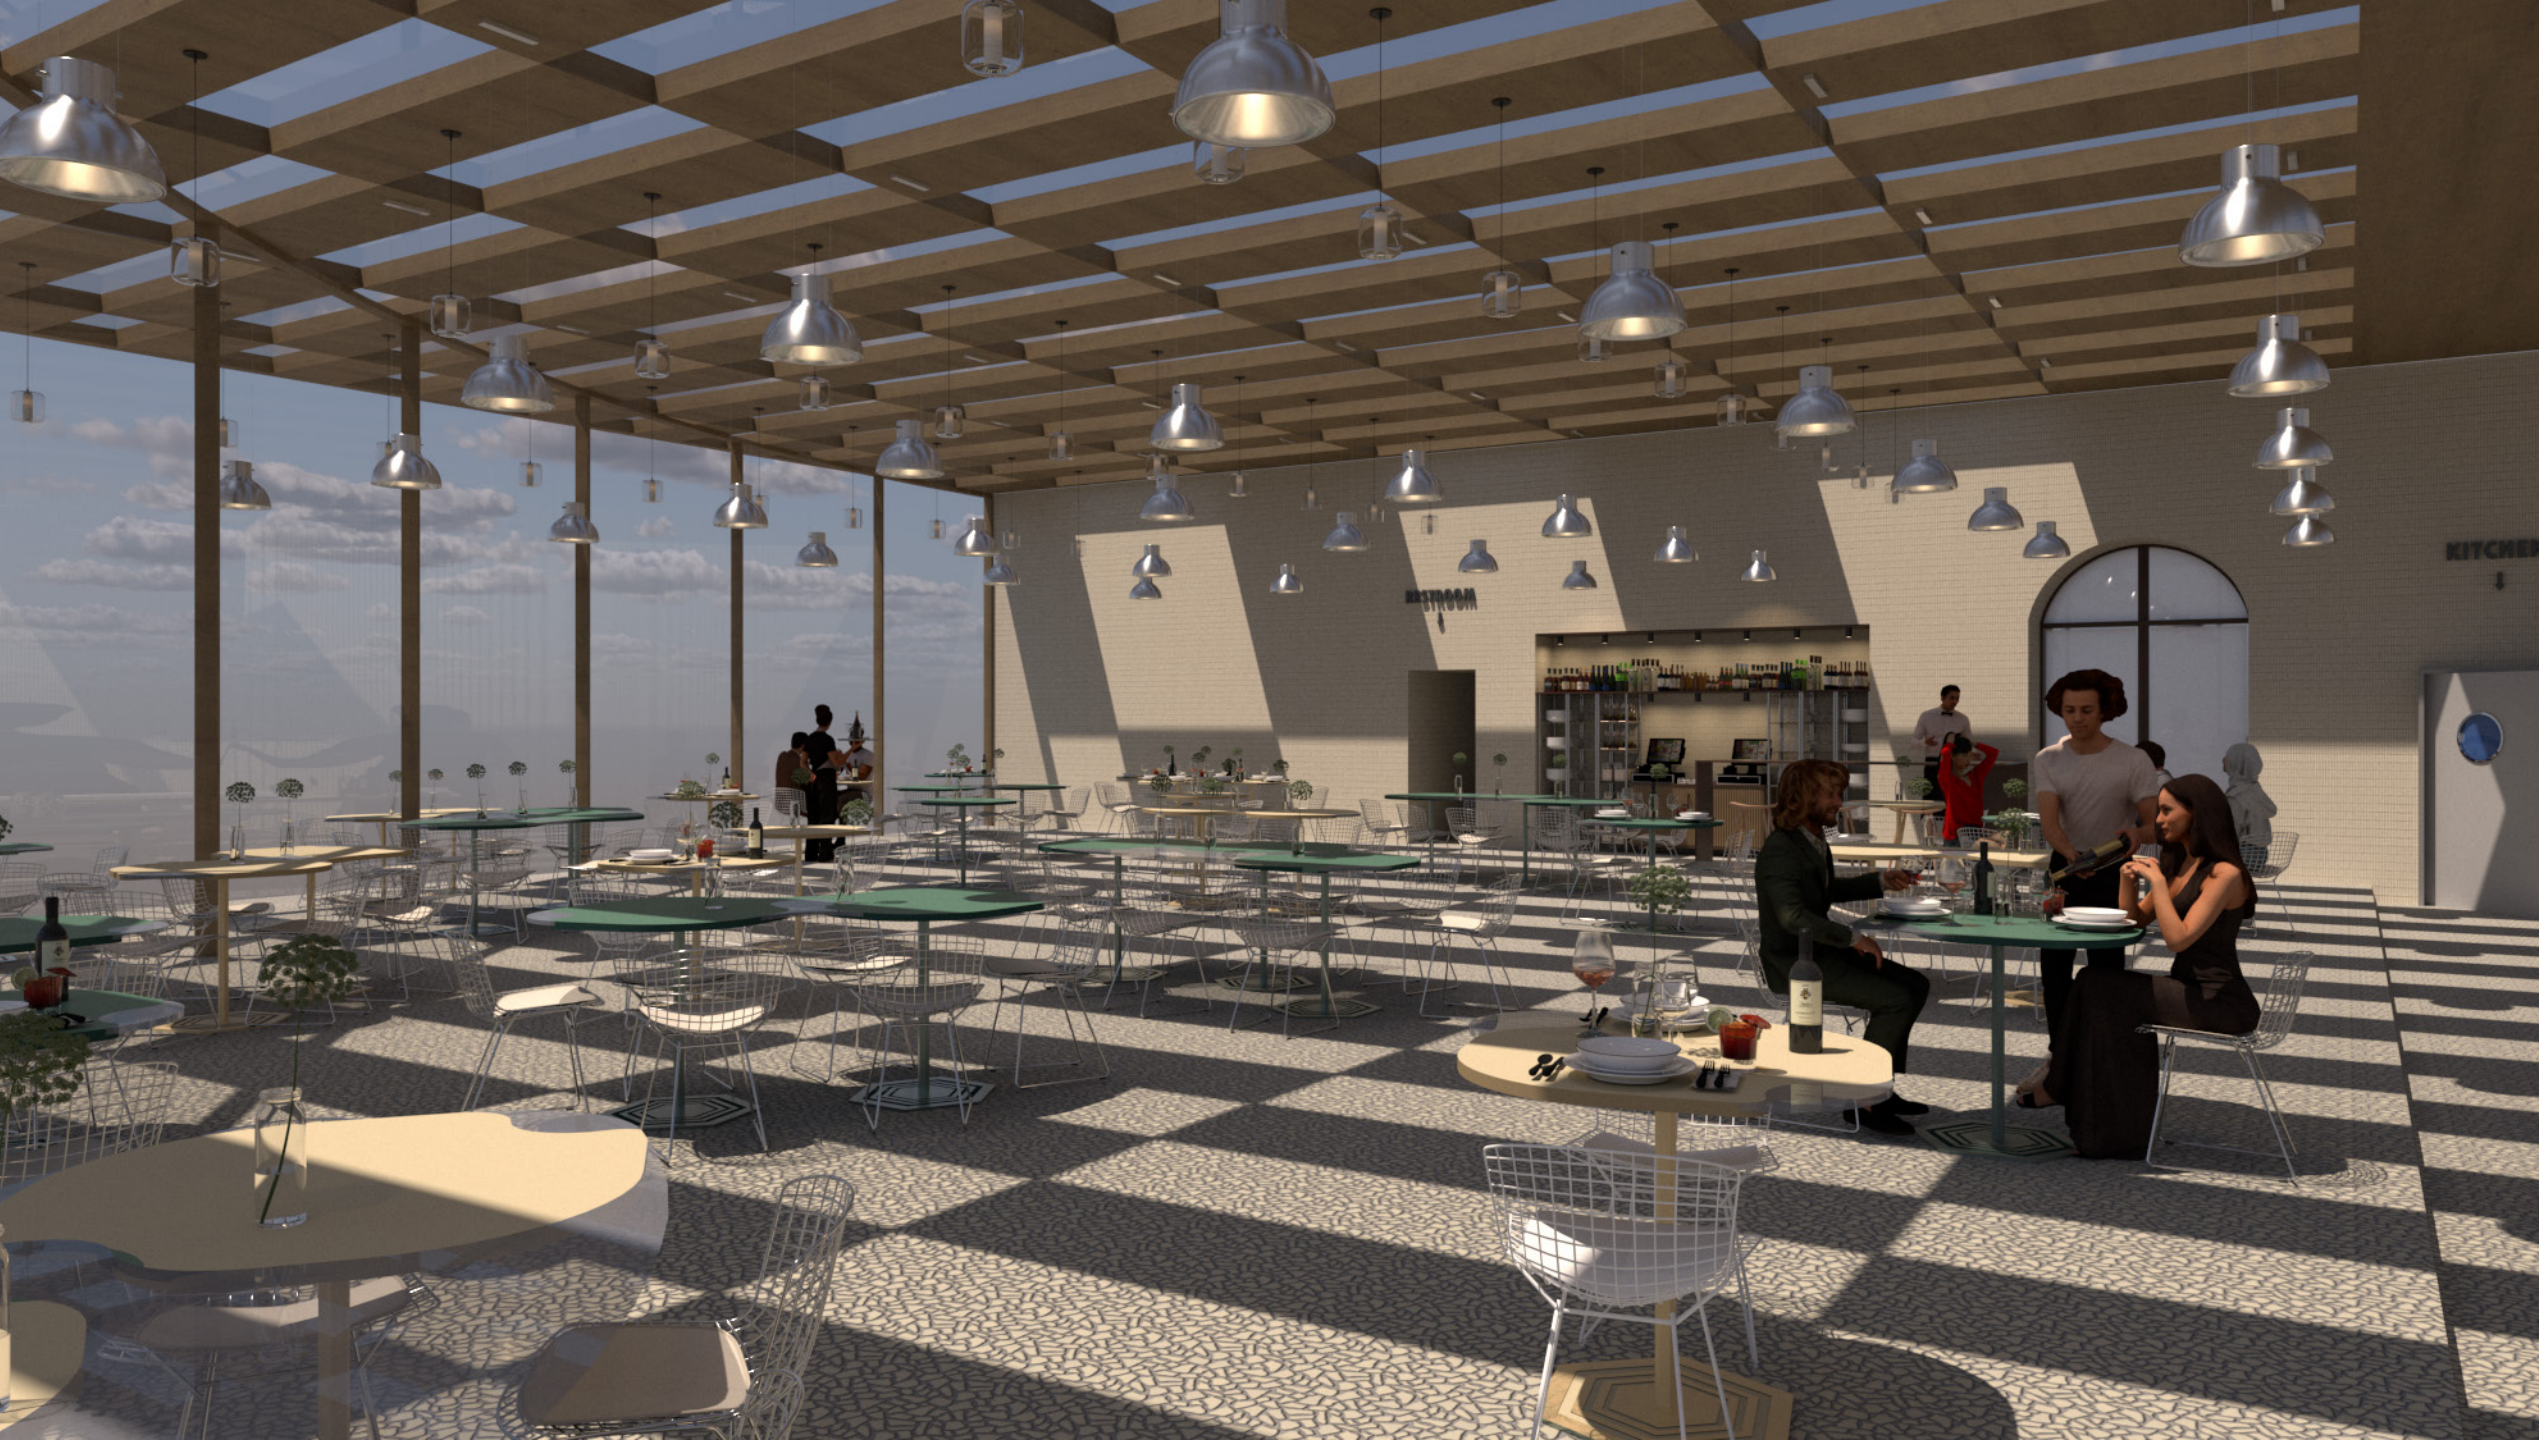

RESTAURANT



SALLE DE SPORT

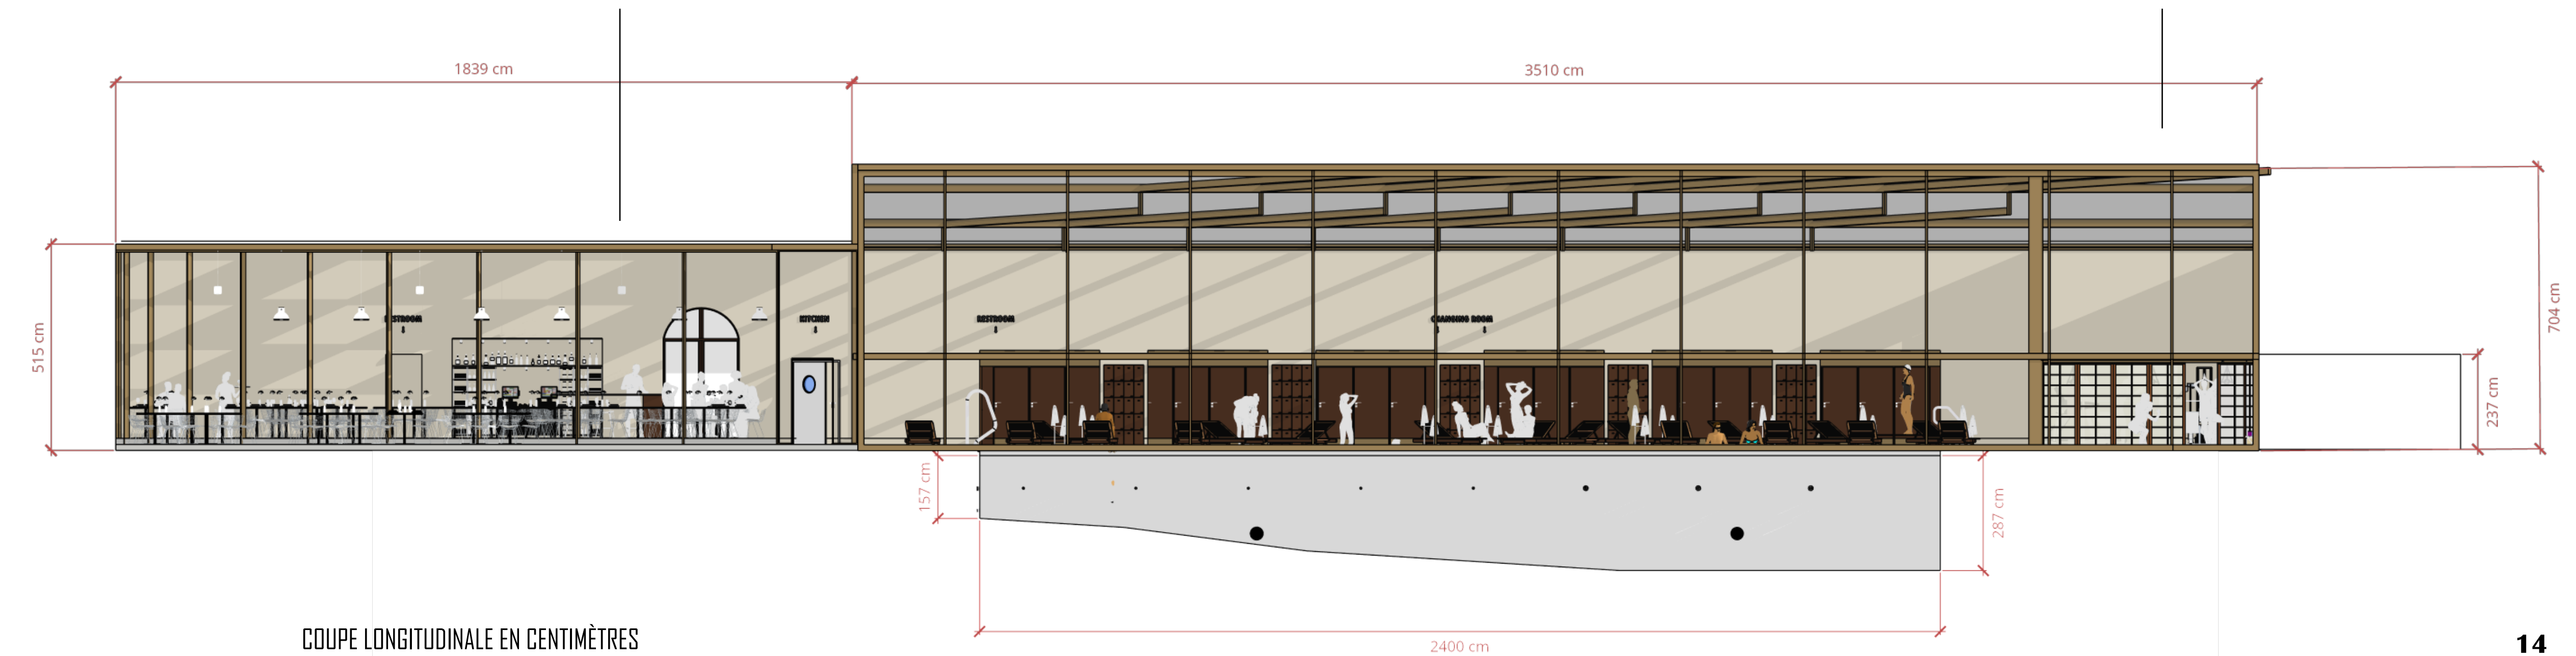

COUPE LONGITUDINALE EN CENTIMÈTRES



FITNESS CENTER

WAVEWOOD

L'ESSENCE DU BOIS EN MOUVEMENT

Lieu : Île d'Oléron, France (projet fictif)

Contexte : Expérimentation d'un espace fluide en bois, autour du mouvement et de la matière

Durée : Projet personnel – 2 semaines


Ce projet réaménage l'entrée d'une maison en un grand espace de vie composé d'un salon, d'une salle à manger et d'une cuisine ouverte.


Les différentes zones sont définies par la géométrie du plan et la fluidité de la circulation, dans un volume aux **murs en béton brut**.

De larges ouvertures latérales diffusent une lumière naturelle constante, animée par les ombres projetées des **poutres courbes en bois** apparentes au plafond.

Le mobilier intégré prolonge les lignes architecturales et renforce la cohérence de l'ensemble.



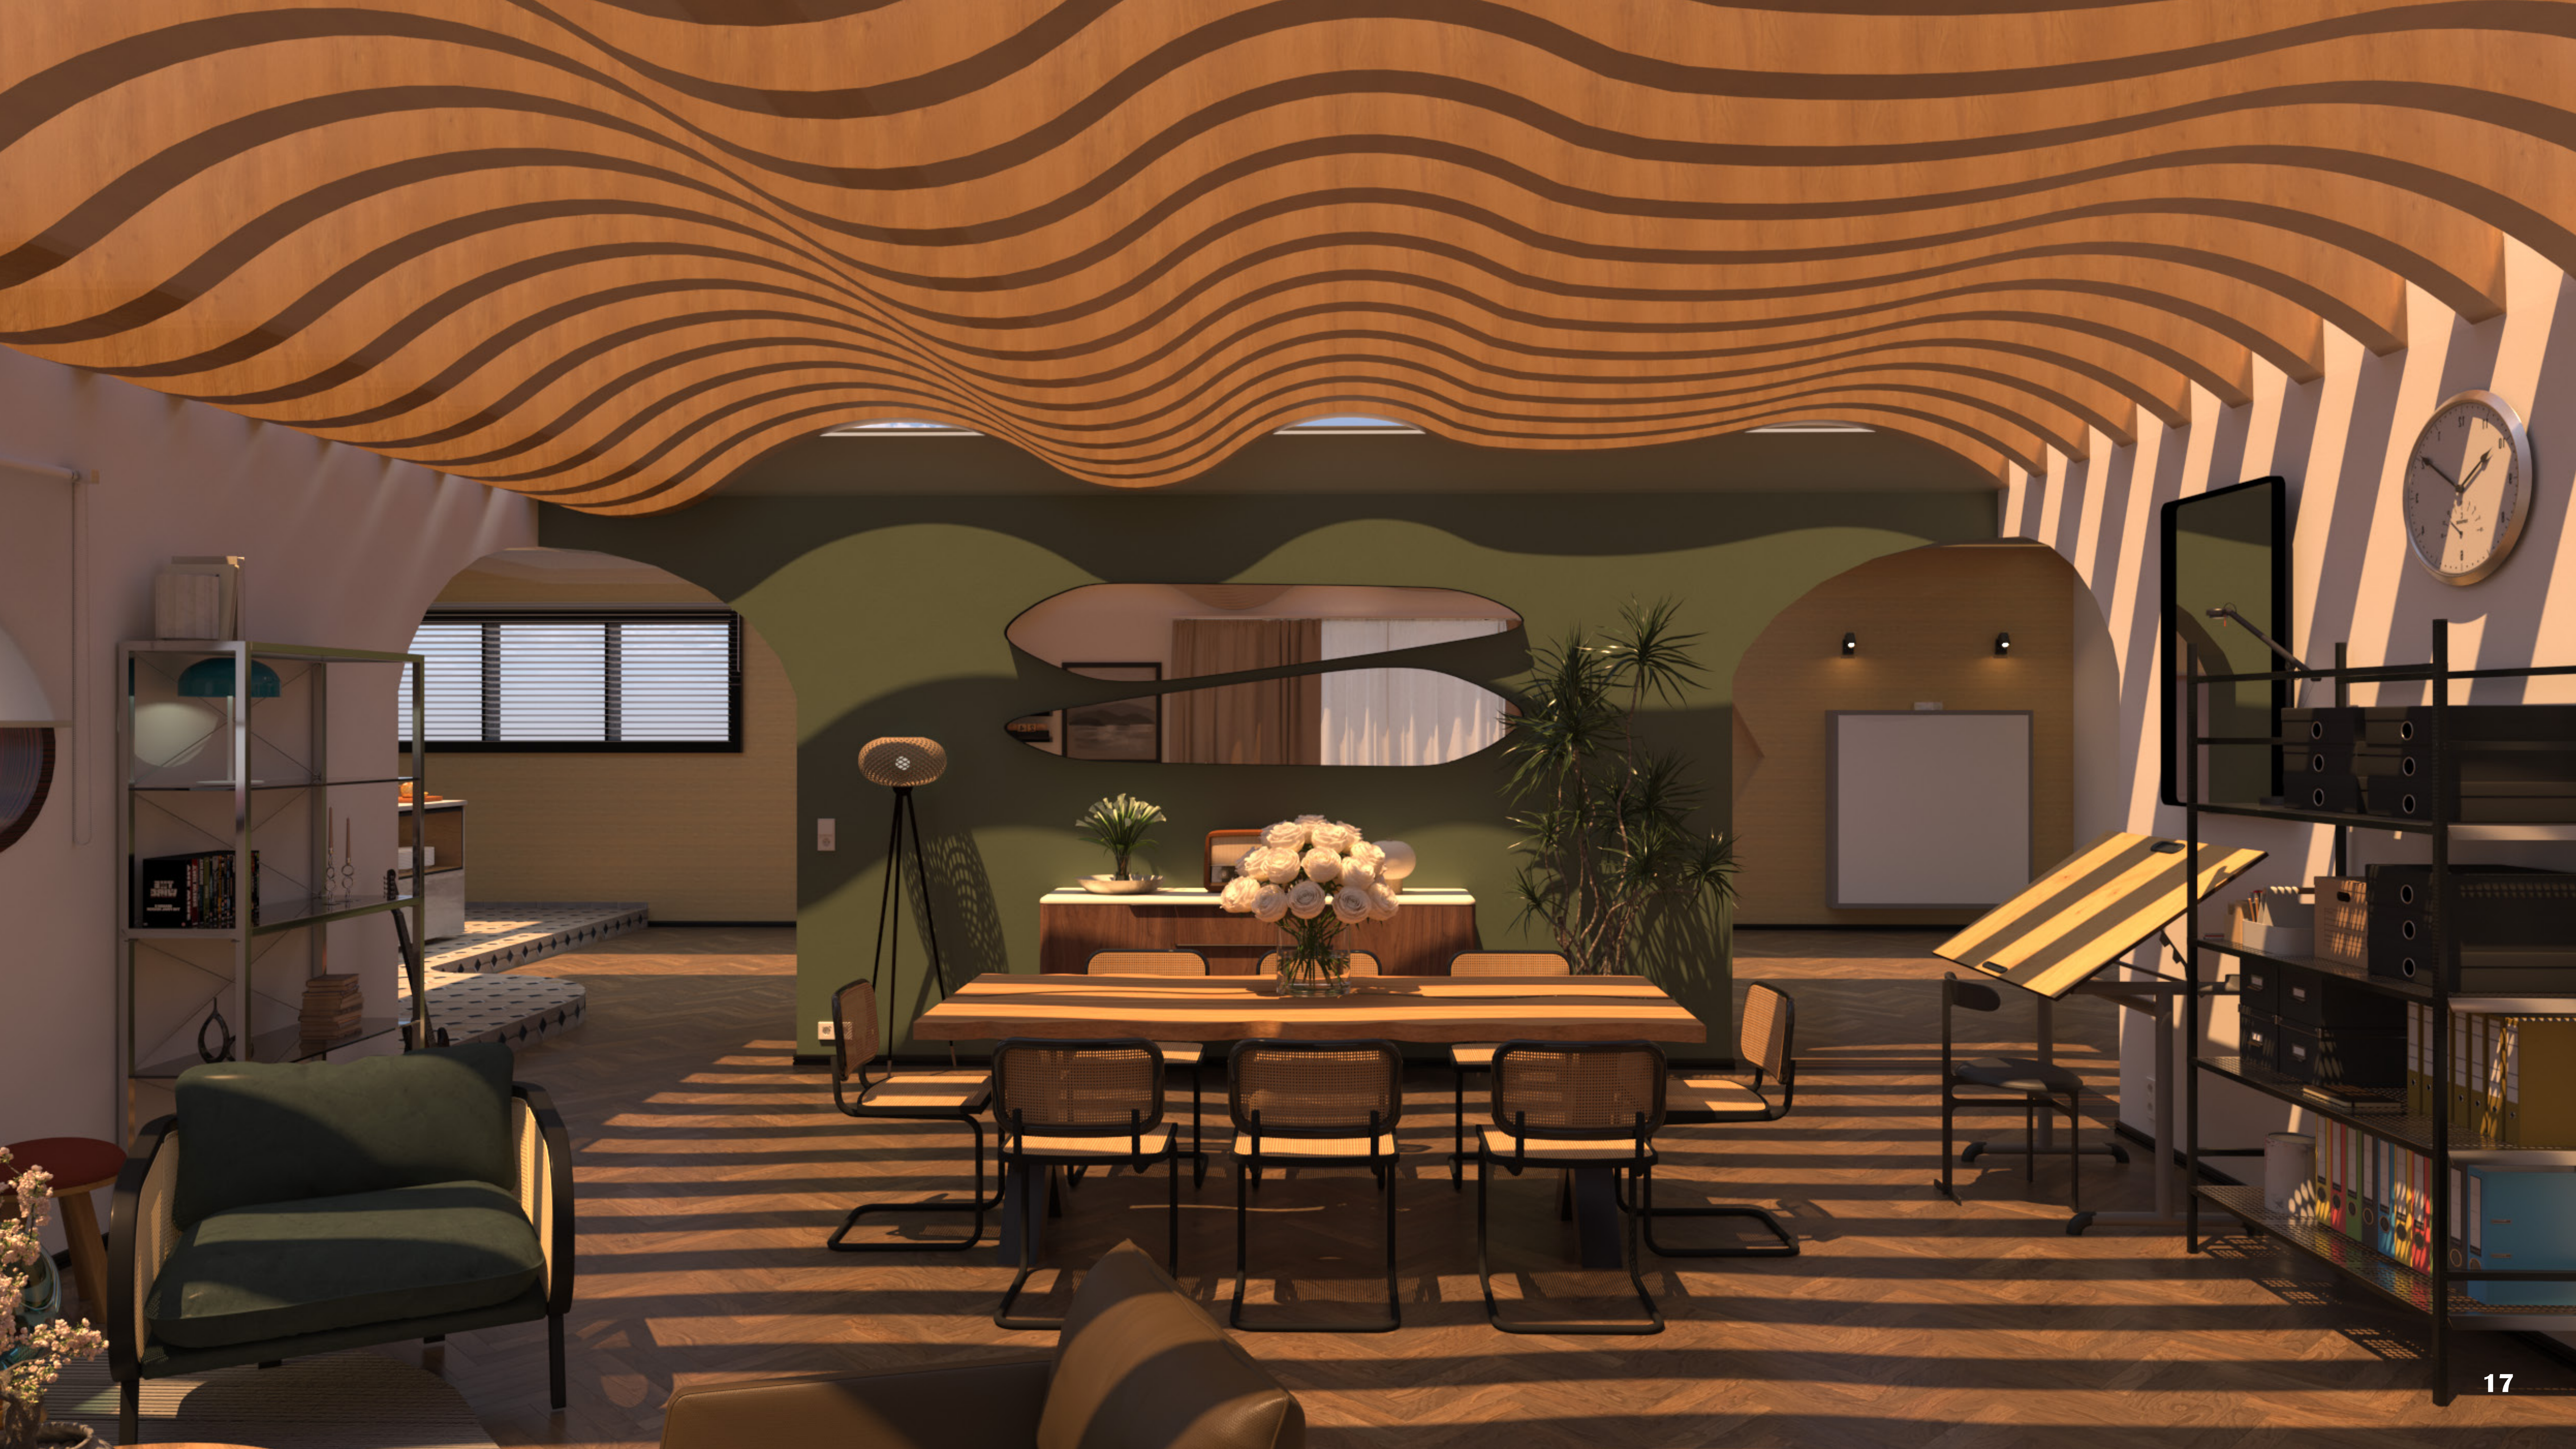

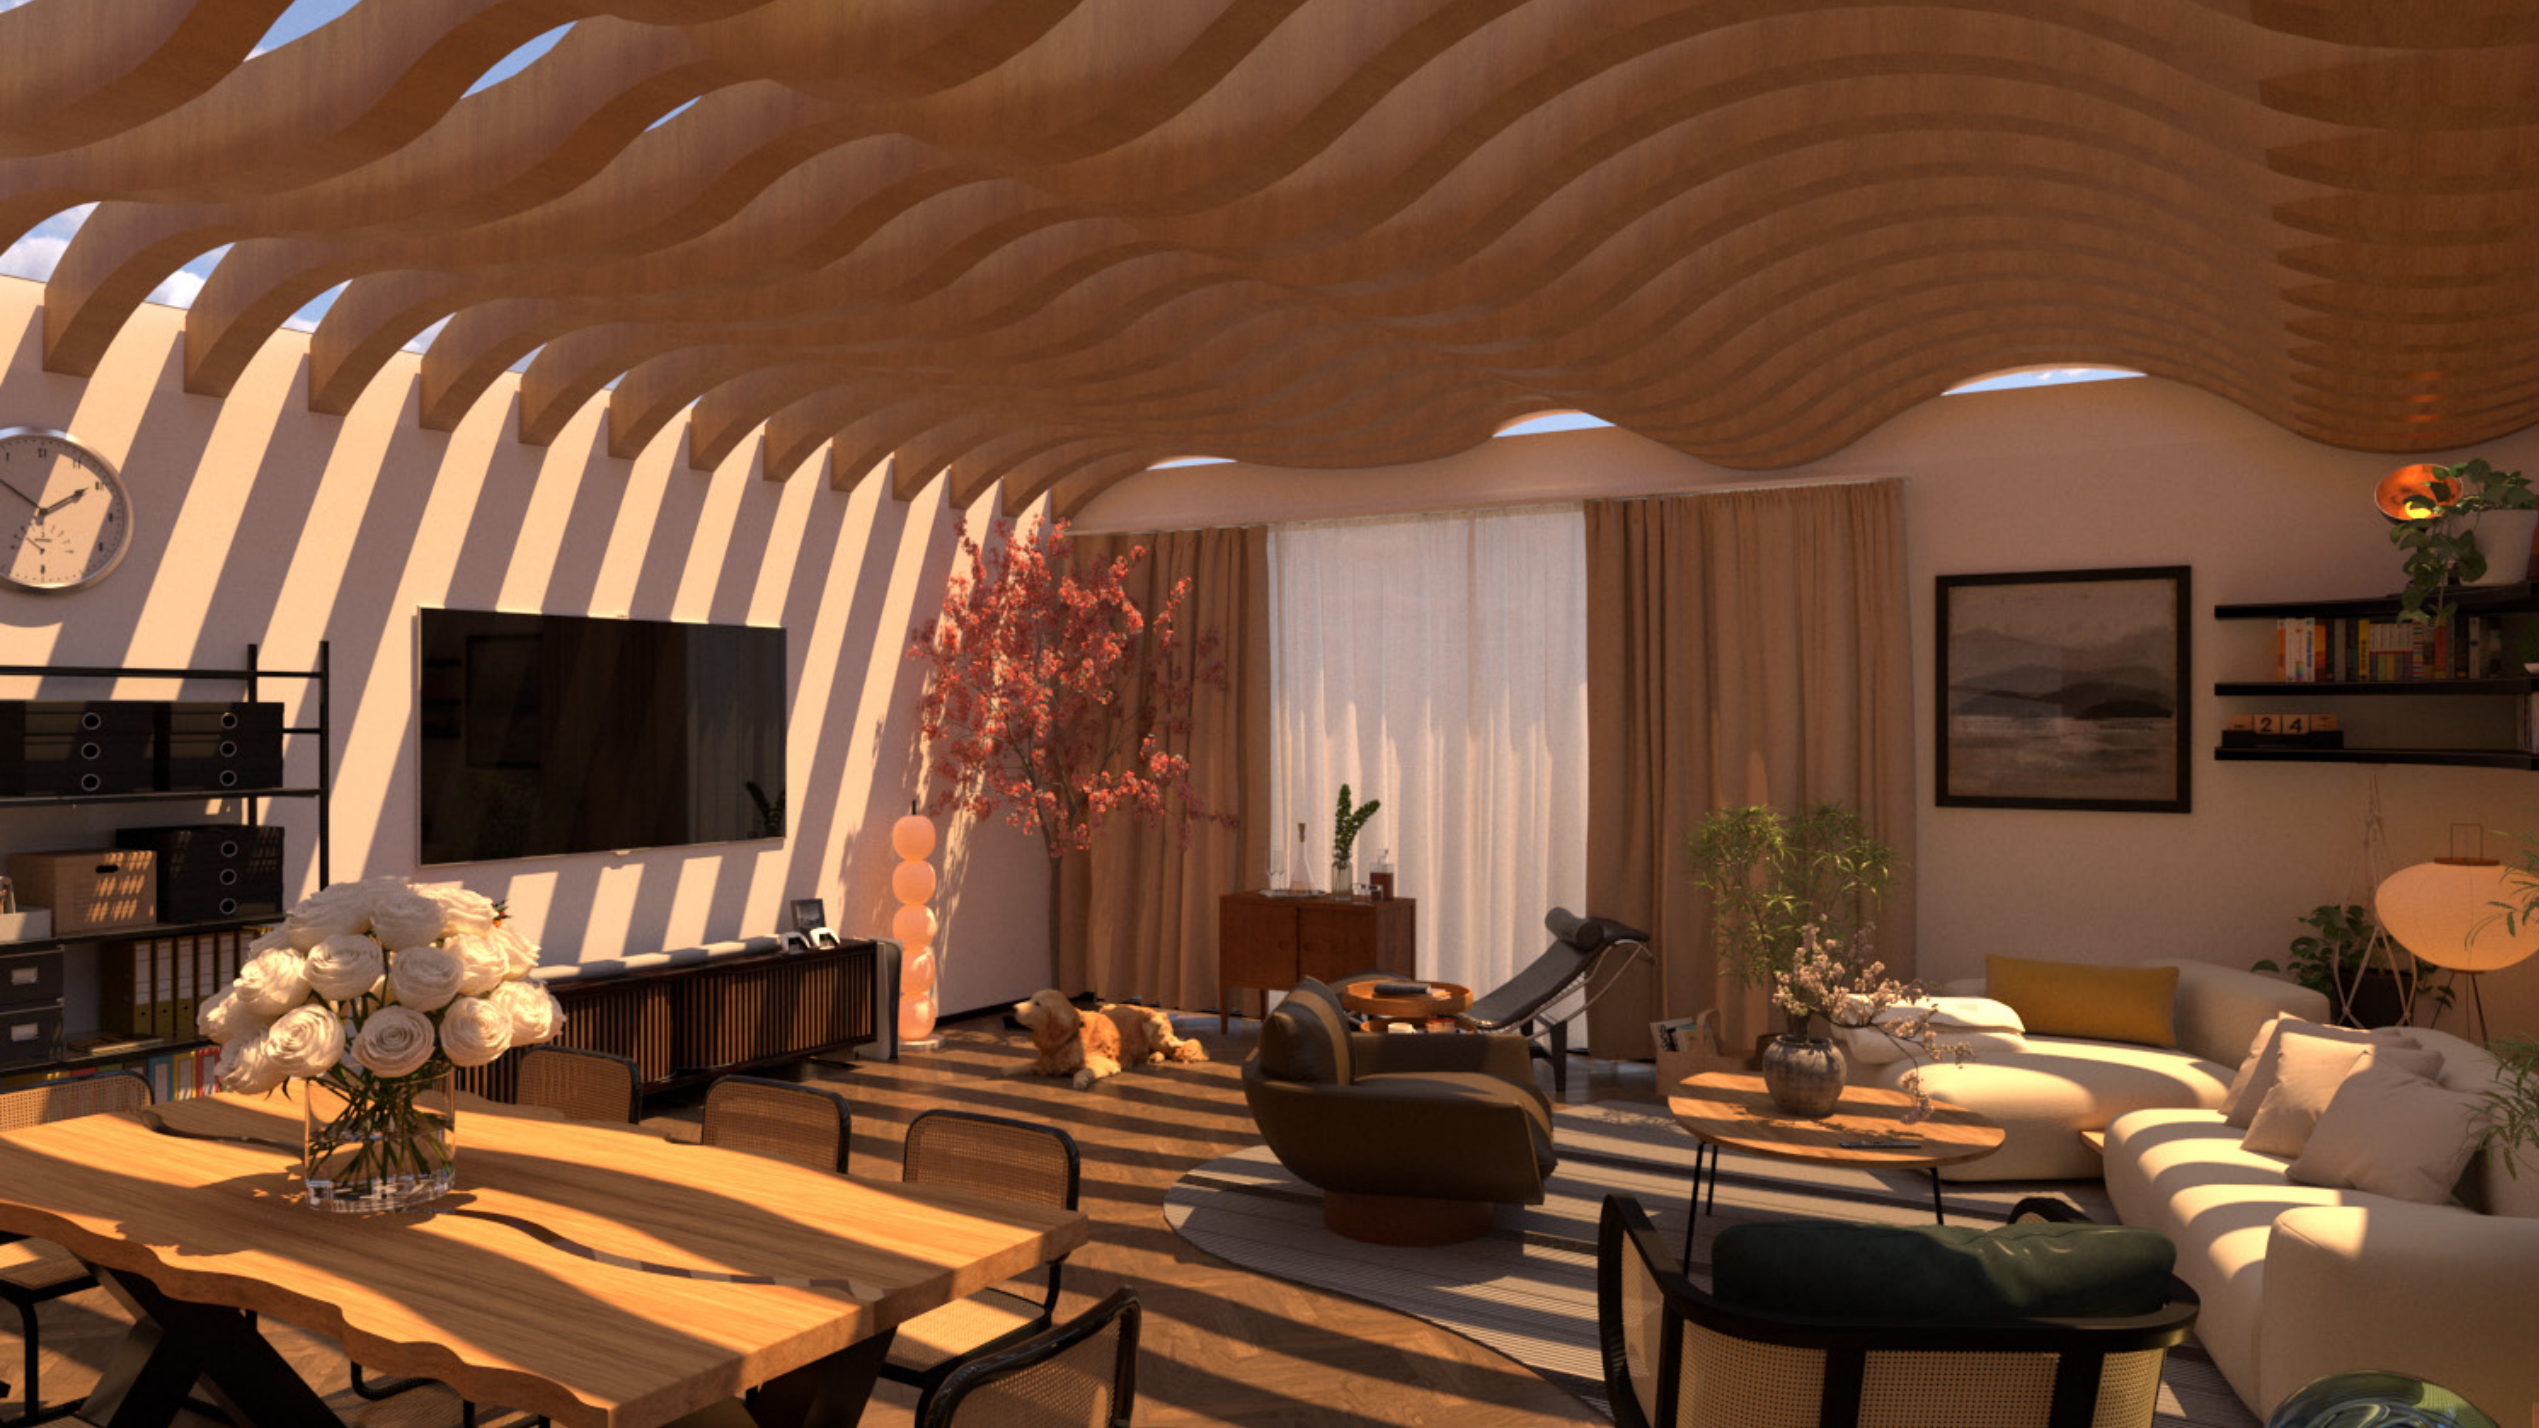

L'ATTENTE, REPENSÉE

UN ESPACE DE TRANSITION POUR APAISER LES VOYAGEURS

Lieu : Gare de Surgères, France (projet fictif)

Contexte : Réaménagement de l'espace d'attente pour améliorer le confort des voyageurs

Durée : Projet académique – 6 semaines


Ce projet réinvente l'espace d'attente de la gare de Surgères, en s'adressant particulièrement aux **voyageurs anxieux** ou **peu familiers avec le train**. **Trois zones** distinctes permettent une **transition progressive** : des assises hautes pour les départs imminents, un espace assis pour une attente modérée, et une zone de détente avec des assises basses pour se relaxer pleinement. Une ambiance lumineuse et sonore accompagne le parcours, offrant une expérience **apaisante et immersive**.




COUPE TRANSVERSALE



PLAN

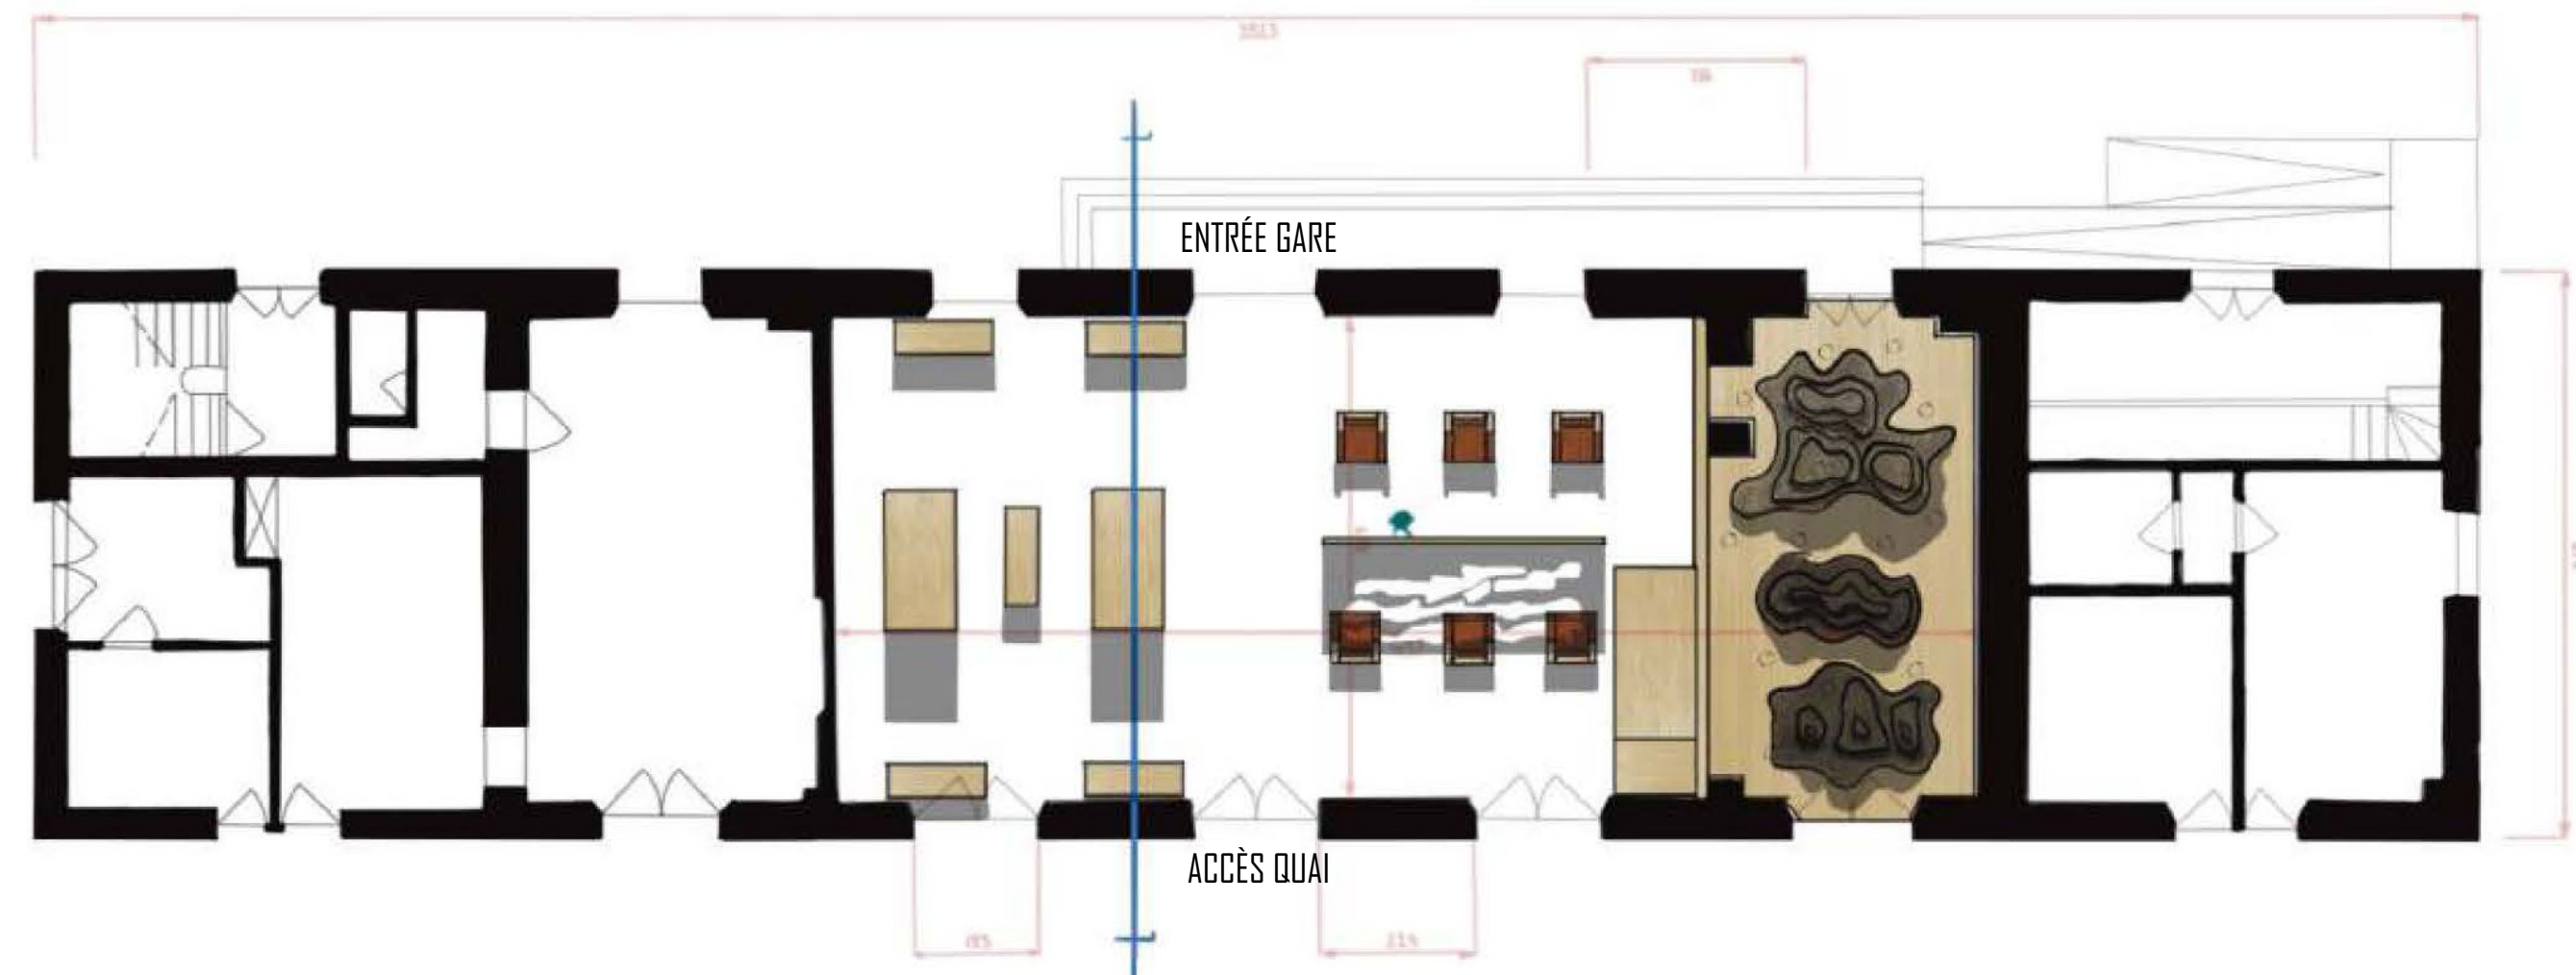

COUPE LONGITUDINALE

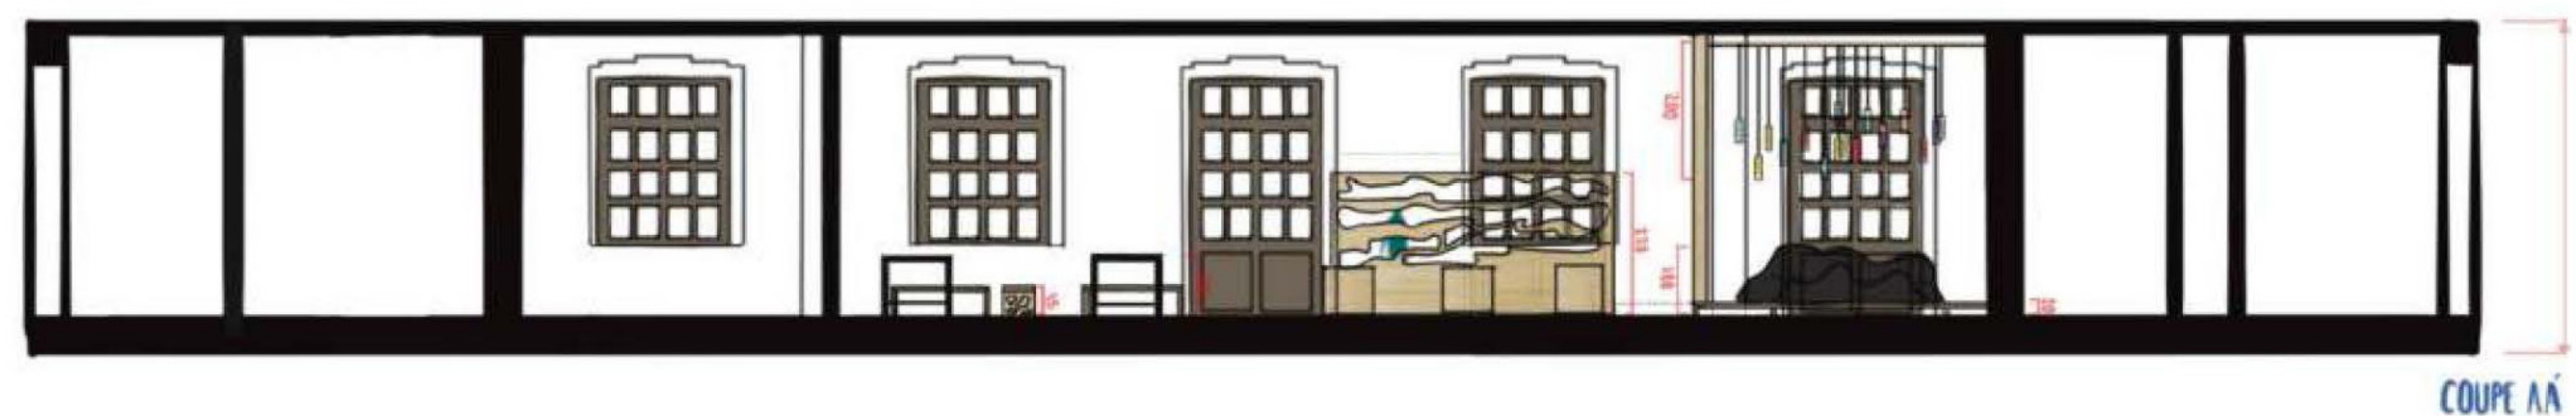

LUMIÈRE MATINALE


DOUCHE QUOTIDIENNE, CONFORT OPTIMAL

Lieu : Vincennes, France (projet fictif)

Contexte : Création d'une salle de bain optimisée autour de la lumière naturelle et du confort

Durée : Projet personnel – 2 jours

Ce projet de salle de bain propose un aménagement fluide et fonctionnel, avec un **mobilier entièrement encastré**. L'espace est structuré autour d'un **plafond incliné** et de **trois velux** qui laissent entrer la lumière du matin, idéale pour commencer la journée sous la chaleur du soleil. La circulation est optimisée grâce à de nombreux rangements discrets, sans encombrement. Une **grande hauteur sous plafond** au niveau de la douche renforce la sensation d'espace et de confort.

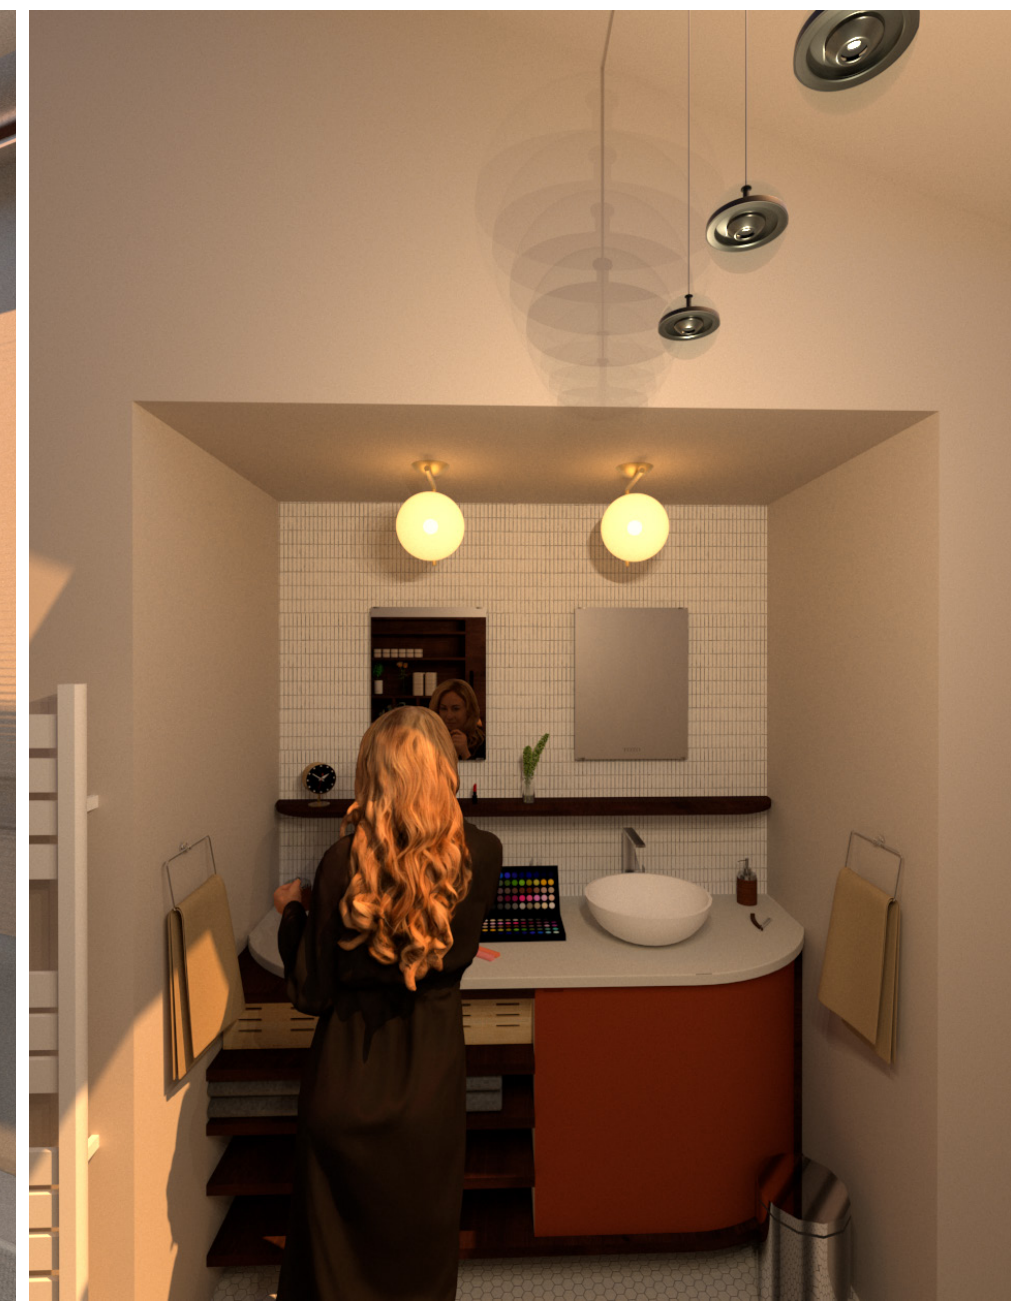

SOAPBOTTLE

UN STAND MINIMALISTE AU SERVICE D'UN PRODUIT DURABLE

Lieu : Paris, France (projet fictif - stand d'exposition)


Contexte : Réflexion autour de la scénographie produit dans un environnement éphémère et modulable

Durée : Projet académique (en binôme) – 1 semaine


Réalisé dans le cadre d'un projet de stand, cet espace met en valeur un produit **écoresponsable** autour d'un **concept minimaliste**. L'enjeu était de concevoir une **structure légère**, modulaire et facilement identifiable dans un contexte d'exposition. L'espace est optimisé pour la présentation produit tout en respectant une cohérence visuelle et environnementale.




PLAN & ÉLÉVATION EN CENTIMÈTRES

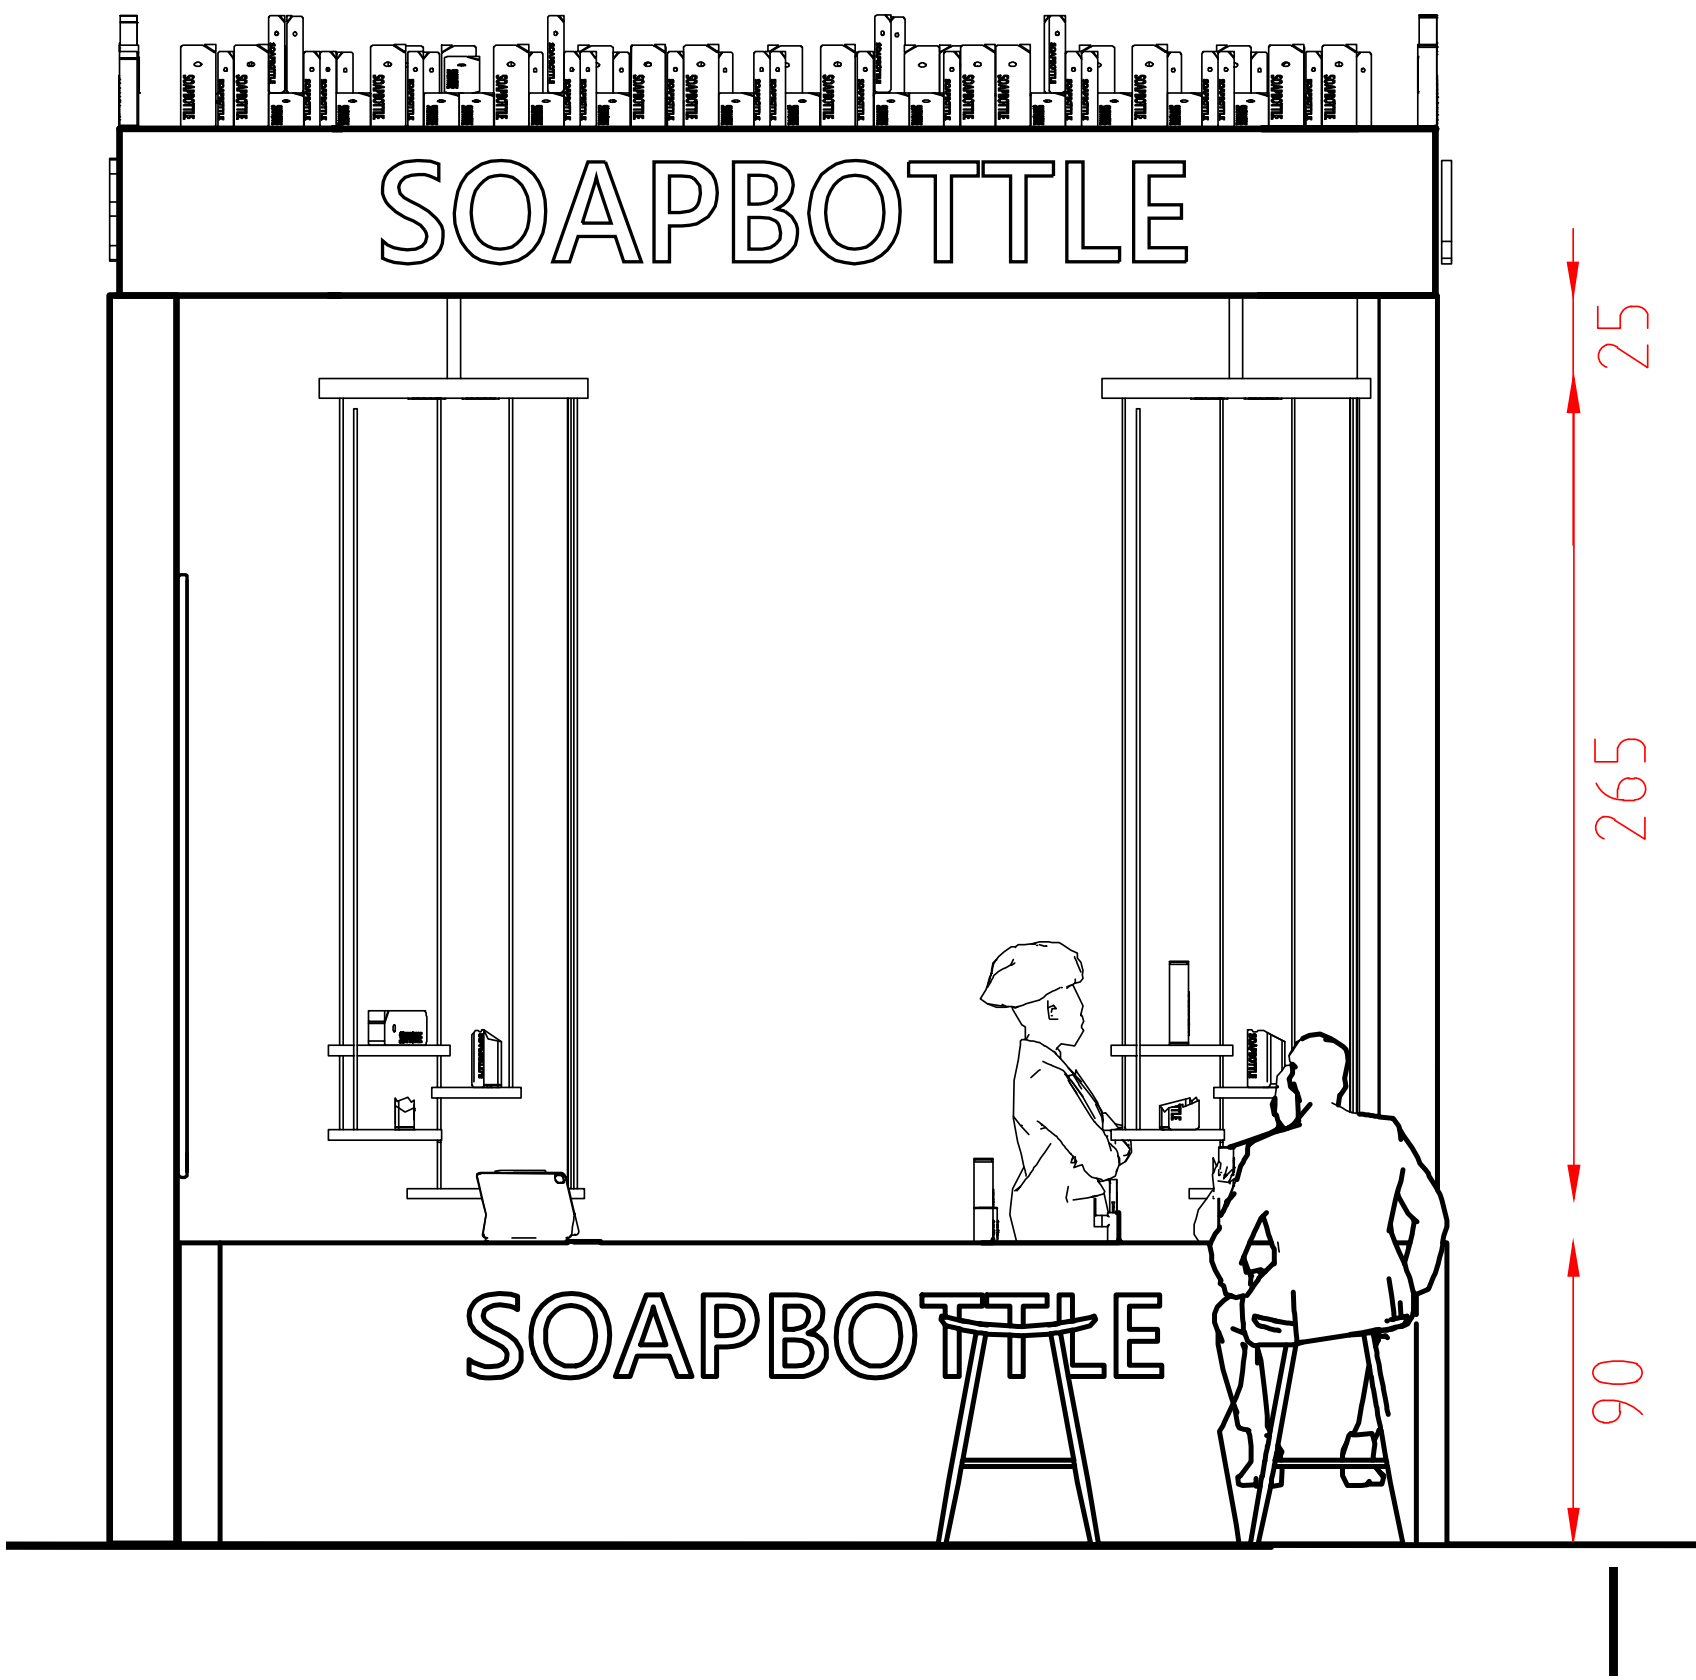

ÉLÉVATION

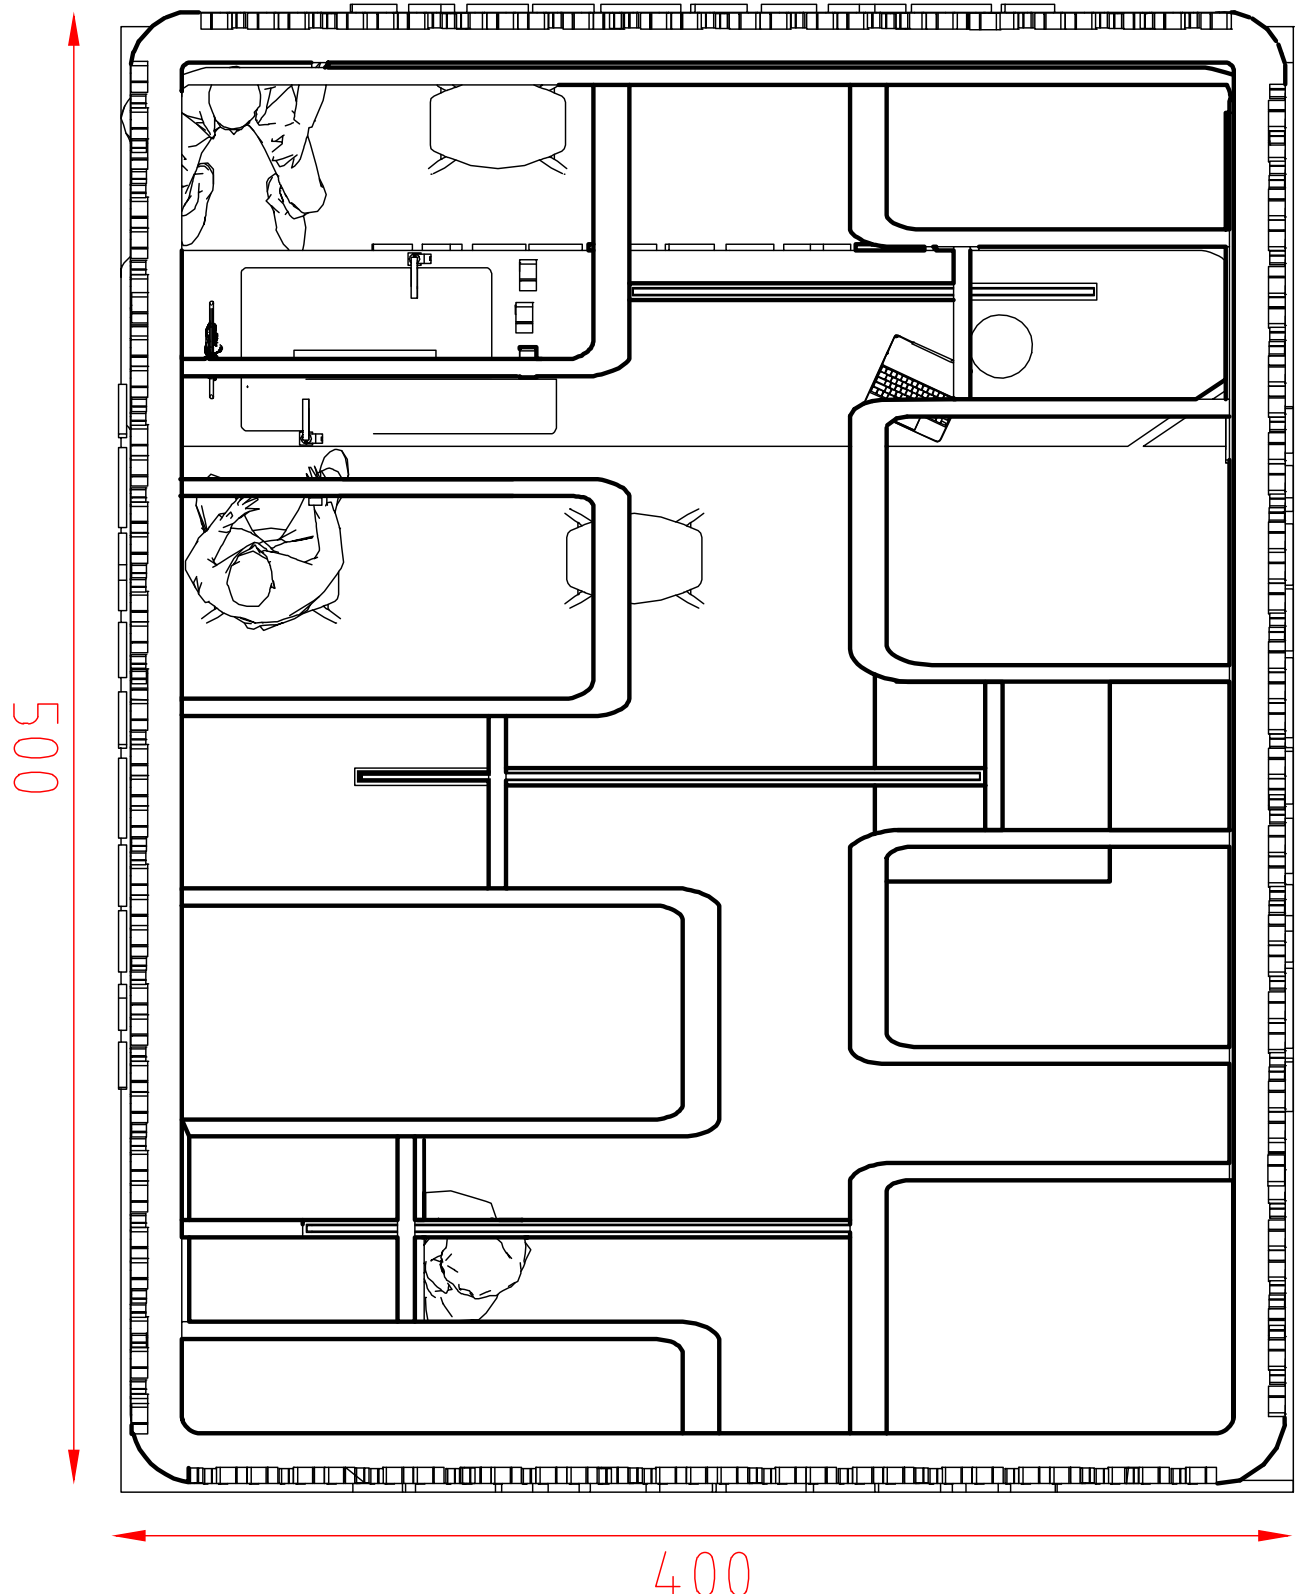

PLAN

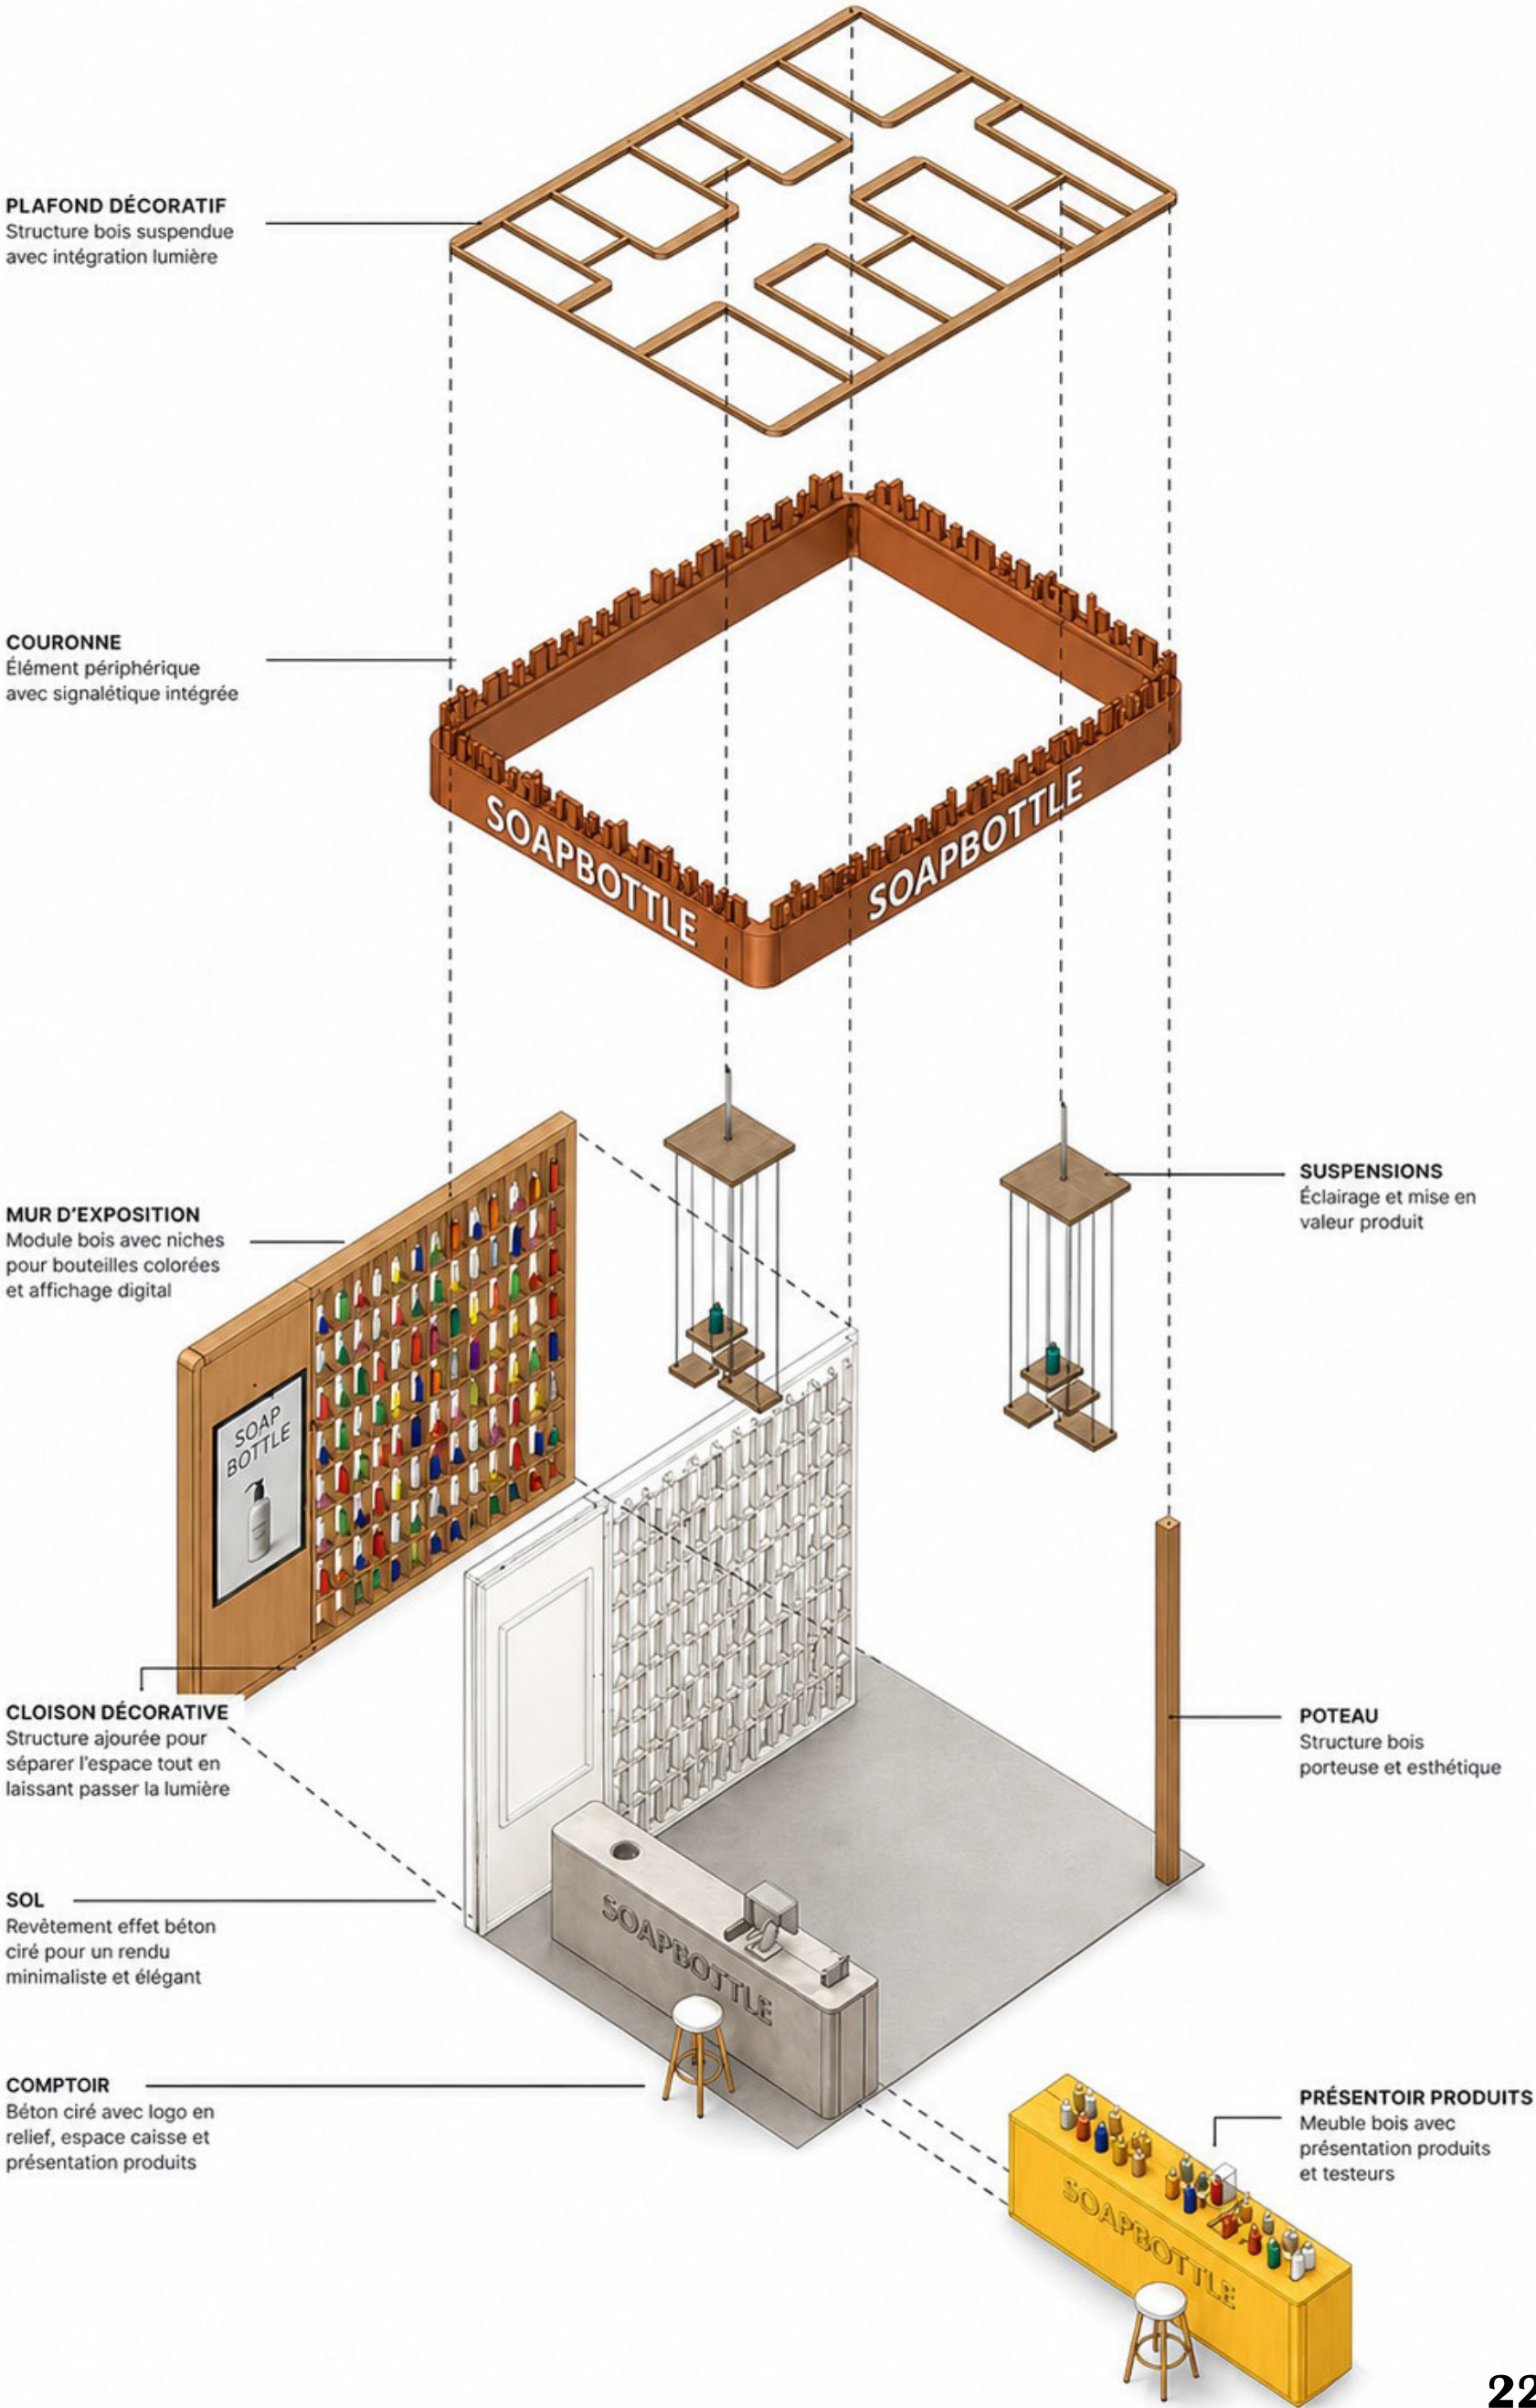

CABINET

UN CABINET MÉDICAL PENSÉ AUTOUR DU CONFORT ET DE LA CIRCULATION

Lieu : Grasse, France

Contexte : Réaménagement d'un cabinet médical avec une attention portée à la circulation et à l'ambiance

Durée : Projet professionnel – 4 semaines

Ce projet de réaménagement d'un **cabinet médical** propose une nouvelle organisation des espaces pour répondre aux besoins des praticiens et des patients. Il intègre des **zones d'attente**, des **cabinets de consultation**, des **espaces techniques** et une circulation logique. Le choix des matériaux et des couleurs a été guidé par une volonté de créer un environnement **rassurant et fonctionnel**.



ESPACES RÉSERVÉS AUX MÉDECINS

CUISINE

WC

WC PMR


CABINET 3

SALLE D'ATTENTE

ENTRÉE

CABINET 1

CABINET 2

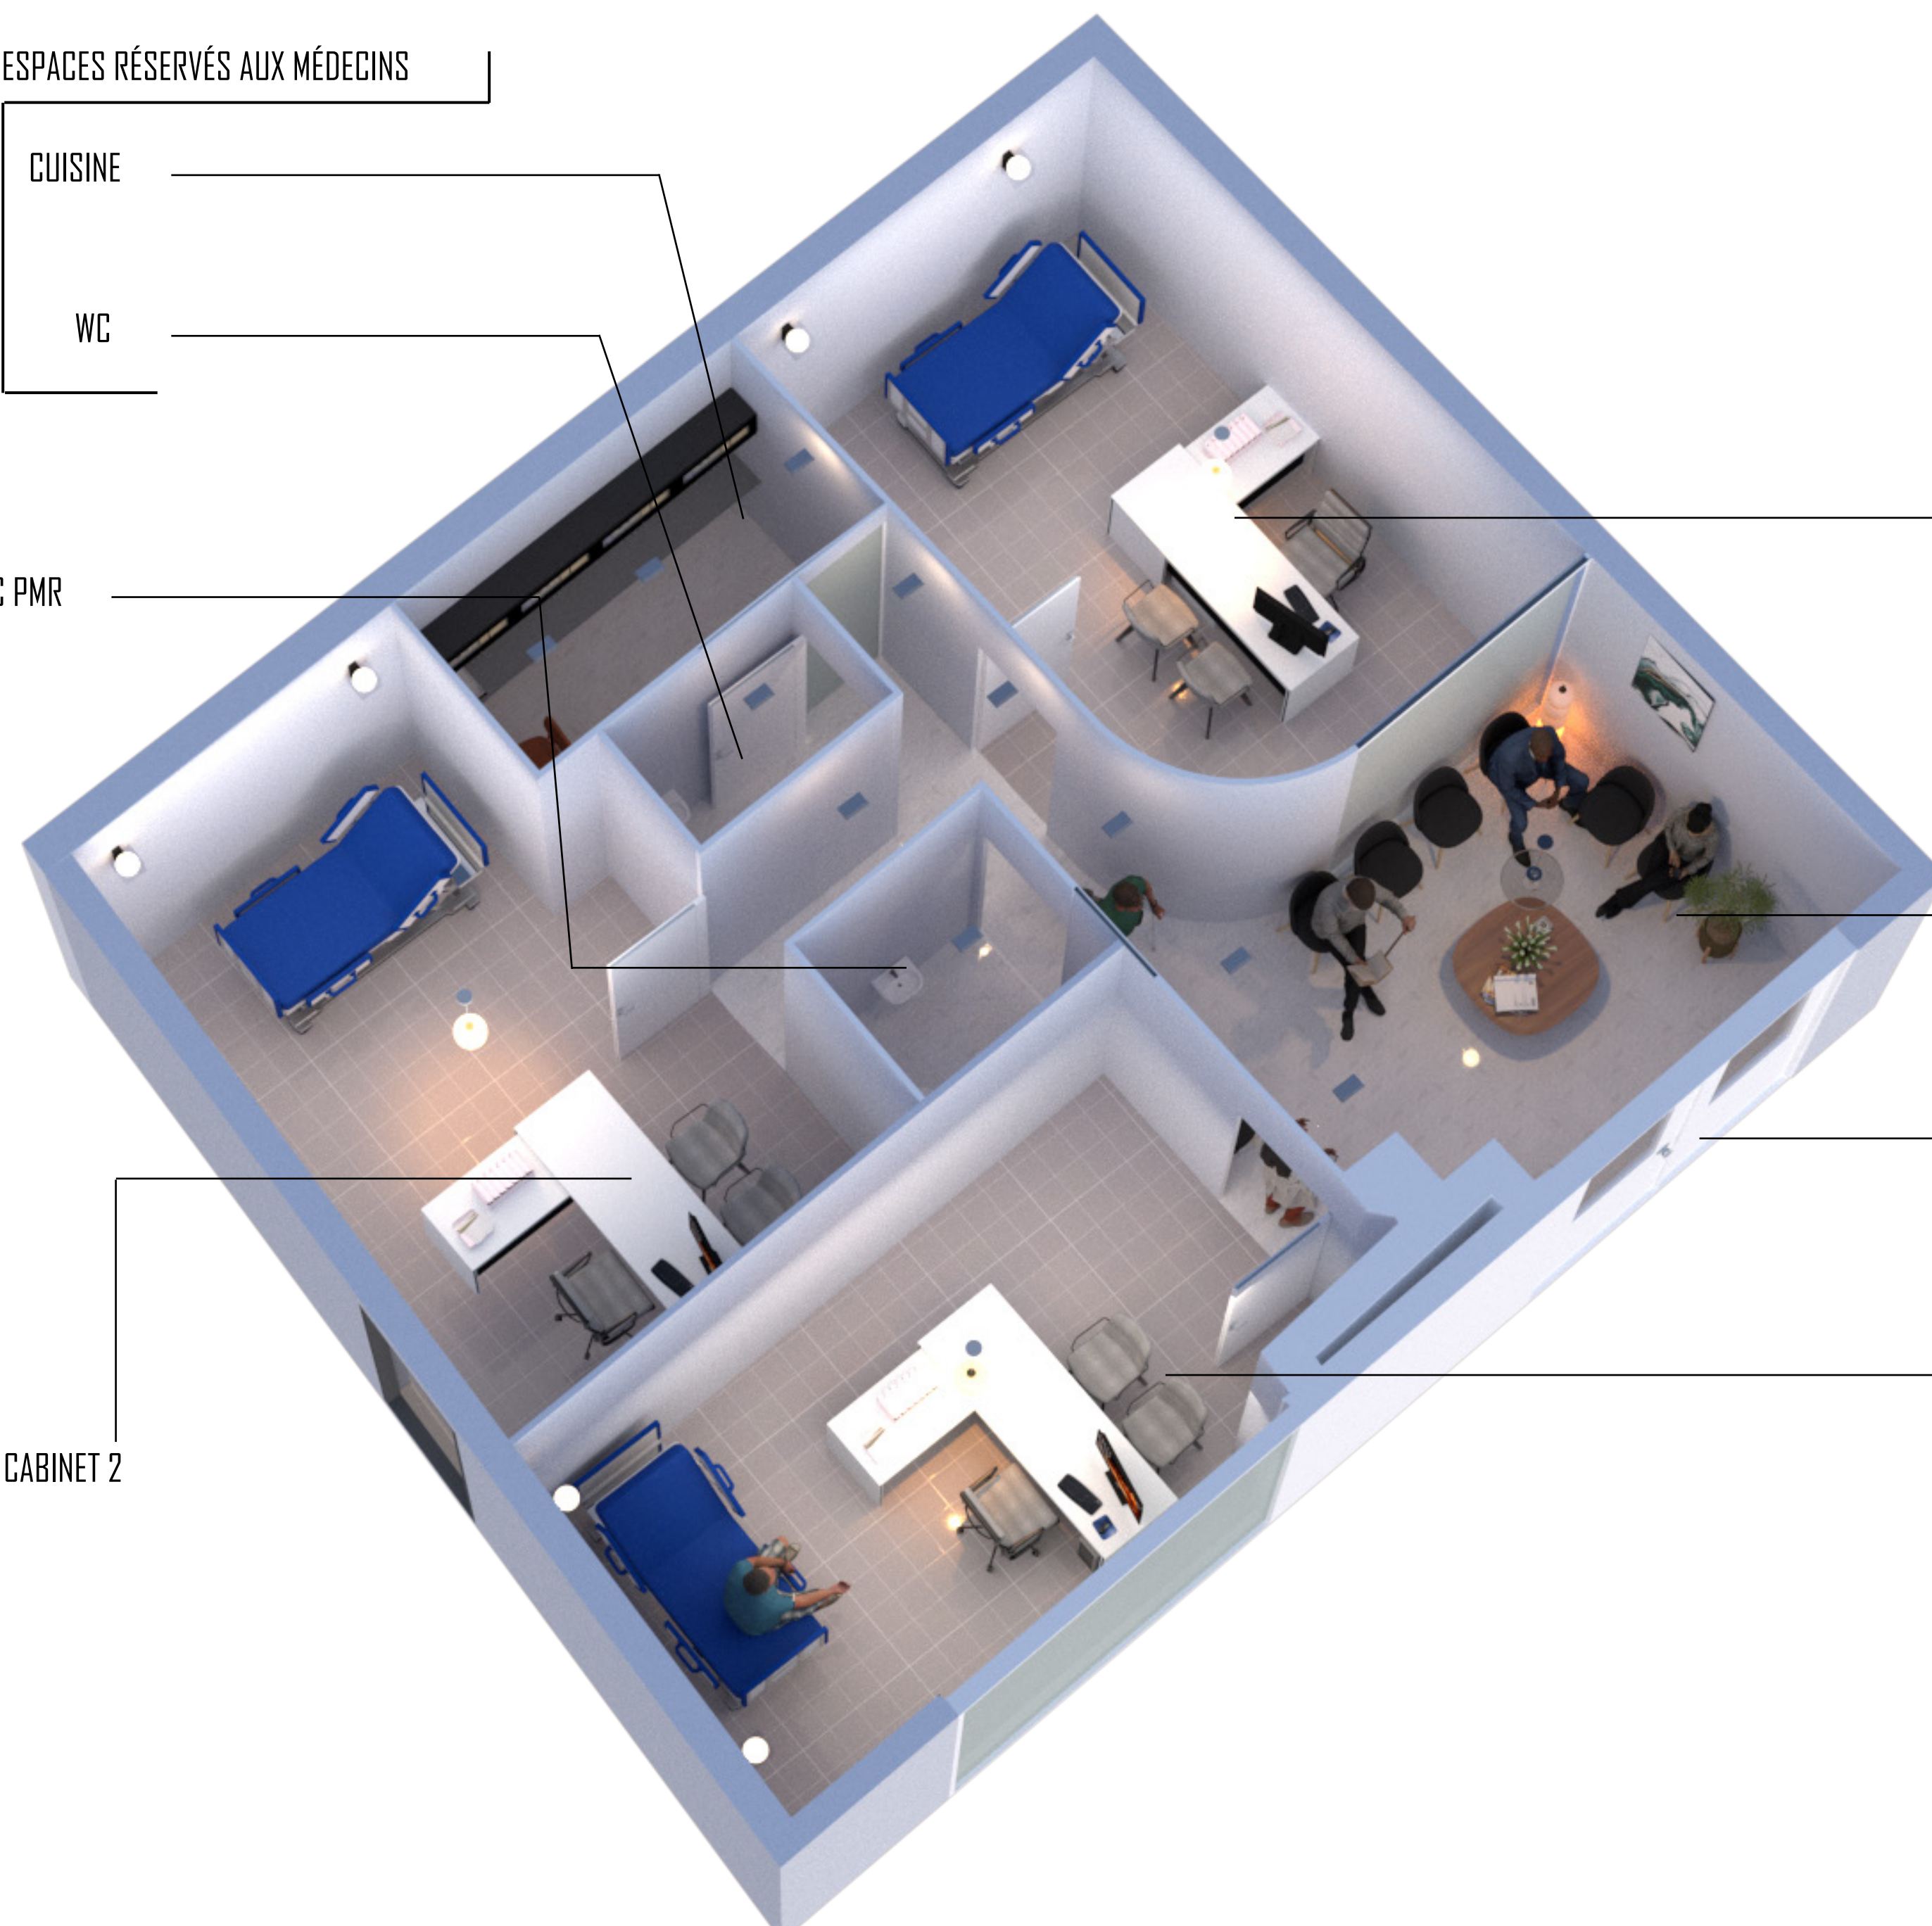

MERCI

07 81 37 22 90

maeva.theolade.pro@gmail.com